



Лист	Наименование	Примечание	Лист	Наименование	Примечание
1	Состав проекта		41	Визуализация спальни	
2	План обмера помещений		42	Визуализация детской комнаты	
3	План демонтажа		43	Визуализация детской комнаты	
4	План монтажа		44	Визуализация детской комнаты	
5	План перепланировки		45	Визуализация детской комнаты	
6	План монтажа конструкций		46	Визуализация детской комнаты	
7	У1, У2, У3.		47	Визуализация санузла	
8	План сантехники		48	Визуализация санузла	
9	План розеток и выключателей		49	Визуализация санузла	
10	План привязки светильников				
11	План включения светильников				
12	План отделки стен				
13	План тёплых полов				
14	План напольных покрытий				
15	План дверей				
16	План напольных плинтусов				
17	План потолков				
18	План расстановки мебели				
19	План расстановки мебели с указанием развёрток стен				
20	Развёртки стен R1, R2, R3.				
21	Развёртки стен R4, R5, R6, R7, R8.				
22	Развёртки стен R9, R10, R11, R12, Раскладка плитки.				
23	Развёртки стен R13, R14, R15.				
24	Развёртки стен R16, R17, R18.				
25	Развёртки стен R19.				
26	Спецификации				
27	Спецификации				
28	3D эскизы				
29	3D эскизы				
30	3D эскизы				
31	Визуализация кухни-гостиной				
32	Визуализация кухни-гостиной				
33	Визуализация кухни-гостиной				
34	Визуализация кухни-гостиной				
35	Визуализация кухни-гостиной				
36	Визуализация кухни-гостиной				
37	Визуализация кухни-гостиной				
38	Визуализация кухни-гостиной				
39	Визуализация спальни				
40	Визуализация спальни				

		Дизайн-проект квартиры по ул. Миля 9	Стадия	Лист	Листов
			РП	1	49
Дизайнер	Хворостов А.О.	Состав проекта			
Заказчик	Юлия и Павел				
Согласовано					
Дата	31.07.2026				

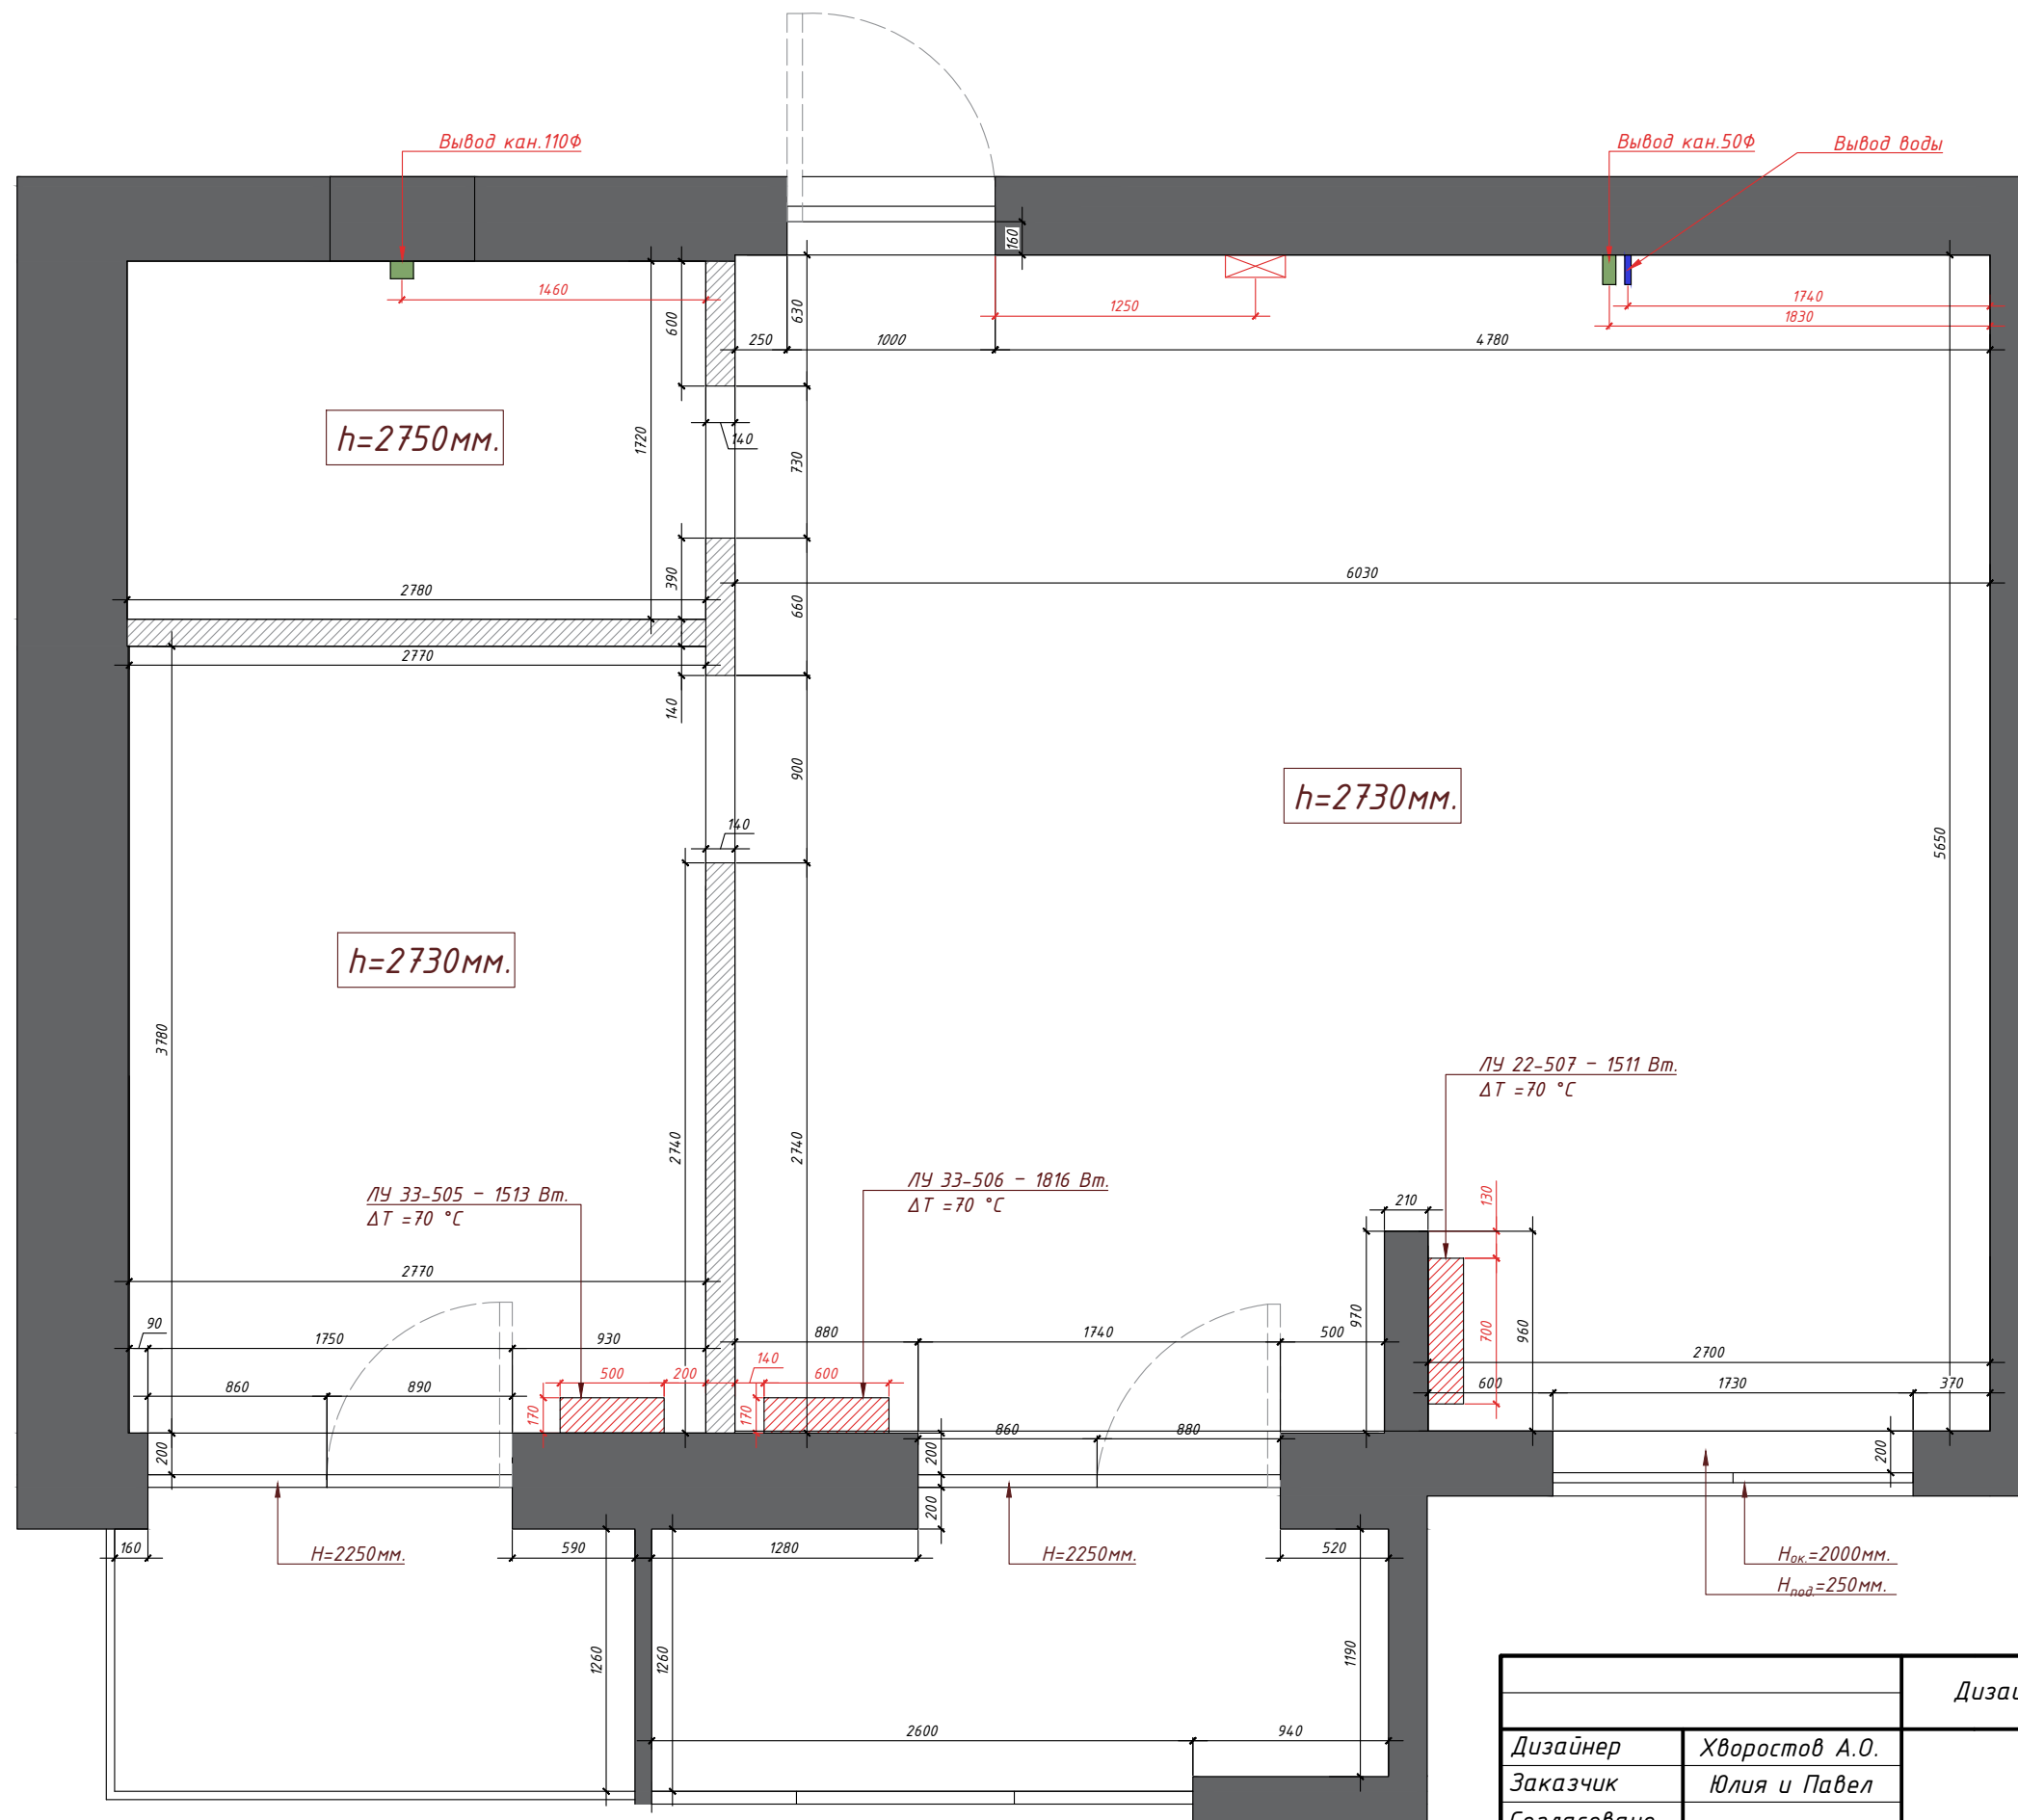

- Примечания:
1. Все размеры указаны с учетом существующей отделки стен.
 2. Допустимая погрешность в обмерах за счет неровности стен...25 мм.
 3. Все размеры окон и дверей даны по проему.
 4. Все высоты даны от чернового пола и потолка


		Дизайн-проект квартиры по ул. Миля 9	Стадия	Лист	Листов
			РП	2	49
Дизайнер	Хворостов А.О.	План обмера помещения (1:35)			
Заказчик	Юлия и Павел				
Согласовано					
Дата	31.07.2026				

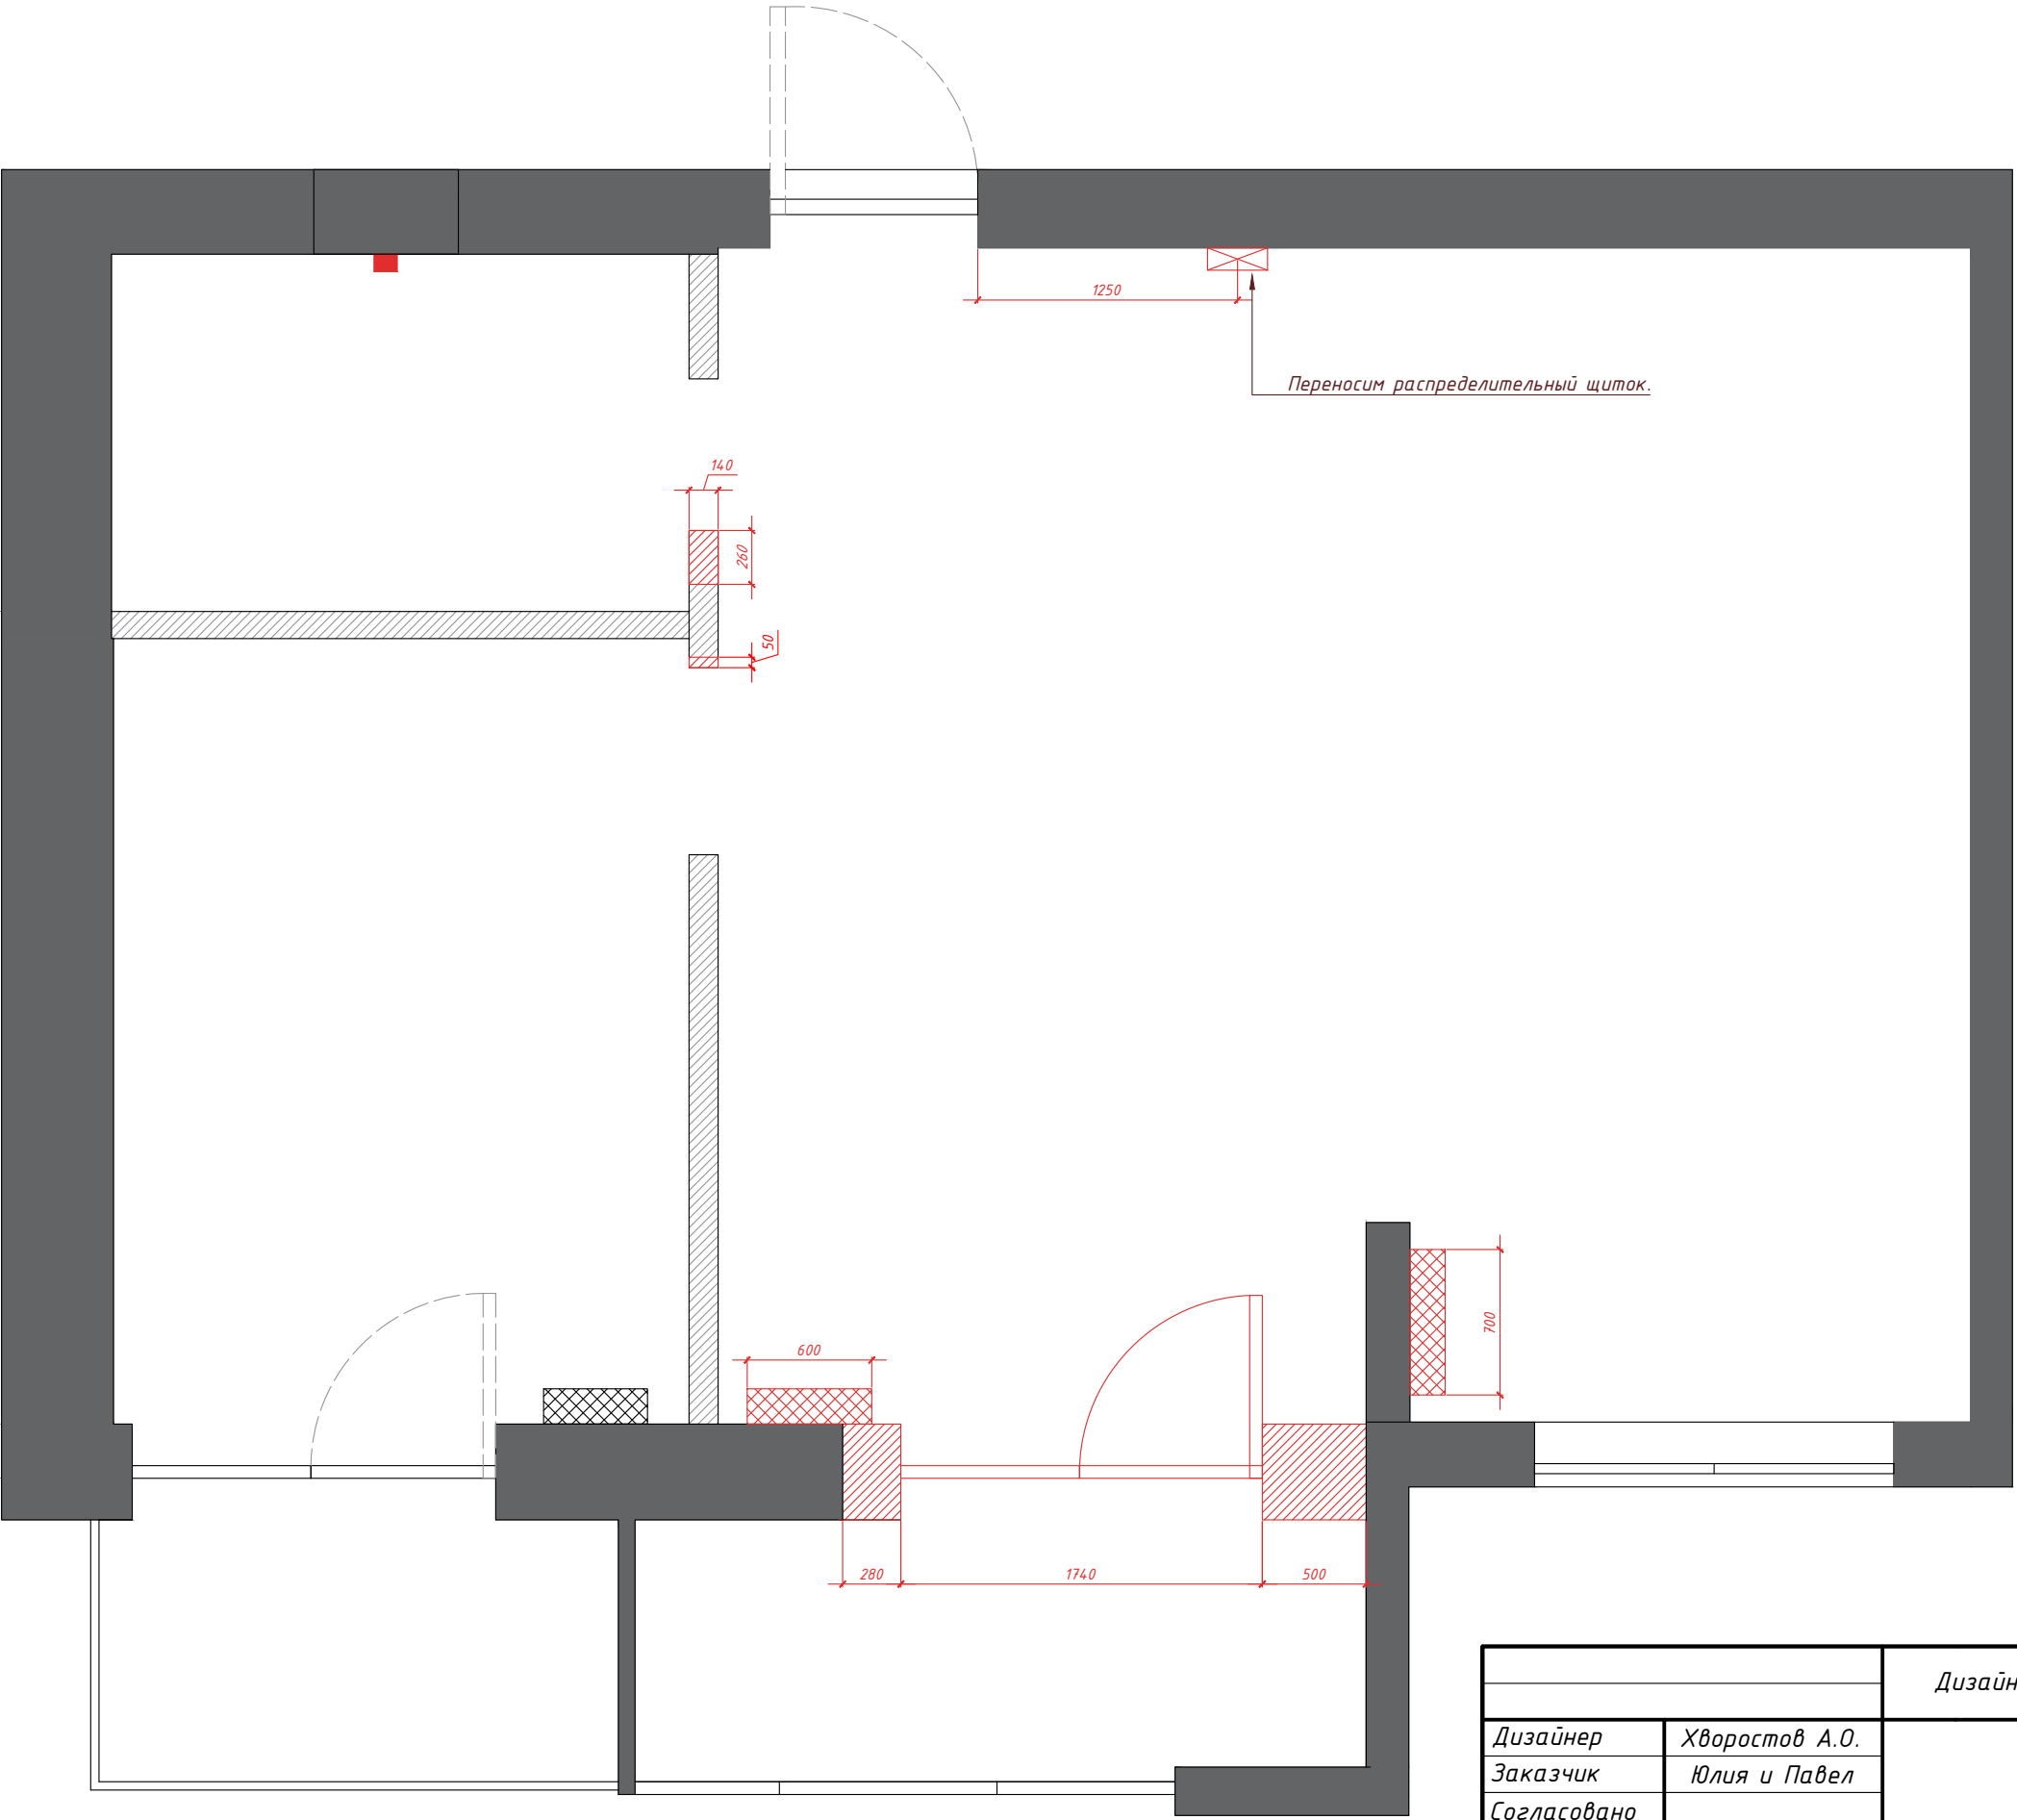

Условные обозначения	
	Несущие стены
	Перегородки
	Демонтируемые перегородки
	Демонтируемые радиаторы
	Демонтируемый эл. щиток

Примечания:
1. Демонтаж стен выполнить согласно рекомендациям специалиста.
2. Необходимо демонтировать все существующие розетки и выключатели, за исключением технических, так как будет проводиться новая электрика.

		Дизайн-проект квартиры по ул. Миля 9	Стадия	Лист	Листов
			РП	3	49
Дизайнер	Хворостов А.О.	План демонтажа (1:35)			
Заказчик	Юлия и Павел				
Согласовано					
Дата	31.07.2026				

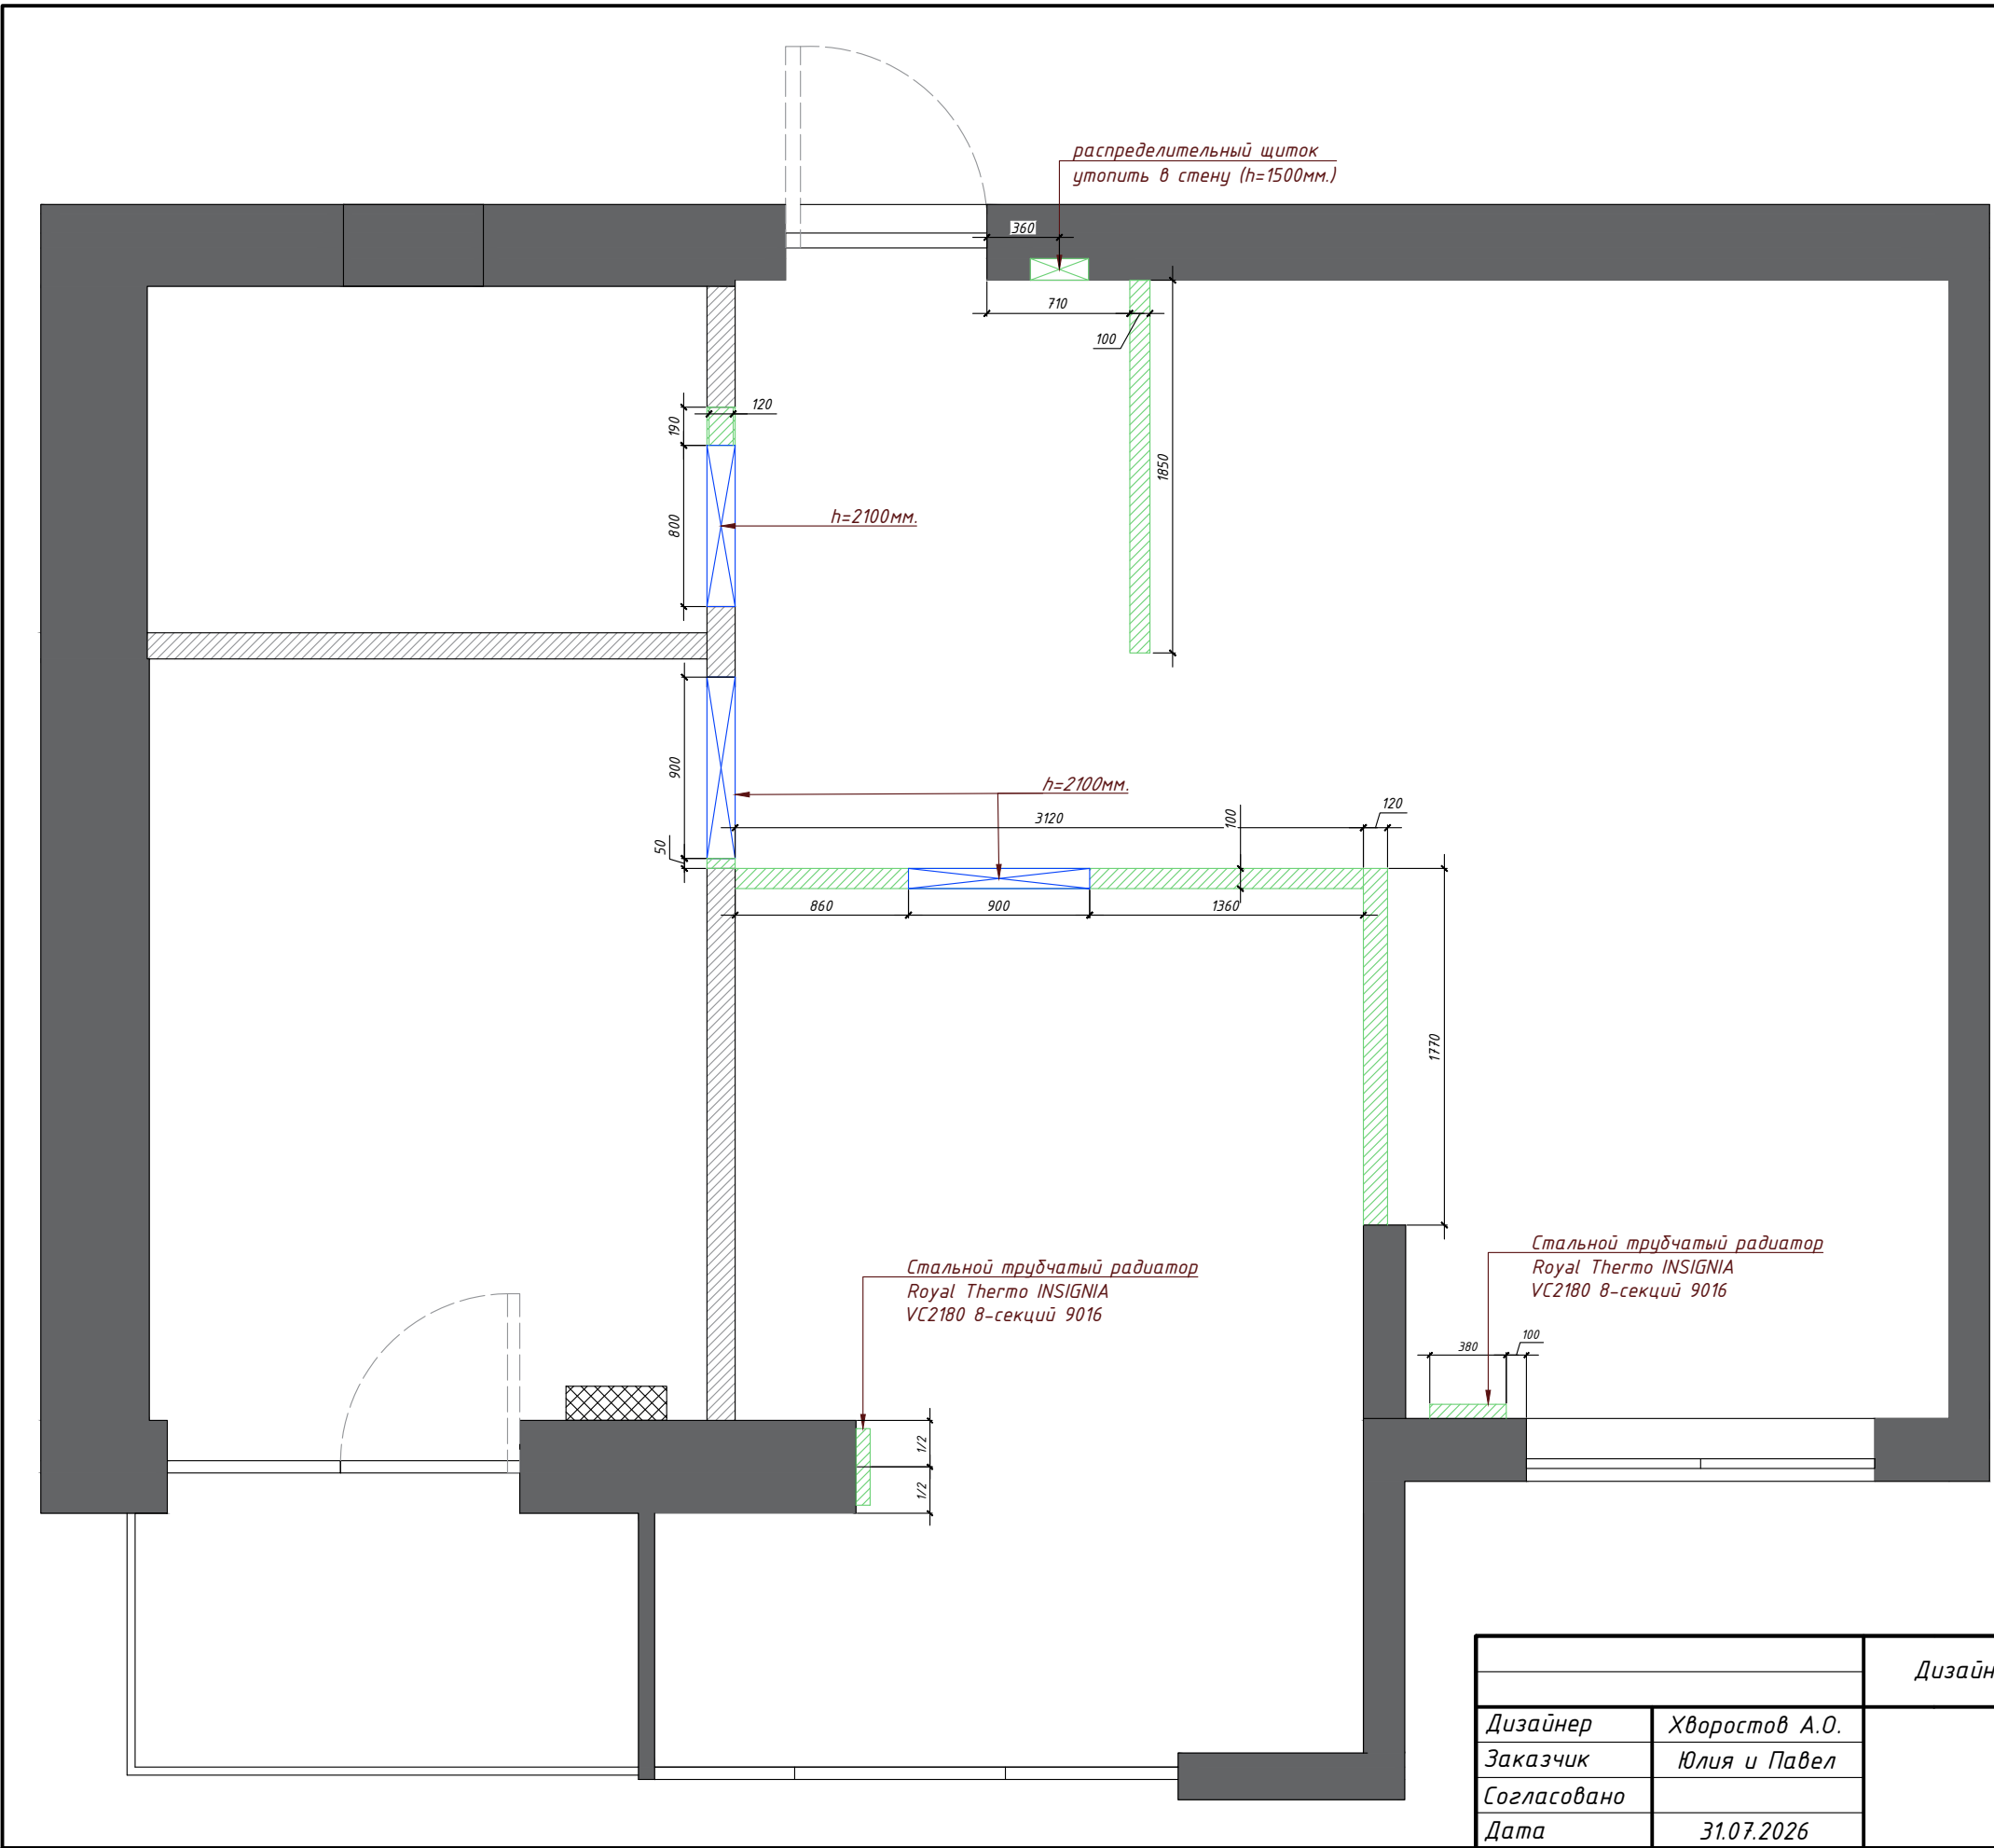

Условные обозначения	
	Несущие стены
	Перегородки
	Монтируемые перегородки
	Монтируемые радиаторы
	Монтируемый эл.щиток
	Возводимый дверной проём


Керамзитобетонные блоки
толщиной 120мм. ($S=5.5-V=0,66 \text{ м3}$)

Керамзитобетонные блоки
толщиной 100мм. ($S=11.67-V=1,167 \text{ м3}$)

Примечание:

1. Новые перегородки и конструкции в помещениях с повышенной влажностью возвести из керамзитобетонного блока.
2. Все размеры новых перегородок даны по блоку, без учета выравнивающего штукатурного слоя
3. Размеры новых дверей даны по проему от уровня существующей стяжки пола и без учета чистового покрытия.
4. Размеры дверных проемов могут быть изменены согласно рекомендациям производителя дверей.
5. Все объемы по материалам посчитаны без учета запаса. Для определения общего количества материалов, просчетов сметной стоимости и определения общего объема работ обязателен перерасчет со специалистом по месту.
6. В санузле выполнить обмазочную гидроизоляцию пола и стен. Монтаж подвесных конструкций осуществлять при помощи гидроизолирующих герметиков.
7. Допустимая погрешность в размерах 25 мм. При большей погрешности, по факту, скорректировать все размеры по месту на усмотрение строительно-монтажной бригады, согласовать изменения с заказчиком или представителем авторского надзора, или лицом его представляющим.
8. Размер и размещение скрытых сантехнических лючков выполнить по месту, согласно решению специалиста.
9. Все наращивание и зашивки стен для прокладки коммуникаций уточнить и скорректировать по месту
10. В местах установки мебельных подвесных конструкций, при необходимости, предусмотреть усиление. Проконсультироваться с специалистом по мебели перед проведением монтажных и отделочных работ

		Дизайн-проект квартиры по ул. Миля 9	Стадия	Лист	Листов
			РП	4	49
Дизайнер	Хворостов А.О.	План монтажа (1:35)			
Заказчик	Юлия и Павел				
Согласовано					
Дата	31.07.2026				

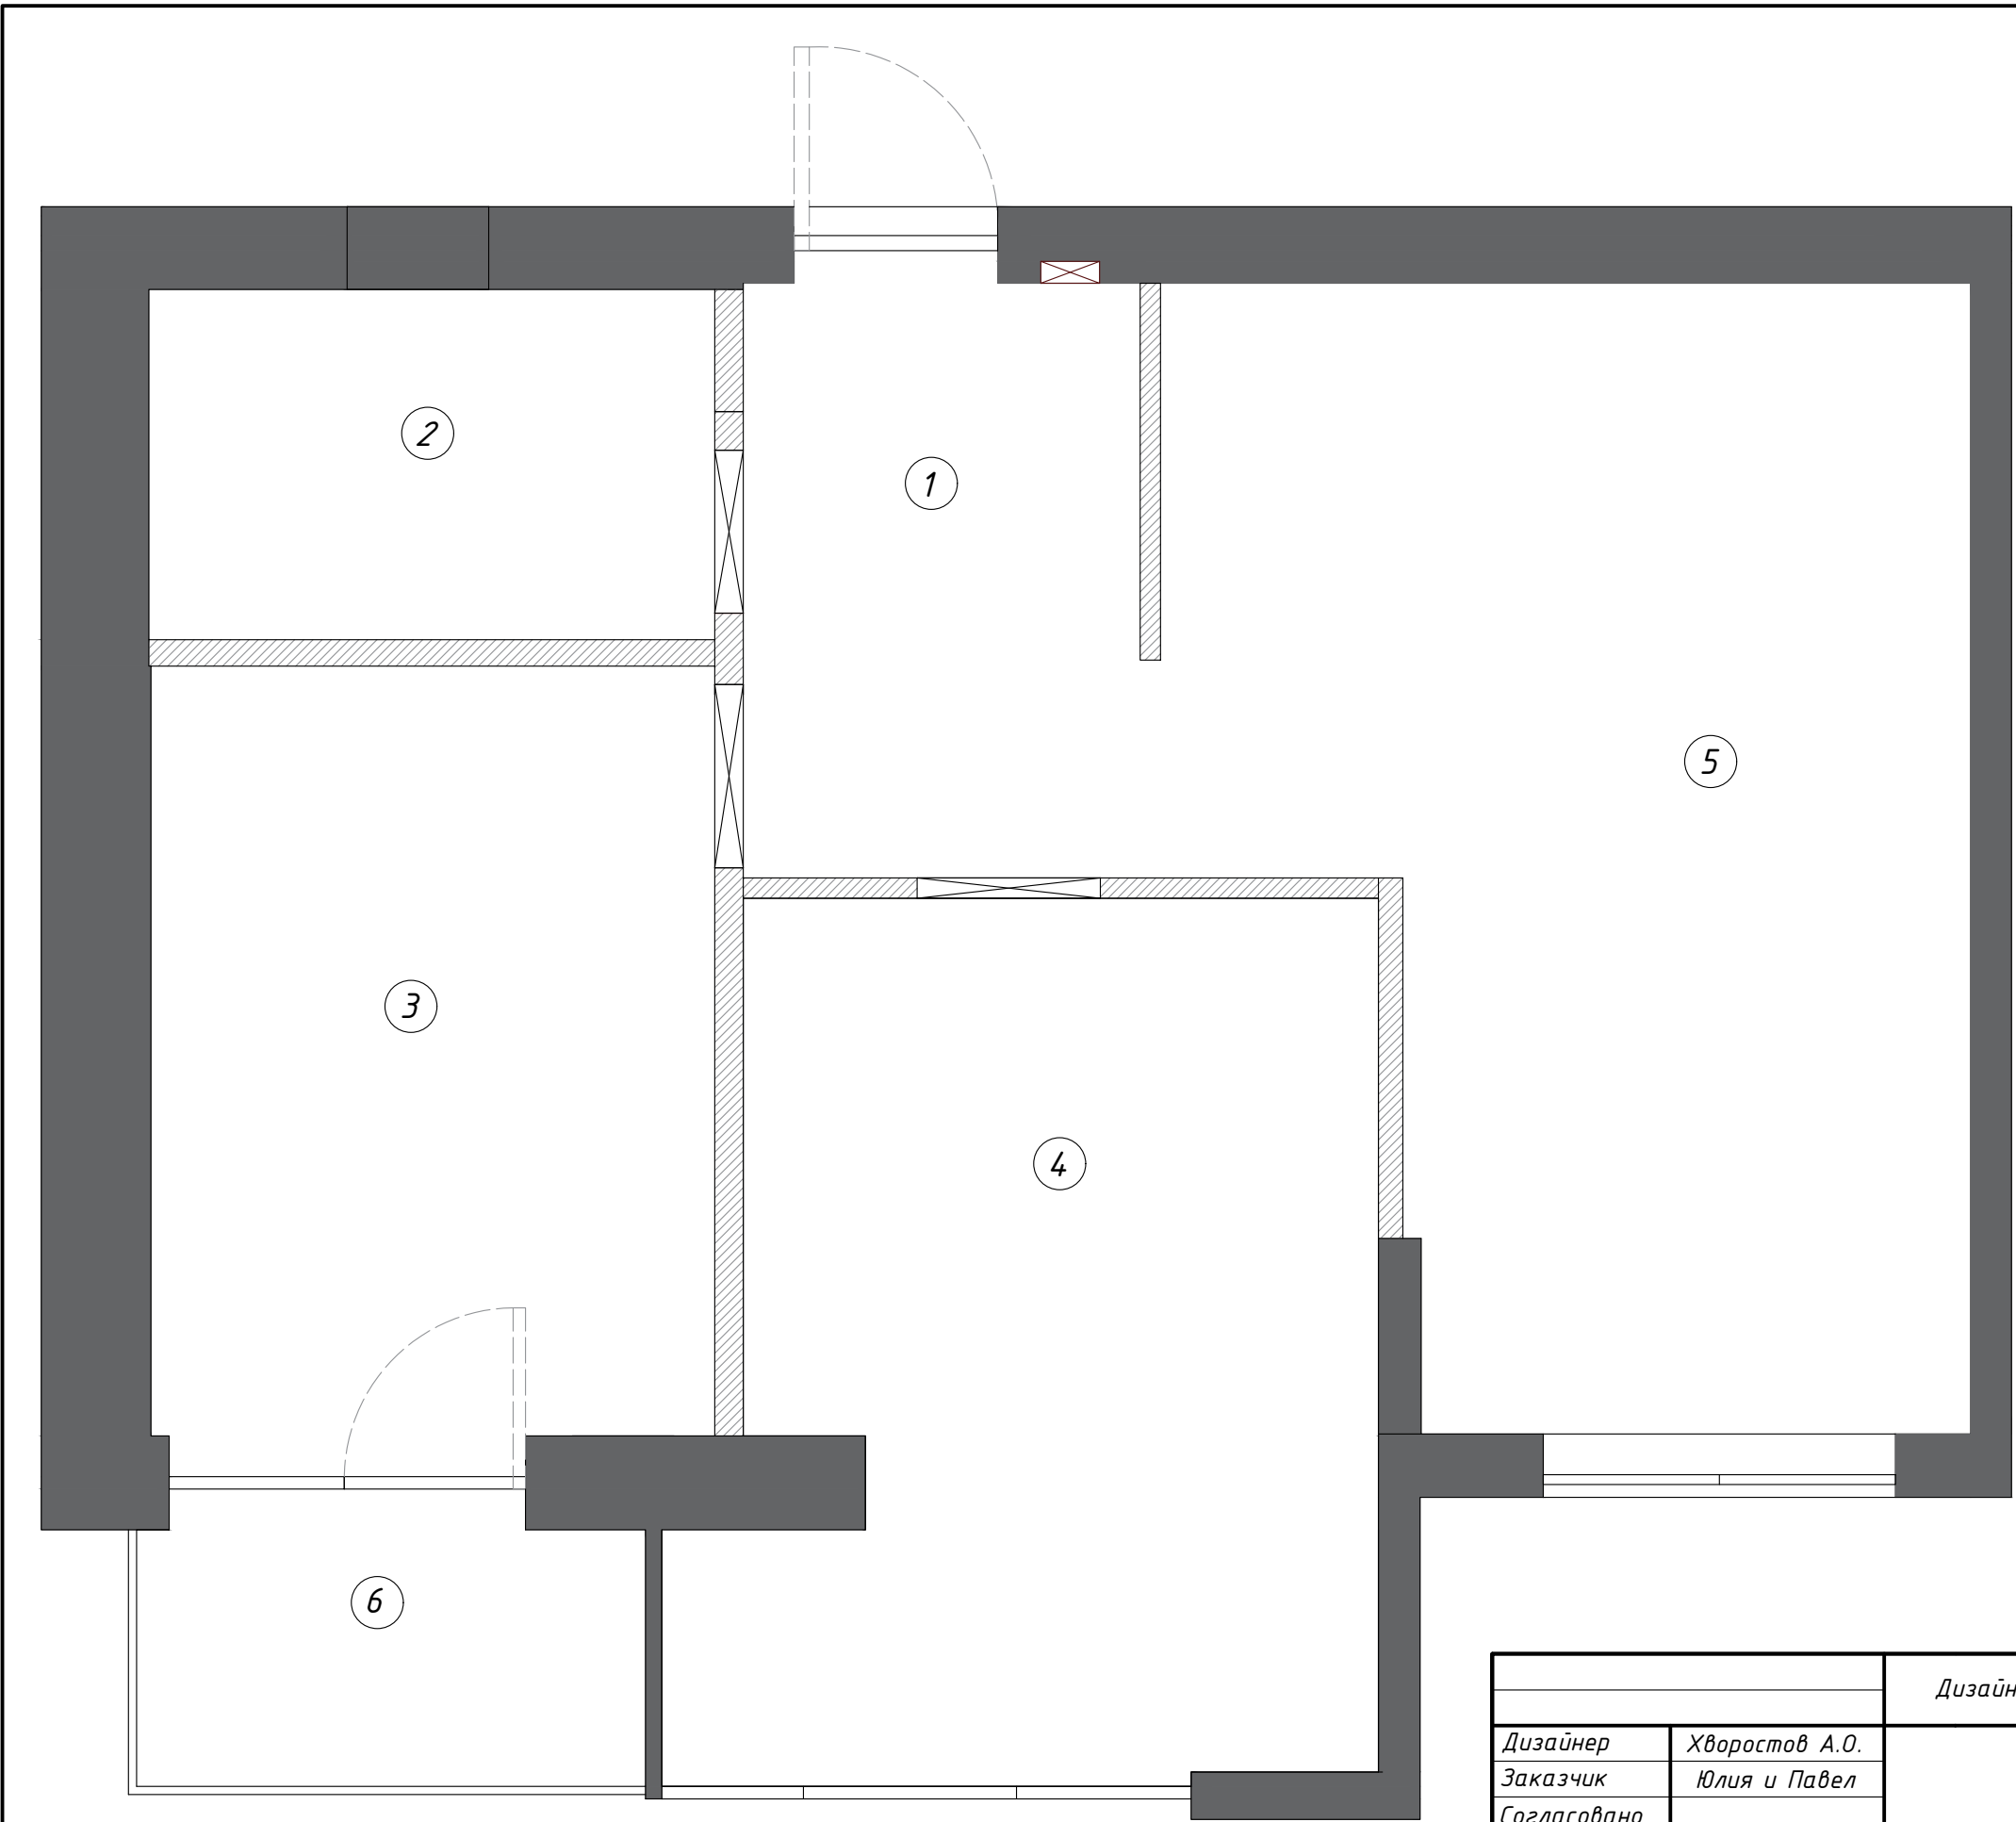







Условные обозначения	
	Несущие стены
	Перегородки
	Радиаторы
	Эл.щиток
	Дверной проём

Экспликация помещений		
1.	Прихожая	S=5,69 м²
2.	Санузел	S=4,78 м²
3.	Спальня	S=10,50 м²
4.	Детская комната	S=13,76 м²
5.	Кухня-гостиная	S=19,15 м²
6.	Балкон	S=3,15 м²


Примечание:
1. Все размеры даны без учёта выравнивающего штукатурного слоя 10-30мм.
2. Все высоты даны от уровня чистовой стяжки пола
3. Допустимая погрешность в размерах 20 мм. При большей погрешности, по факту, скорректировать размеры по месту на усмотрение строительно-монтажной бригады, согласовать изменения с заказчиком или представителем авторского надзора, или лицом его представляющим.

		Дизайн-проект квартиры по ул. Миля 9	Стадия	Лист	Листов
			РП	5	49
Дизайнер	Хворостов А.О.	План перепланировки (1:35)			
Заказчик	Юлия и Павел				
Согласовано					
Дата	31.07.2026				

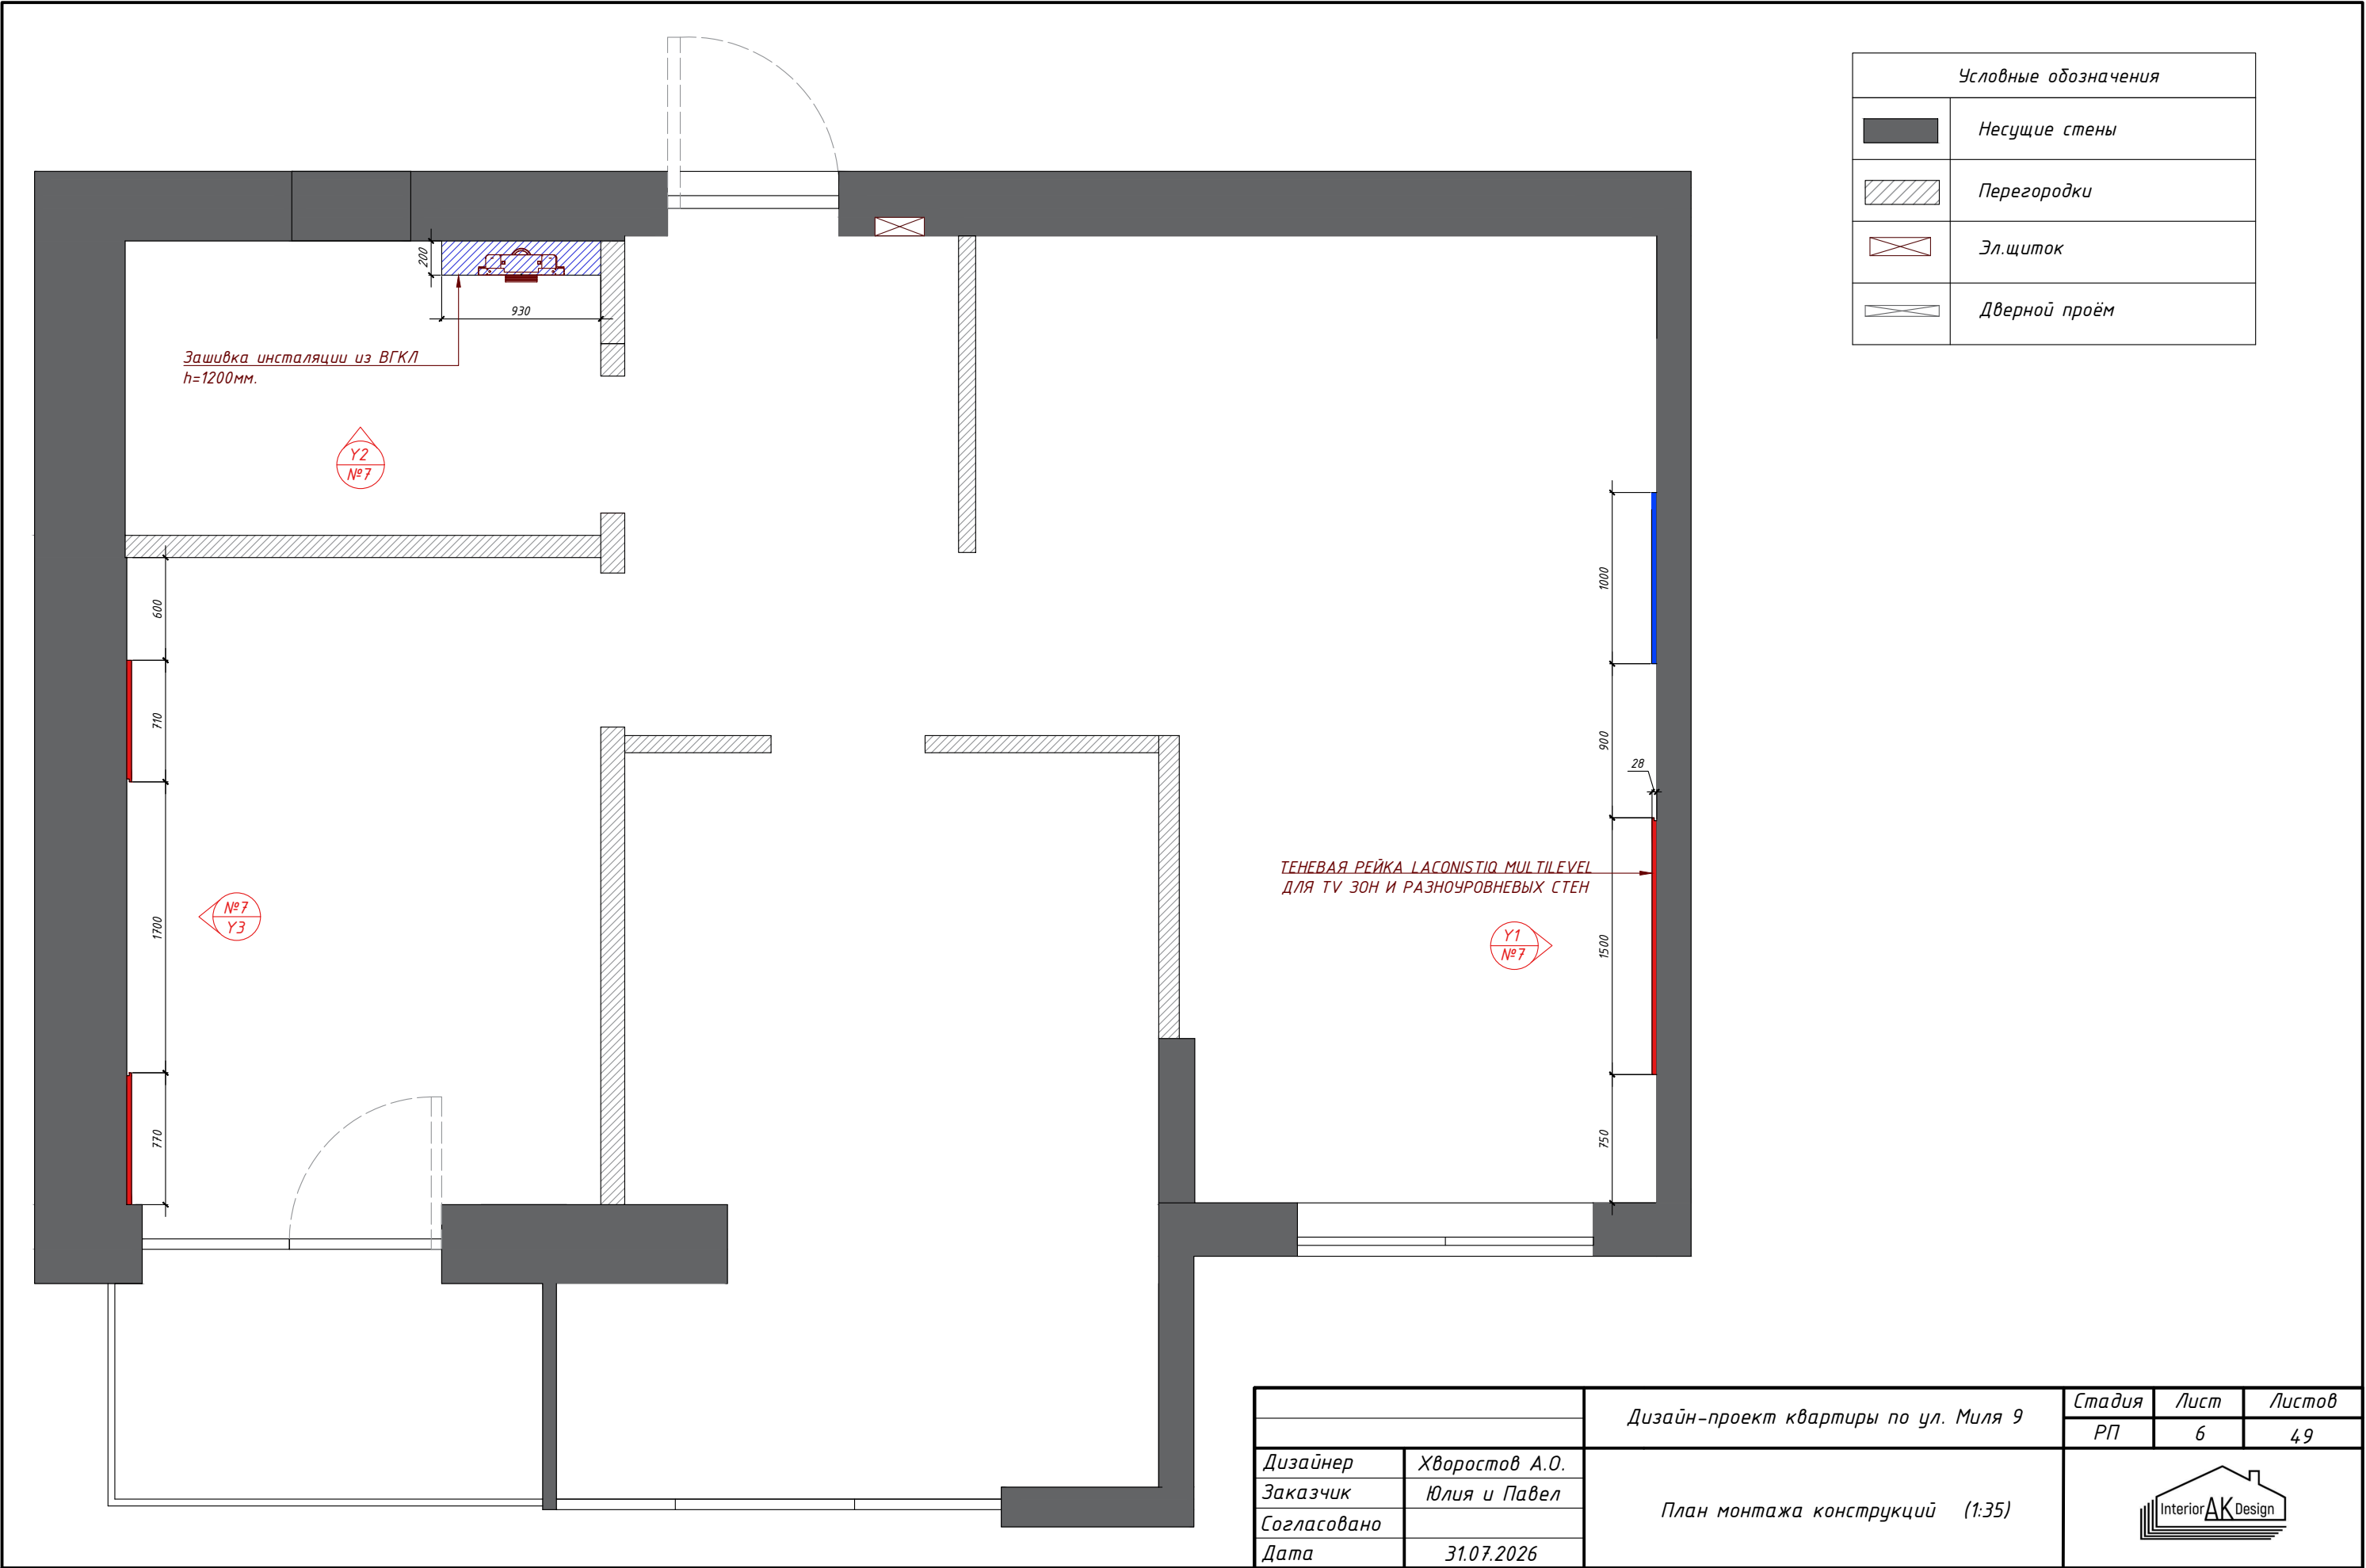

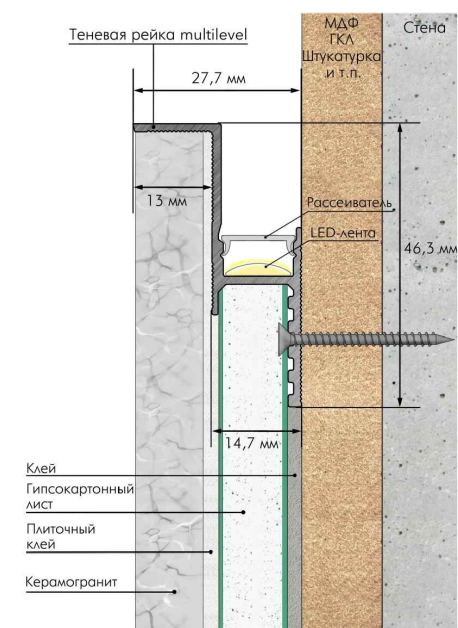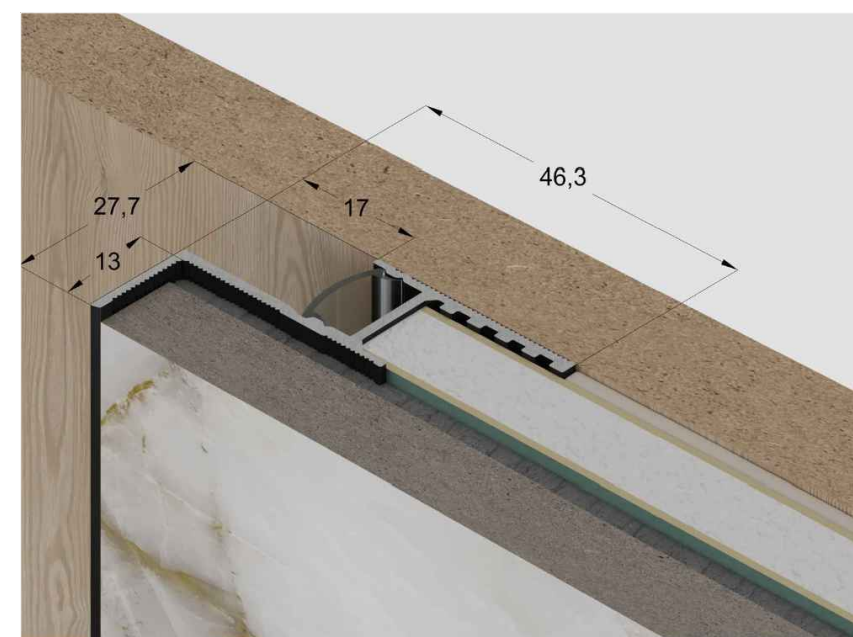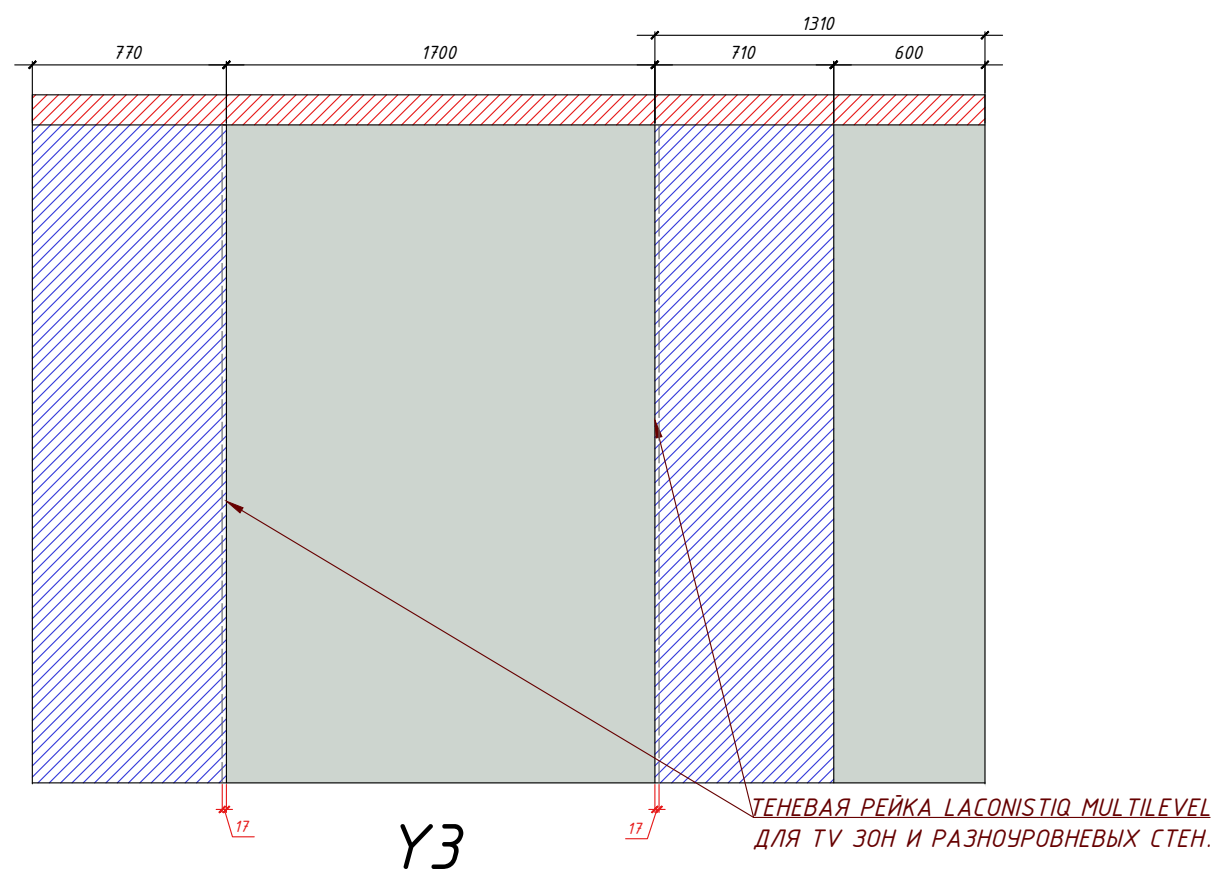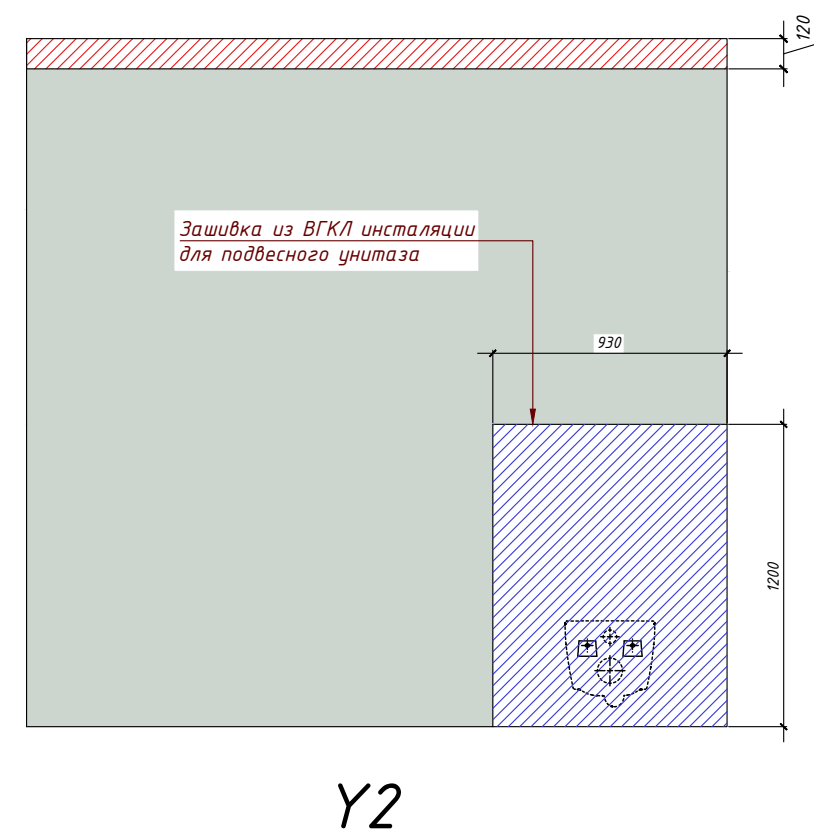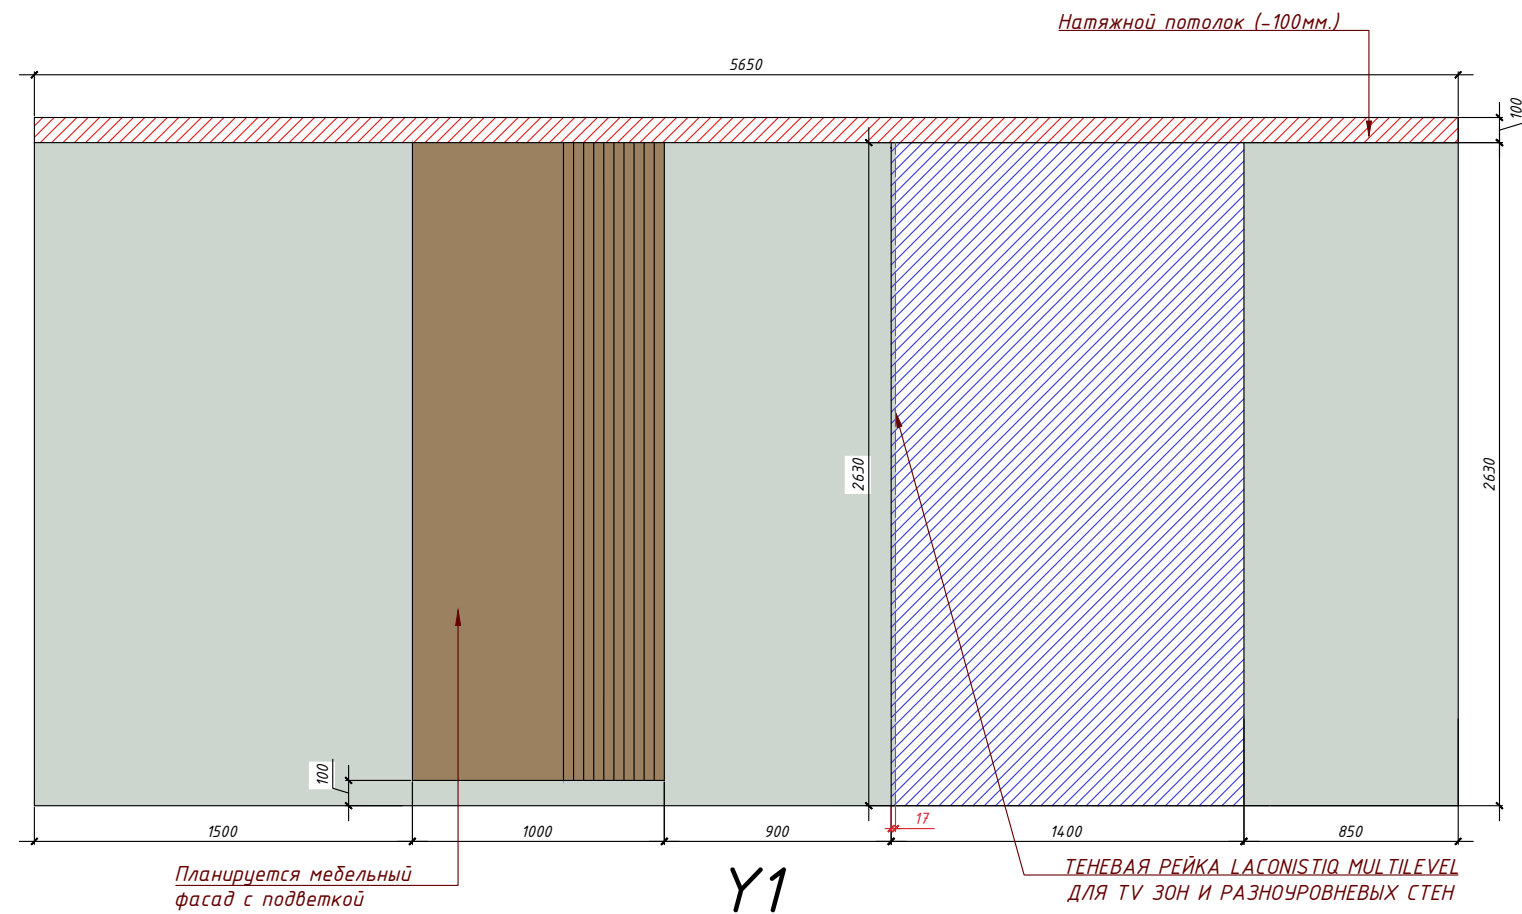


		Дизайн-проект квартиры по ул. Миля 9	Стадия	Лист	Листов
			РП	7	49
Дизайнер	Хворостов А.О.	Y1, Y2, Y3 (1:30)			
Заказчик	Юлия и Павел				
Согласовано					
Дата	31.07.2026				

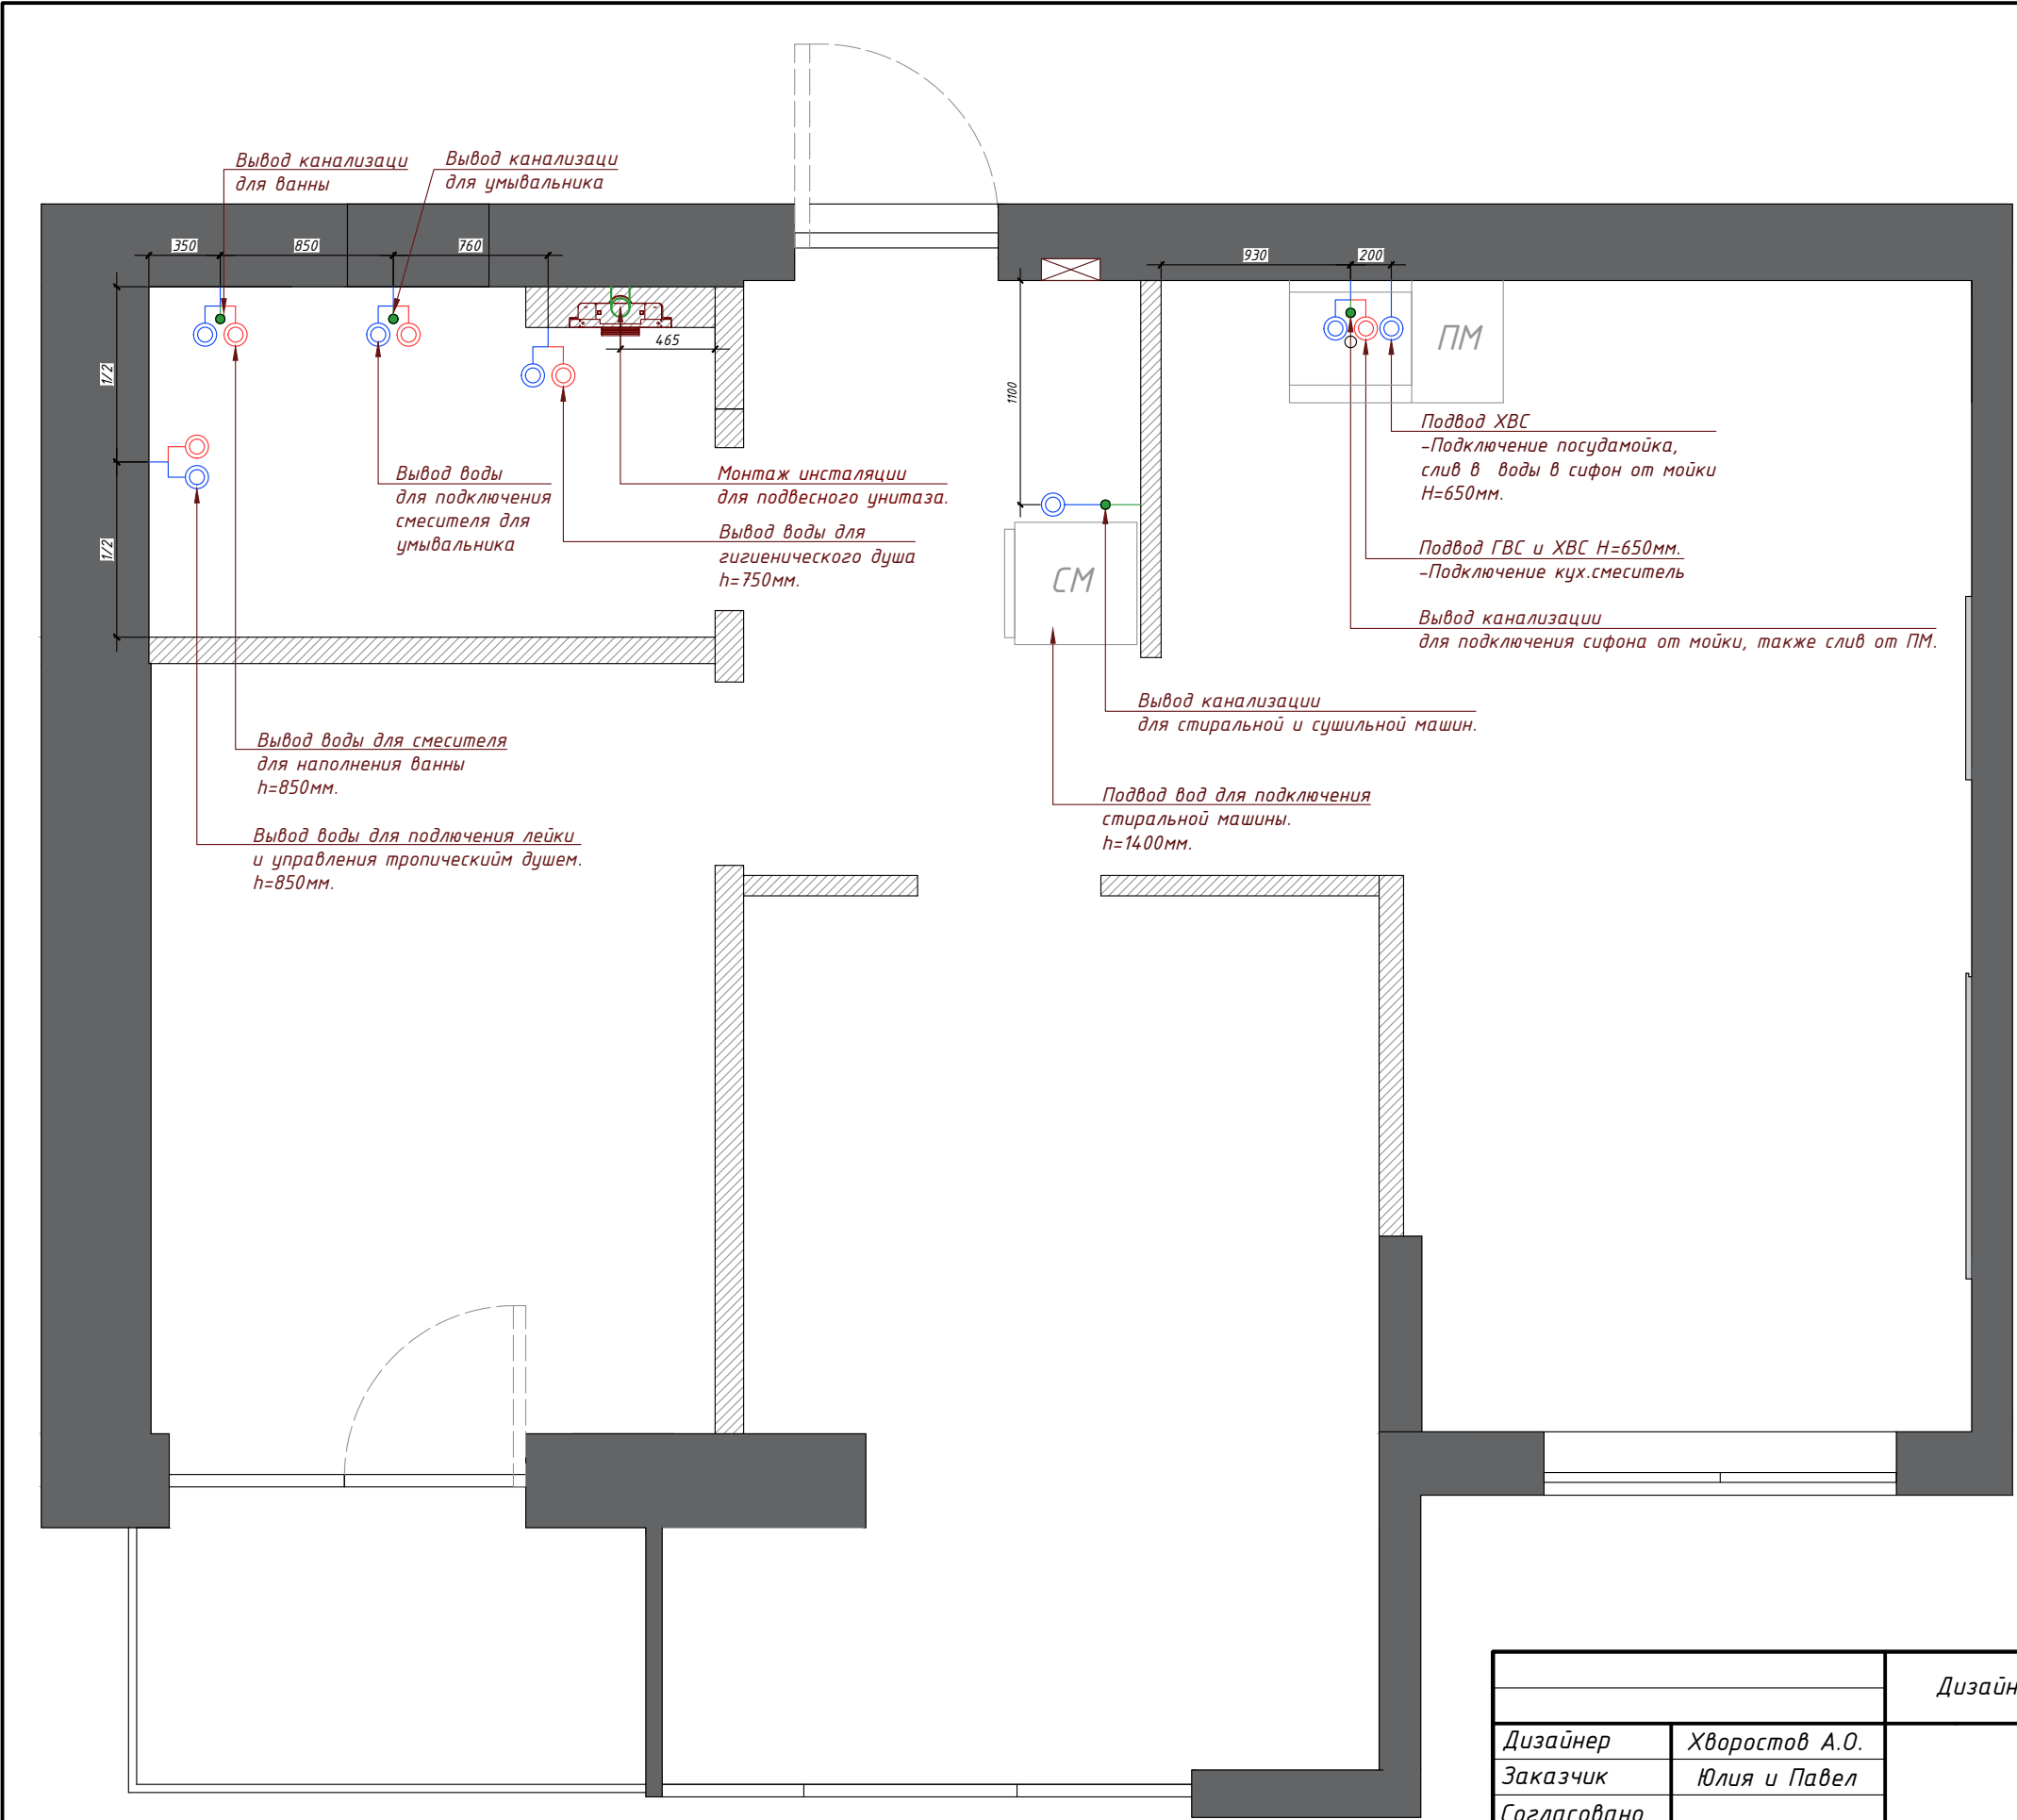

Условные обозначения	
	Точка вывода ГВС и ХВС
	Точка вывода ХВС
	Точка вывода канализации

- Примечание:
- Разметку и штробление стен под водорозетки осуществлять только после окончательного согласования и выбора сантехнических приборов и при наличии их на объекте.
 - Все размеры даны по центру прибора. Все размеры даны по выравнивающему штукатурному слою.
 - Все высоты даны от уровня чистового пола. Выполнить перерасчет высоты от уровня чистовой стяжки по месту исходя из выбранных чистовых напольных покрытий.
 - Допустимая погрешность в размерах 20 мм. При большей погрешности, по факту, скорректировать размеры по месту на усмотрение строительно-монтажной бригады, согласовать изменения с заказчиком или представителем авторского надзора, или лицом его представляющим.
 - Высоту монтажа унитазов уточнить по месту согласно подводу канализационных труб. Рекомендуемая высота монтажа унитаза от у.ч.п. до верха 400-450 мм.
 - Рекомендуемая высота душевых леек 2100-2200 мм или 2300-2400, если не указана иная.
 - В обязательном порядке выполнить звукоизоляцию всех стояков. При прокладке труб ХВС и ГВС выполнить термоизоляцию труб.
 - При необходимости заменить на объекте все коллекторы от застройщика.
 - Подключение и монтаж бойлера согласно рекомендациям специалиста. Подвести к бойлеру: ХВС, ГВС.
 - Специалисту по сантехнике, при проведении работ необходимо консультироваться с специалистом по плитке во избежание нестыковок.
 - При прокладке труб выполнить их подштрабливание в стены, для устройства наращивания стен согласно проектным размерам.
 - Скорректировать все выводы для сантехники по месту согласно выбранной модели и рекомендациям производителя

		Дизайн-проект квартиры по ул. Миля 9	Стадия	Лист	Листов
			РП	8	49
Дизайнер	Хворостов А.О.	План сантехники (1:35)			
Заказчик	Юлия и Павел				
Согласовано					
Дата	31.07.2026				

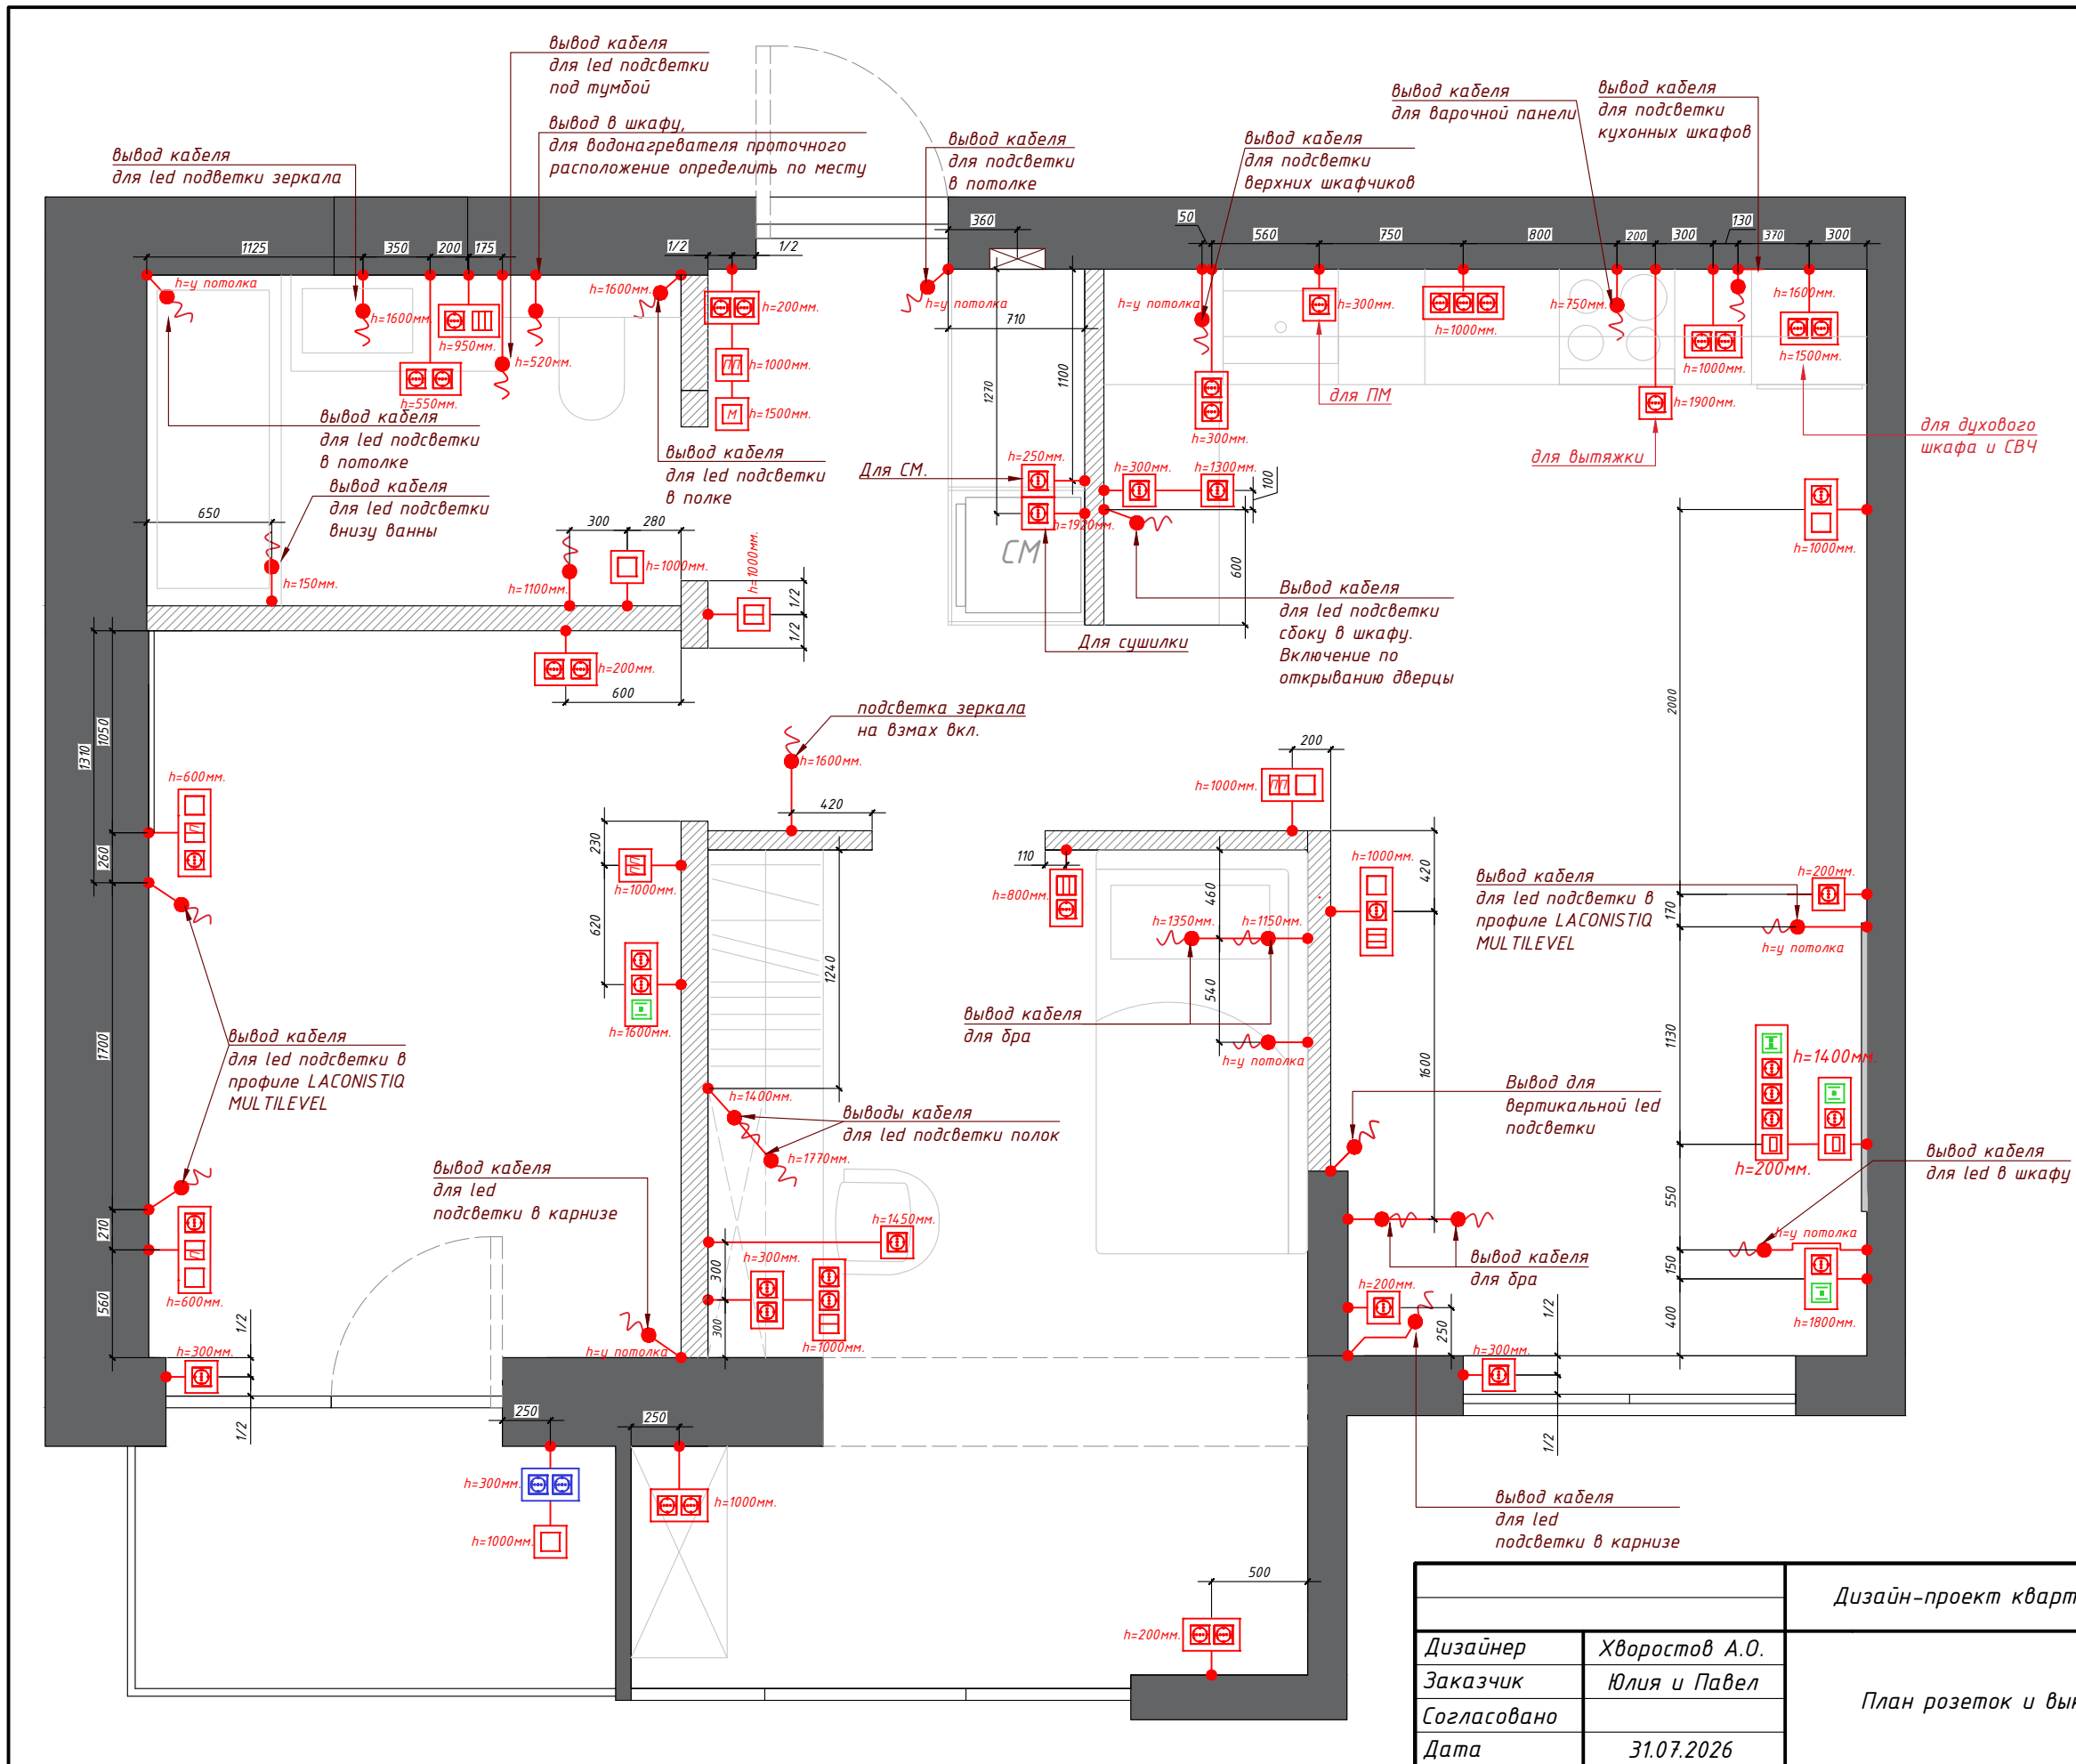


Спецификация розеток и выключателей		
	Розетка 220V.	47 шт.
	Розетка 220V. (ip44)	2 шт.
	Розетка заглушка кабелей	2 шт.
	Розетка RJ45 x 1 (internet)	3 шт.
	Розетка RJ45 x 2 (internet)	1 шт.
	Выключатель одноклавишный	7 шт.
	Выключатель двухклавишный	3 шт.
	Выключатель двухклавишный проходной	2 шт.
	Мастер выключатель	1 шт.
	Вывод эл.кабеля.	28 шт.
	Выключатель двухклавишный проходная одна клавиша.	2 шт.
	Выключатель трёхклавишный	3 шт.

Примечание:
1. Допустимая погрешность в размерах 20 мм. При большей погрешности, по факту, скорректировать размеры по месту на усмотрение строительно-монтажной бригады, согласовать изменения с заказчиком или представителем авторского надзора, или лицом его представляющим.
2. Все размеры привязок выключателей и пультов управления даны по центру прибора.
3. Все высоты привязок выключателей и пультов управления даны от уровня чистового пола. Выполнить перерасчет высоты от уровня чистовой стяжки по месту исходя из выбранных чистовых напольных покрытий.
4. Размещение всех выключателей и пультов скорректировать по месту и согласовать с заказчиком или представителем авторского надзора, или лицом его представляющим.
5. Все размеры даны по выравнивающему штукатурному слою.
6. При прокладке электро-кабелей и устройства точек по электрике в санузле предусмотреть дополнительные меры по изоляции и защите от влаги. Розетки и выключатели устанавливать с влагозащитой

Дизайн-проект квартиры по ул. Миля 9		Стадия	Лист	Листов
		РП	9	49
Дизайнер	Хворостов А.О.	План розеток и выключателей (1:35)		
Заказчик	Юлия и Павел			
Согласовано				
Дата	31.07.2026			



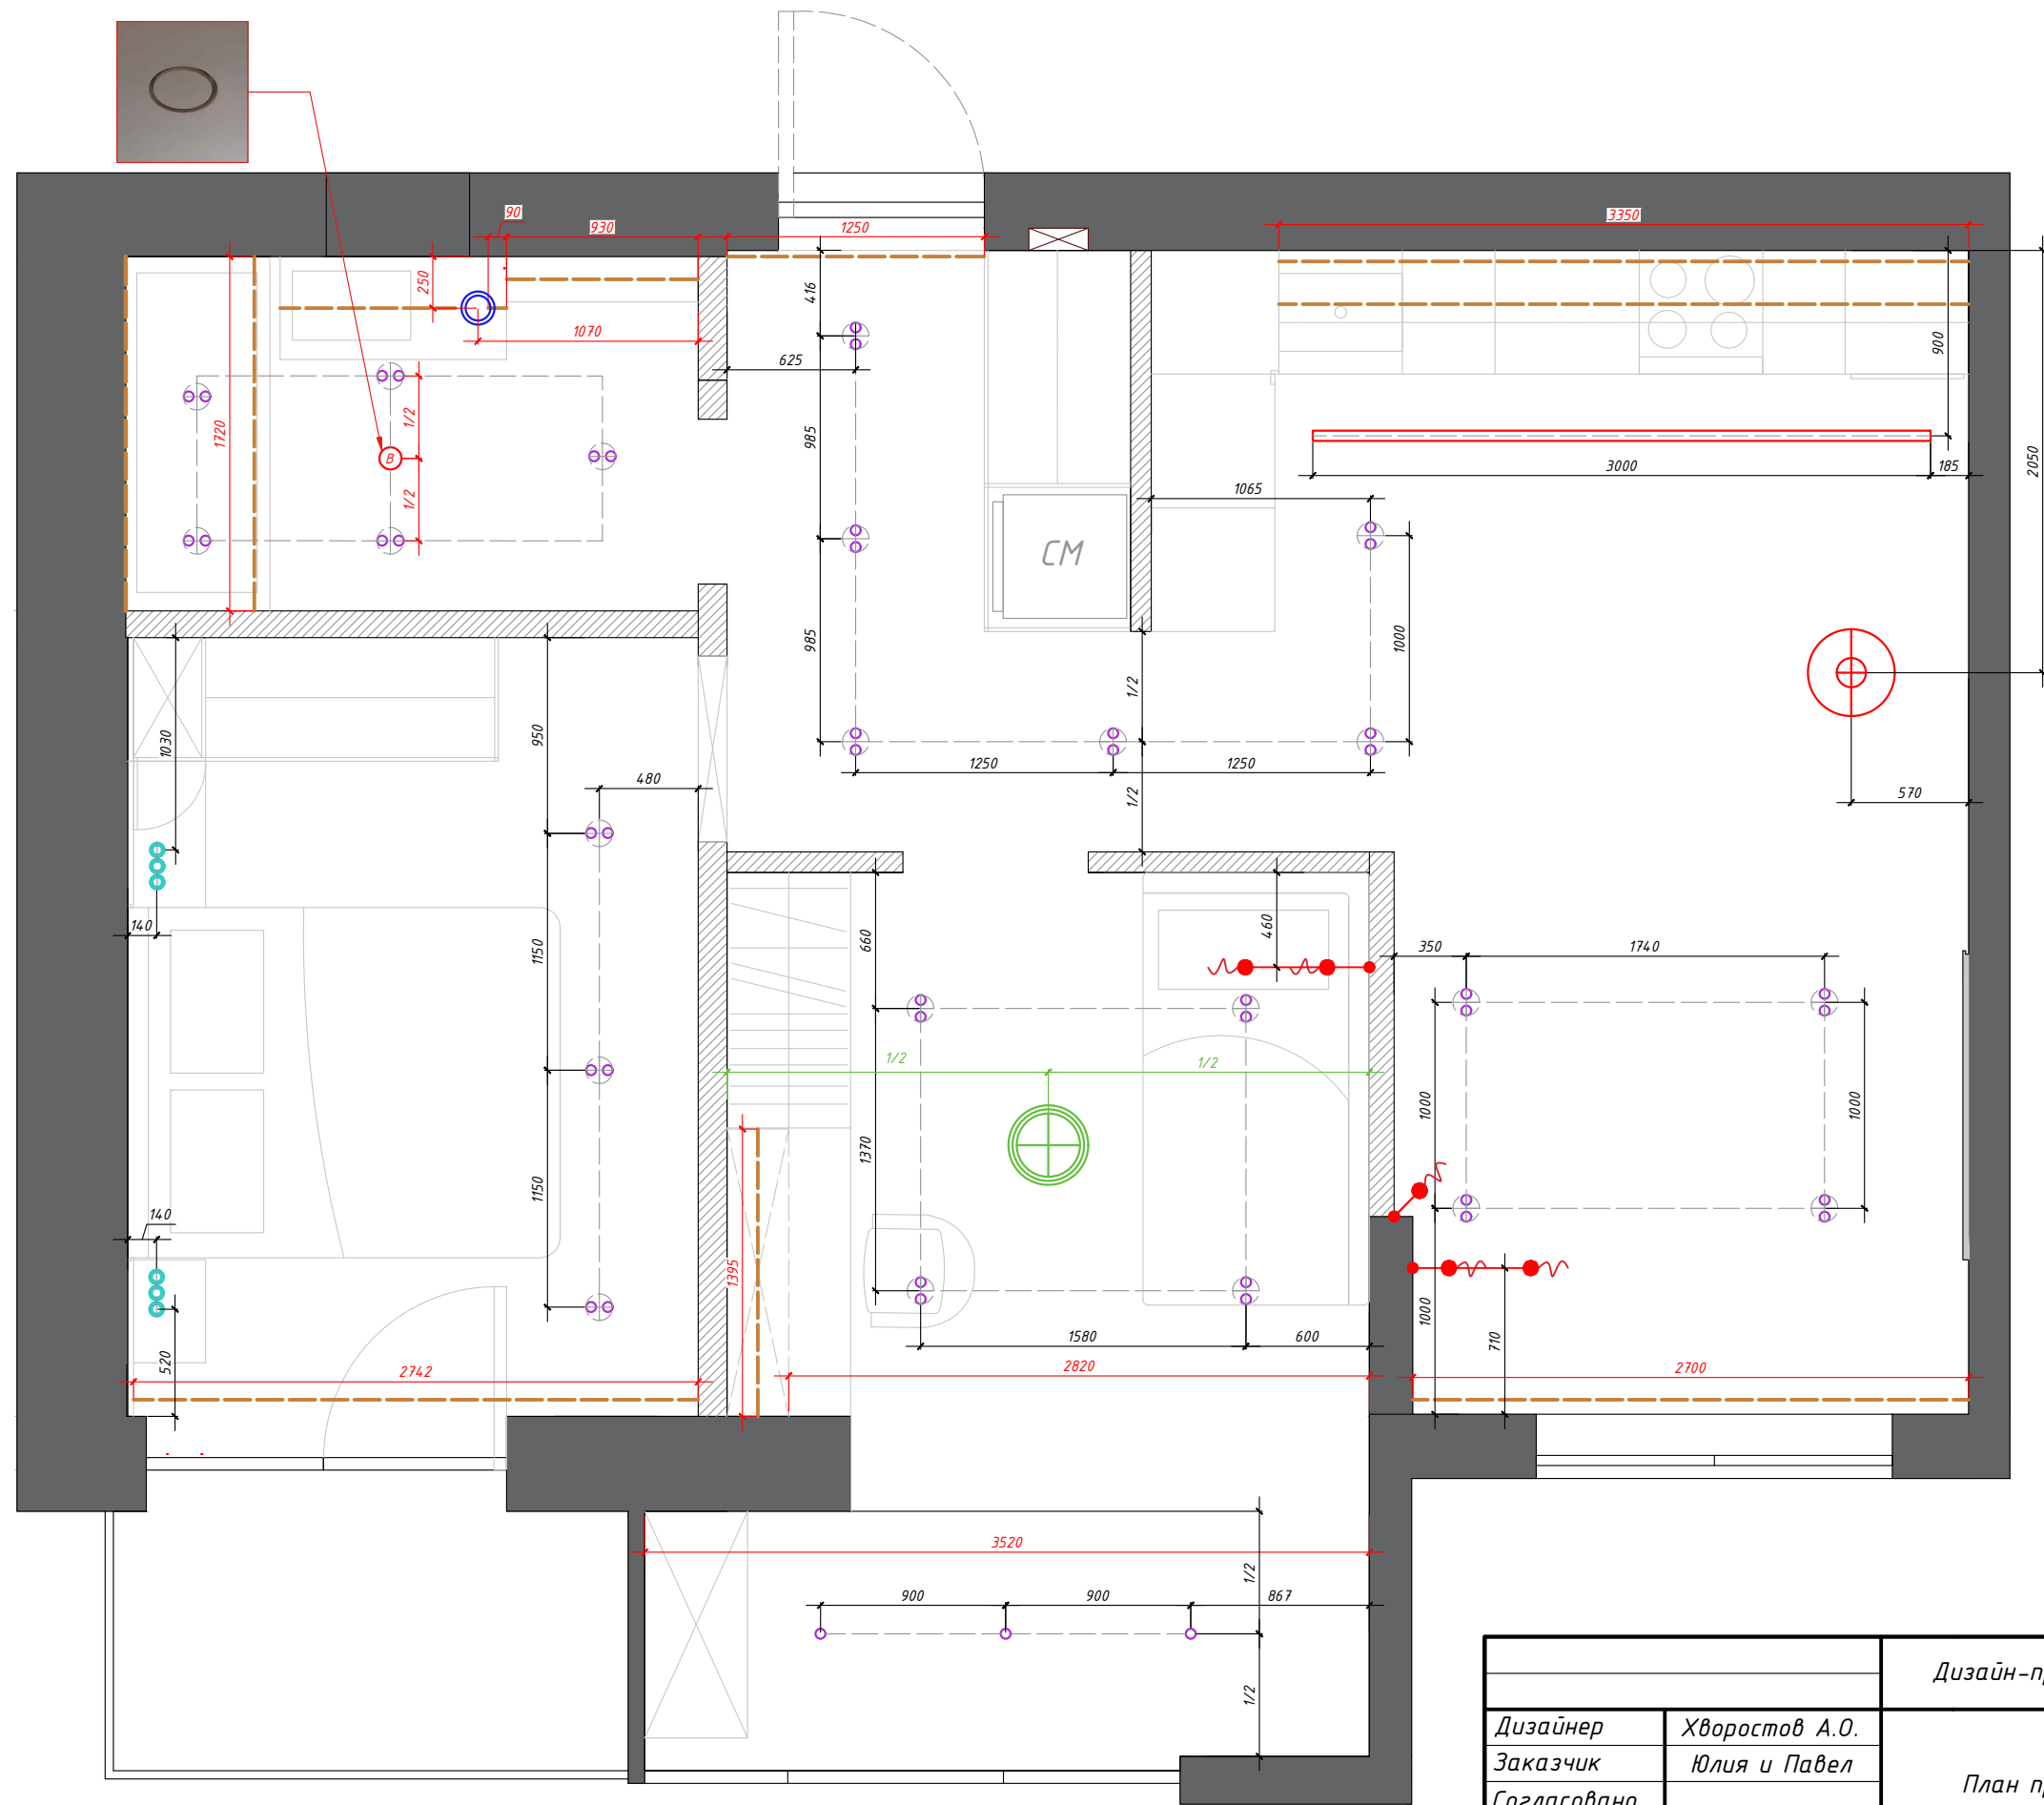


Спецификация светильников			
		Встраиваемый светильник Нео / Нео 1*GU10 9 Вт	44 шт.
		Подвесной дизайнерский светильник Flamingo 1530 by Vibia	1 шт.
		Потолочный светильник	1 шт.
		Кольцевые люстры и светильники CASPIAN два кольца или аналог из Китая.	1 шт.
		Подвесной светильник Cisterna by Romatti 22x37 или аналог в Китае	1 шт.
		Подвесной светильник Jemstone 5084/5L	6 шт.
		Вент. решетка скрытая для натяжного потолка	1 шт.
		Flexy TREK 08	3 м.
		Светильник LIGHT 201 он идет в шинпровод	4 шт.

Примечание:

- Допустимая погрешность в размерах 20 мм. При большей погрешности, по факту, скорректировать размеры по месту на усмотрение строительно-монтажной бригады, согласовать изменения с заказчиком или представителем авторского надзора, или лицом его представляющим.
- Все размеры привязок выключателей и пультов управления даны по центру прибора.
- Все высоты привязок выключателей и пультов управления даны от уровня чистового пола. Выполнить перерасчет высоты от уровня чистовой стяжки по месту исходя из выбранных чистовых напольных покрытий.
- Размещение всех выключателей и пультов скорректировать по месту и согласовать с заказчиком или представителем авторского надзора, или лицом его представляющим.
- Все размеры даны по выравнивающему штукатурному слою.
- При прокладке электро-кабелей и устройства точек по электрике в санузле предусмотреть дополнительные меры по изоляции и защите от влаги. Розетки и выключатели устанавливать с влагозащитой

		Дизайн-проект квартиры по ул. Миля 9	Стадия	Лист	Листов
			РП	10	49
Дизайнер	Хворостов А.О.	План привязки светильников (1:35)			
Заказчик	Юлия и Павел				
Согласовано					
Дата	31.07.2026				

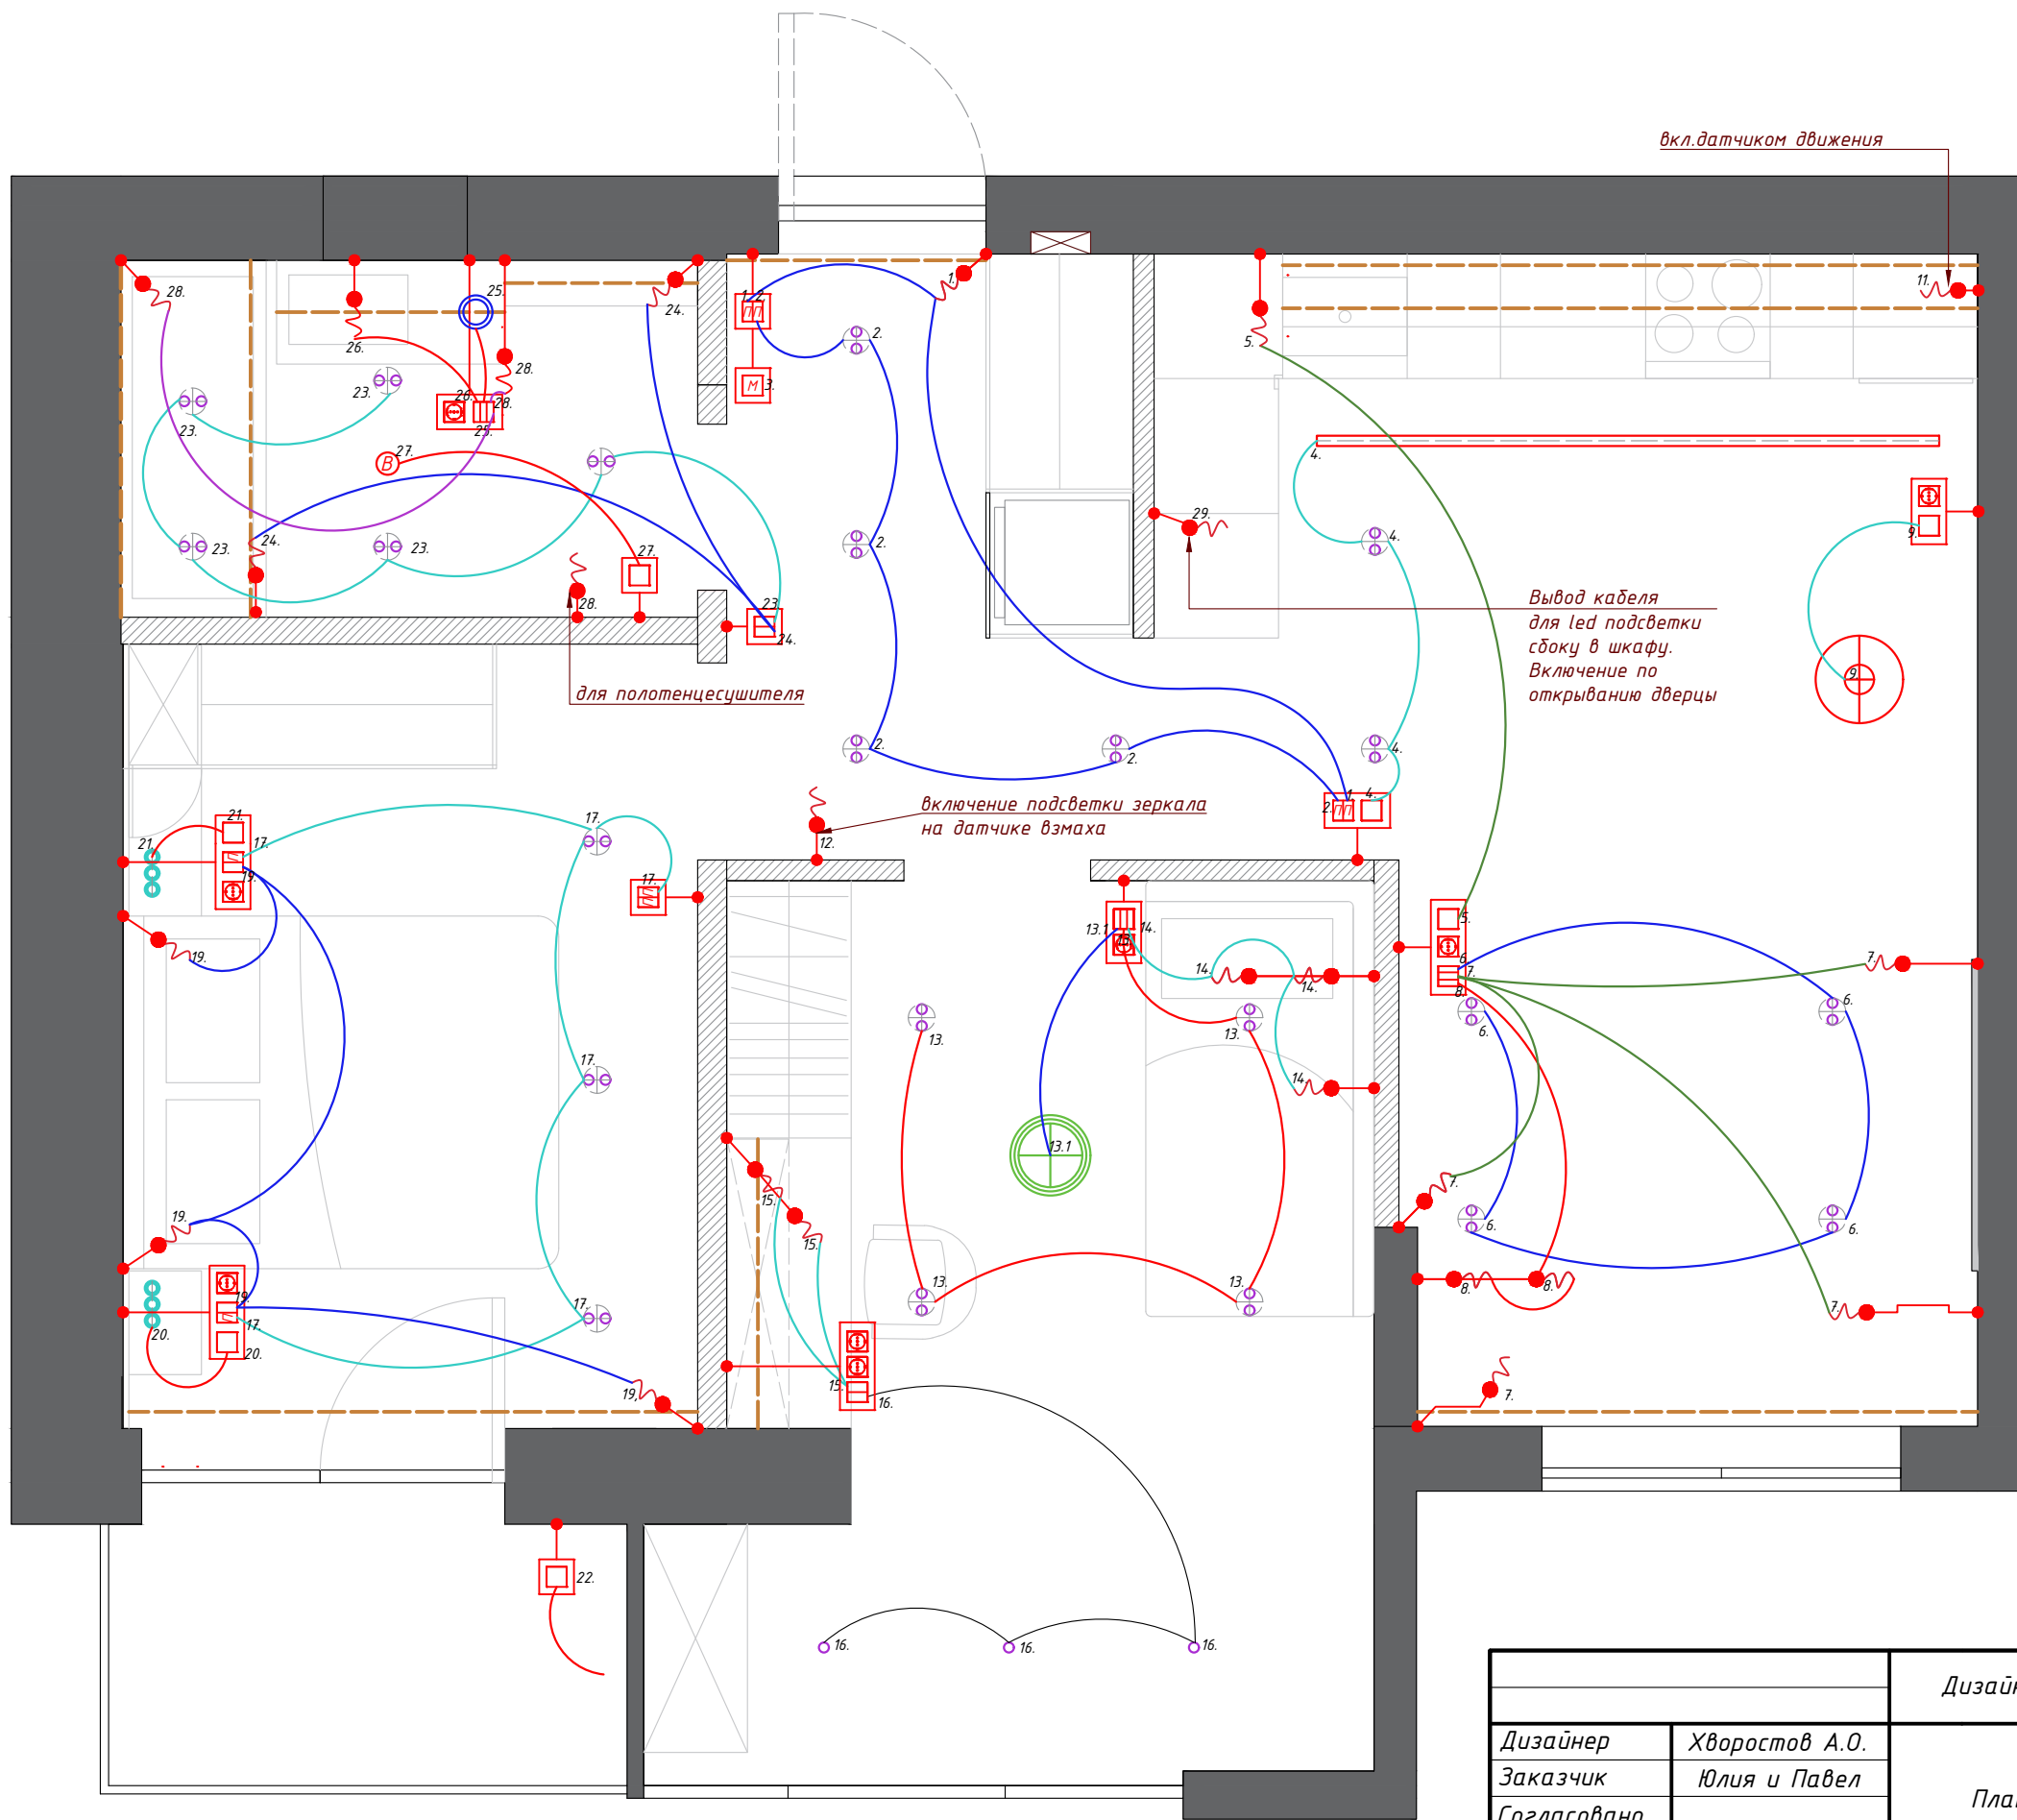


Спецификация светильников			
		Встраиваемый светильник Neo / Neo 1*GU10 9 Вт	44 шт.
		Подвесной дизайнерский светильник Flamingo 1530 by Vibia	1 шт.
		Потолочный светильник	1 шт.
		Подвесной светильник Cisterna by Romatti 22x37 или аналог в Китае	1 шт.
		Подвесной светильник Froght Артикул: PDL2248-2	6 шт.
		Вент. решетка скрытая для натяжного потолка	1 шт.
		Flexy TREK 08	3 м.
		Светильник LIGHT 201 он идет в шинный провод	4 шт.

Примечание:

- Допустимая погрешность в размерах 20 мм. При большей погрешности, по факту, скорректировать размеры по месту на усмотрение строительно-монтажной бригады, согласовать изменения с заказчиком или представителем авторского надзора, или лицом его представляющим.
- Все размеры привязок выключателей и пультов управления даны по центру прибора.
- Все высоты привязок выключателей и пультов управления даны от уровня чистового пола. Выполнить перерасчет высоты от уровня чистовой стяжки по месту исходя из выбранных чистовых напольных покрытий.
- Размещение всех выключателей и пультов скорректировать по месту и согласовать с заказчиком или представителем авторского надзора, или лицом его представляющим.
- Все размеры даны по выравнивающему штукатурному слою.
- При прокладке электро-кабелей и устройства точек по электрике в санузле предусмотреть дополнительные меры по изоляции и защите от влаги. Розетки и выключатели устанавливать с влагозащитой

Дизайн-проект квартиры по ул. Миля 9		Стадия	Лист	Листов
		РП	11	49
Дизайнер	Хворостов А.О.	План включения светильников (1:35)		
Заказчик	Юлия и Павел			
Согласовано				
Дата	31.07.2026			




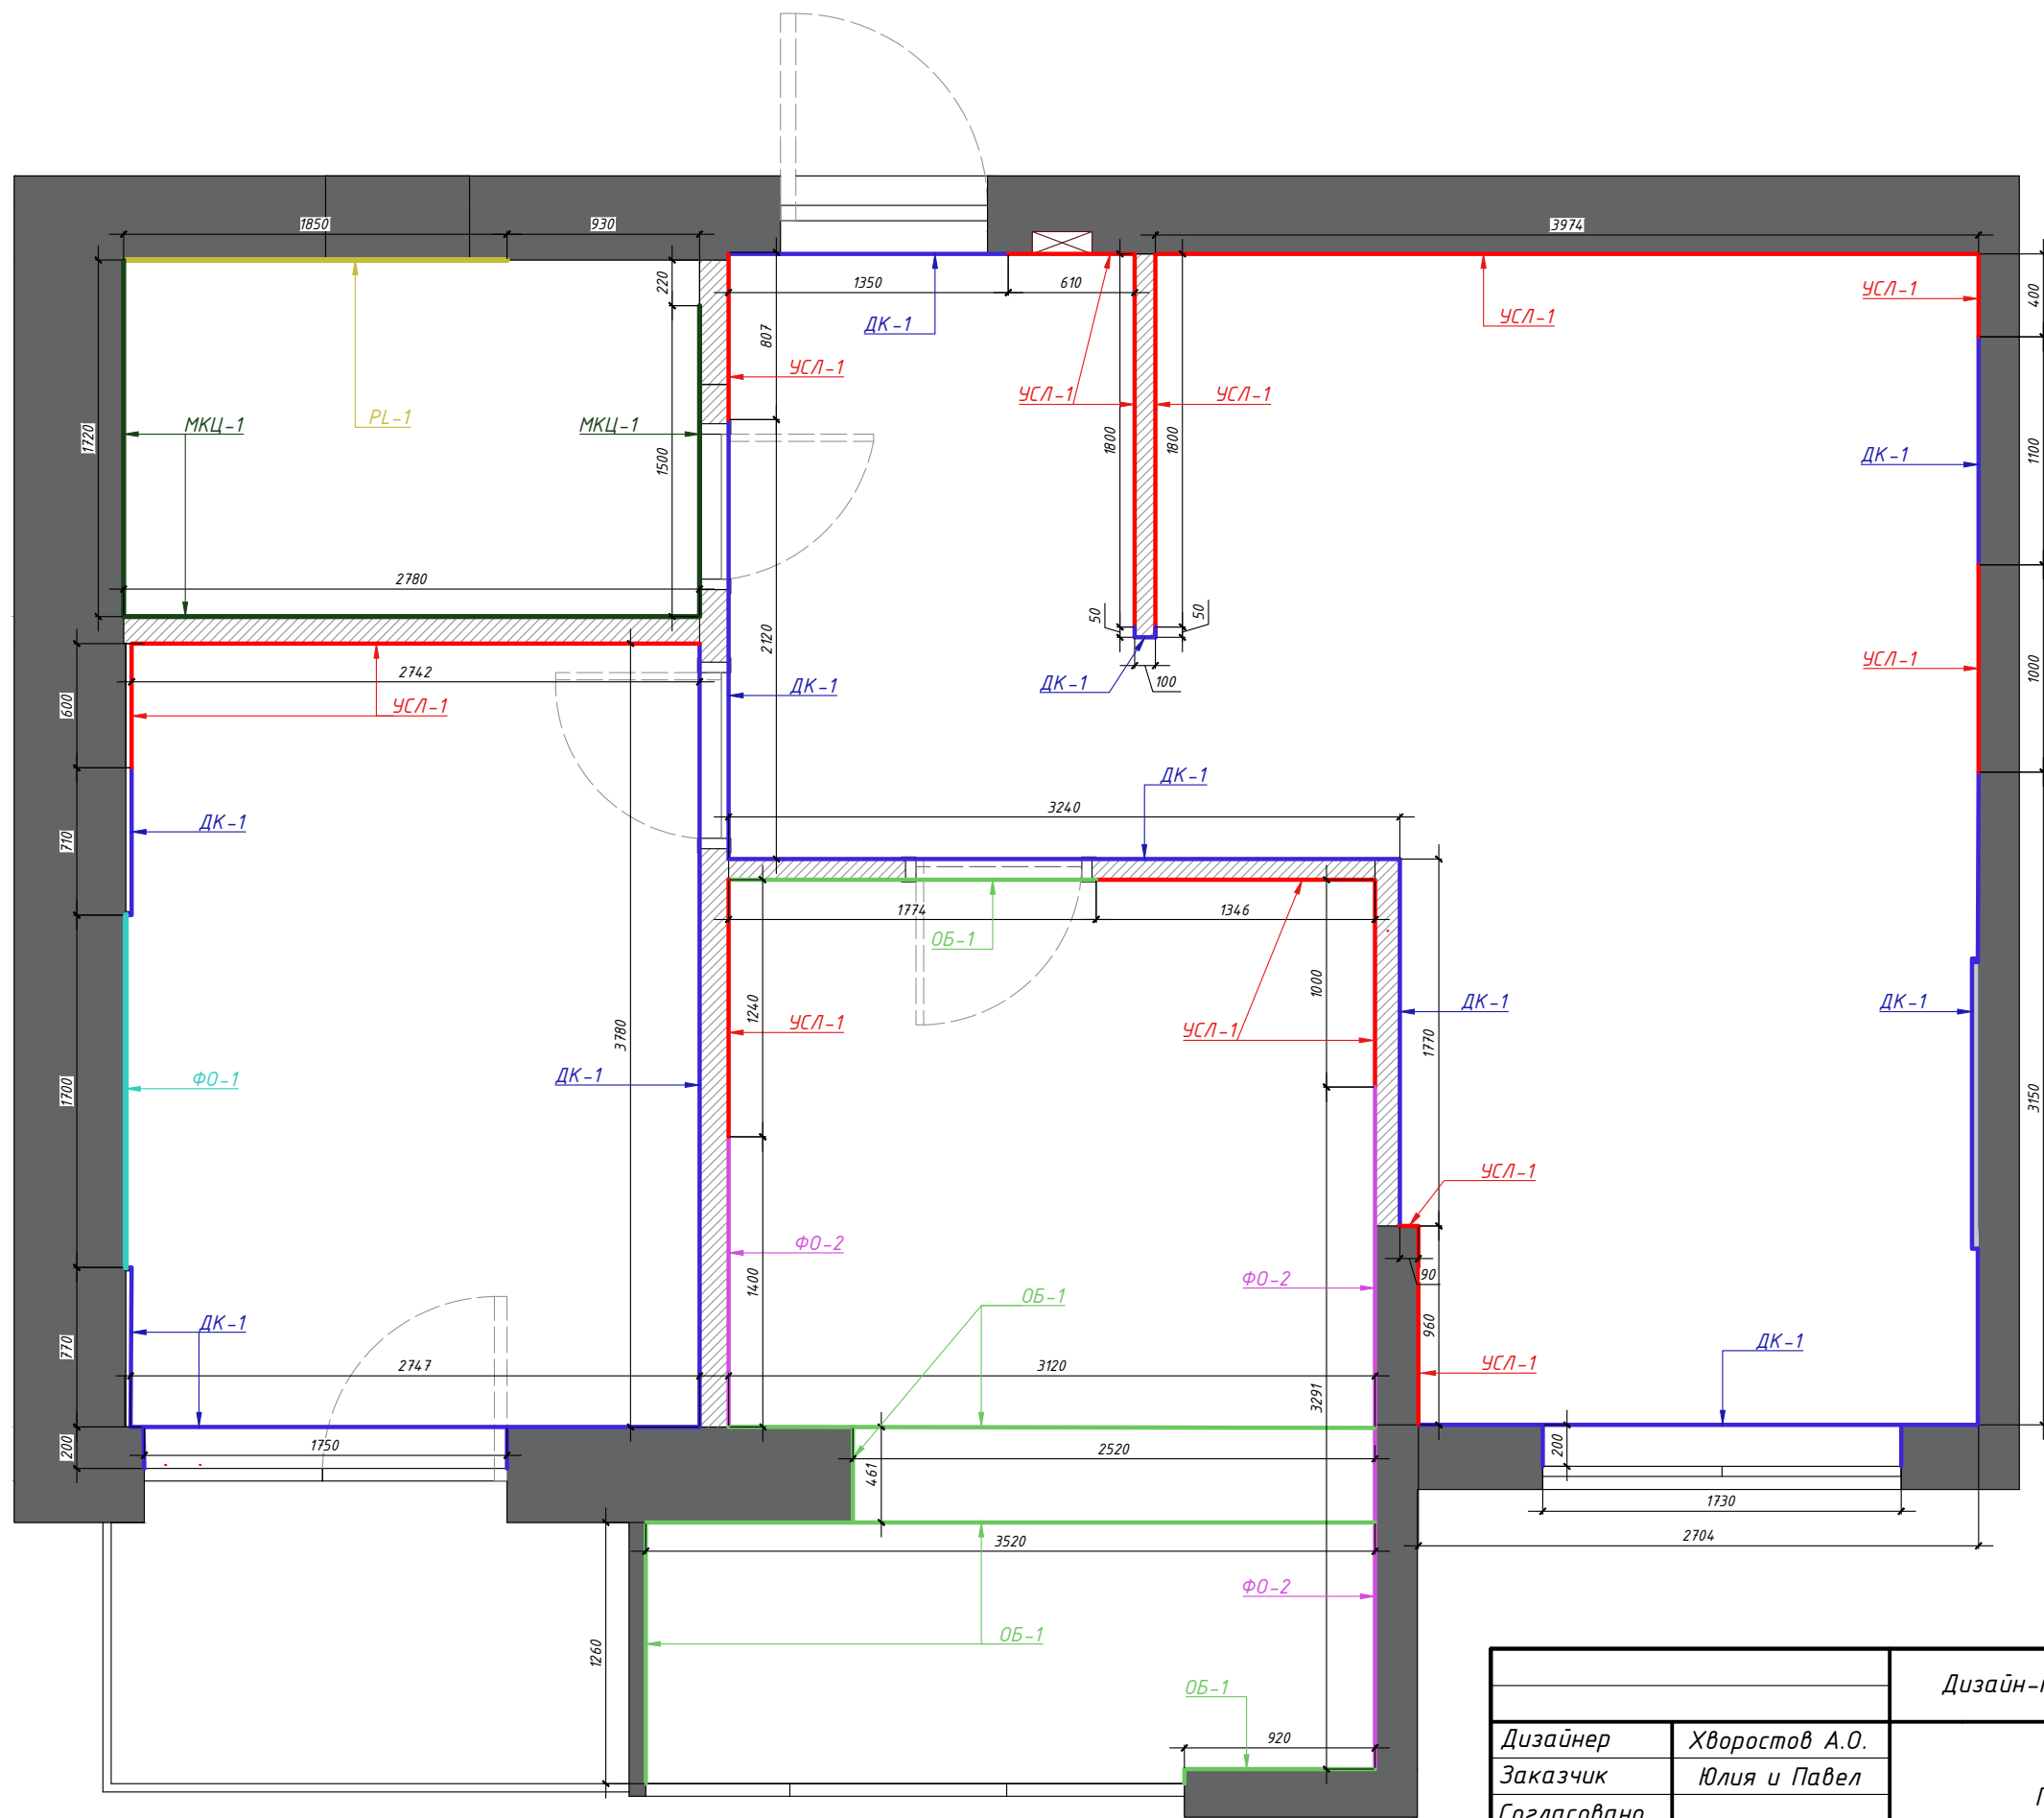

Условные обозначения		
<u>УСЛ-1</u>	Условная покраска (MAV) Краска ВД FLAGMAN 35 кухня и в анная белая шелковисто-матовая 11 л	50 м ²
<u>ДК-1</u>	Штукатурка декоративная Marmorino Naturale Fine B.CO/P Кухня-гостиная (RAL 9001 — Cream) = 50 м.кв. Коридор (NCS S 1002-R) = 11 м.кв.	61 м ²
<u>ОБ-1</u>	Обои Grandeco Keen KE1006 https://minskoboi.by/product/oboi-grandeco-keen-ke1006/	23.50 м ² (3-4 трубки)
<u>ФО-2</u>	Оникс Артикул: 1-148 (Vinni.by) Или аналог фотопечать : https://signex.by/shirokoformatnaya-pechat/fotooboi	12.80 м ²
<u>ФО-1</u>	Артикул: 5-103 (5-102 color 1) Или аналог фотопечать : https://signex.by/shirokoformatnaya-pechat/fotooboi	4.65 м ²
<u>PL-1</u>	Tribeca Sage Green 6x24.6	6 м ²
<u>МКЦ-1</u>	Микроцемент	18 м ²

- Примечание:
- Допустимая погрешность в размерах 20 мм. При большей погрешности, по факту, скорректировать размеры по месту на усмотрение строительно-монтажной бригады, согласовать изменения с заказчиком или представителем авторского надзора, или лицом его представляющим.
 - Все размеры указаны с учетом чистовой отделки стен.
 - Все объемы по материалам посчитаны без учета запаса, для определения общего количества материалов, просчетов сметной стоимости и определения общего объема работ. Выполнить перерасчет со специалистом по месту.
 - Перед проведением отделочных работ выполнить цветовые выкраски, согласовать все цвета с заказчиком или представителем авторского надзора, или лицом его представляющим.
 - Цвет отделочных материалов может быть скорректирован заказчиком самостоятельно
 - Все объемы по отделке посчитаны с учетом отделки стен, откосов, дверей невидимок и без учёта других элементов
 - В местах стыка упрощенной и чистовой отделки за мебелью выполнить завод чистовой отделки на 100 мм на упрощенную. Видимые углы плитки выполнить с запилот под 45°.
 - Откосы исполнить в цвет стен, где обои то белая краска

		Дизайн-проект квартиры по ул. Миля 9	Стадия	Лист	Листов
			РП	12	49
Дизайнер	Хворостов А.О.	План отделки стен (1:35)			
Заказчик	Юлия и Павел				
Согласовано					
Дата	31.07.2026				


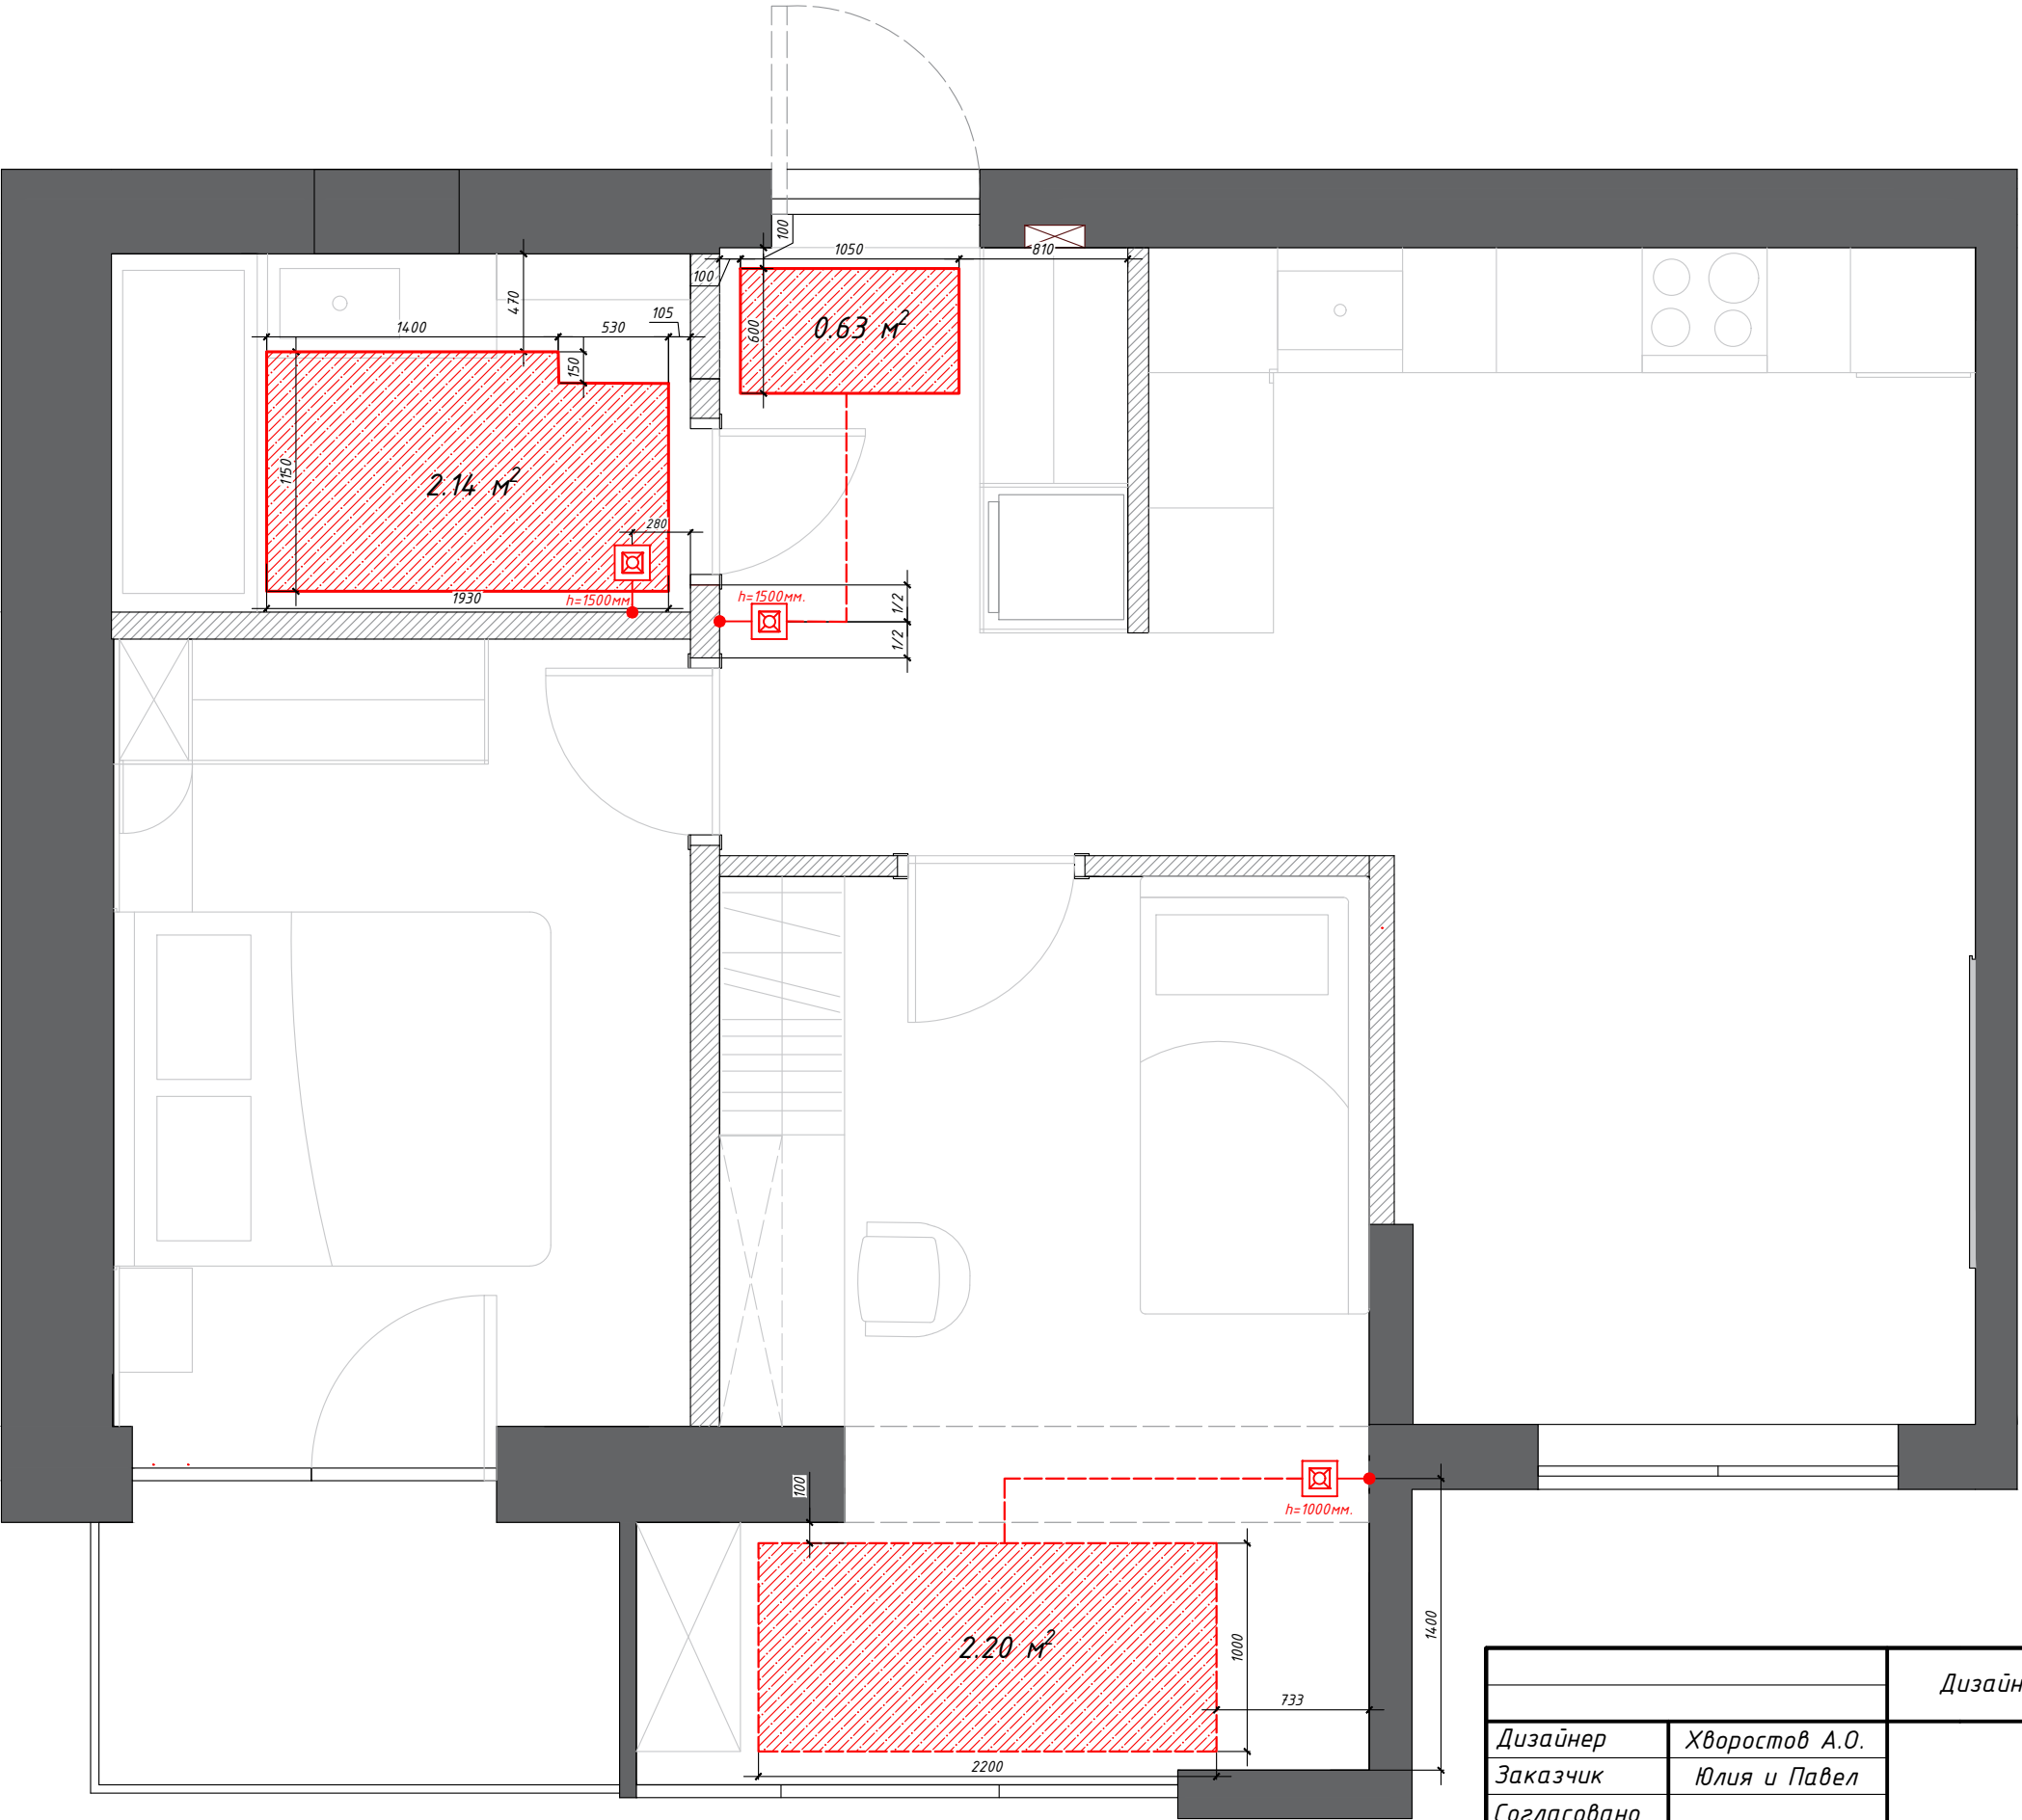


Условные обозначения		
	Нагревательный кабель Nexans	5 м²
	Регулятор тёплого пола	3 шт.

Примечание:

- Допустимая погрешность в размерах 20 мм. При большей погрешности, по факту, скорректировать все размеры по месту на усмотрение строительно-монтажной бригады, согласовать изменения с заказчиком или представителем авторского надзора, или лицом его представляющим.
- В указанных зонах выполнить электрический теплый пол.
- Монтаж теплого пола осуществлять согласно рекомендациям производителя.
- При закупки теплого пола учесть длину кабеля для терморегулятора. Высоты терморегуляторов 900-1600 от у.ч.п.
- Все объемы по материалам посчитаны без учета запаса. Для определения общего количества материалов, просчетов сметной стоимости и определения общего объема работ обязателен перерасчет со специалистом по месту.
- Все размеры даны по выравнивающему штукатурному слою.
- Проект системы отопления, теплотехнический расчет, подбор отопительного оборудования выполнить профильным специалистом. Монтаж новых радиаторов осуществлять только после разработки и согласования необходимых разделов проектной документации
- Устройство теплого пола на лоджии незаконно, заказчик предупрежден. Студия не несёт ответственности за данное решение.

		Дизайн-проект квартиры по ул. Миля 9	Стадия	Лист	Листов
			РП	13	49
Дизайнер	Хворостов А.О.	План тёплых полов (1:35)			
Заказчик	Юлия и Павел				
Согласовано					
Дата	31.07.2026				

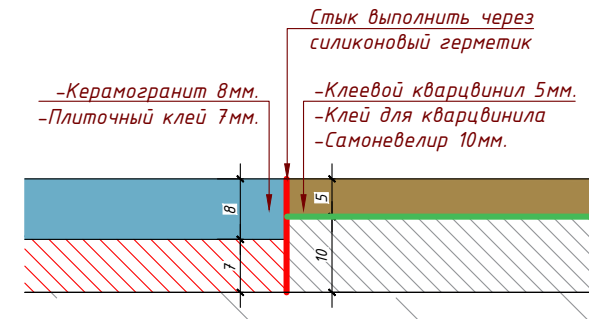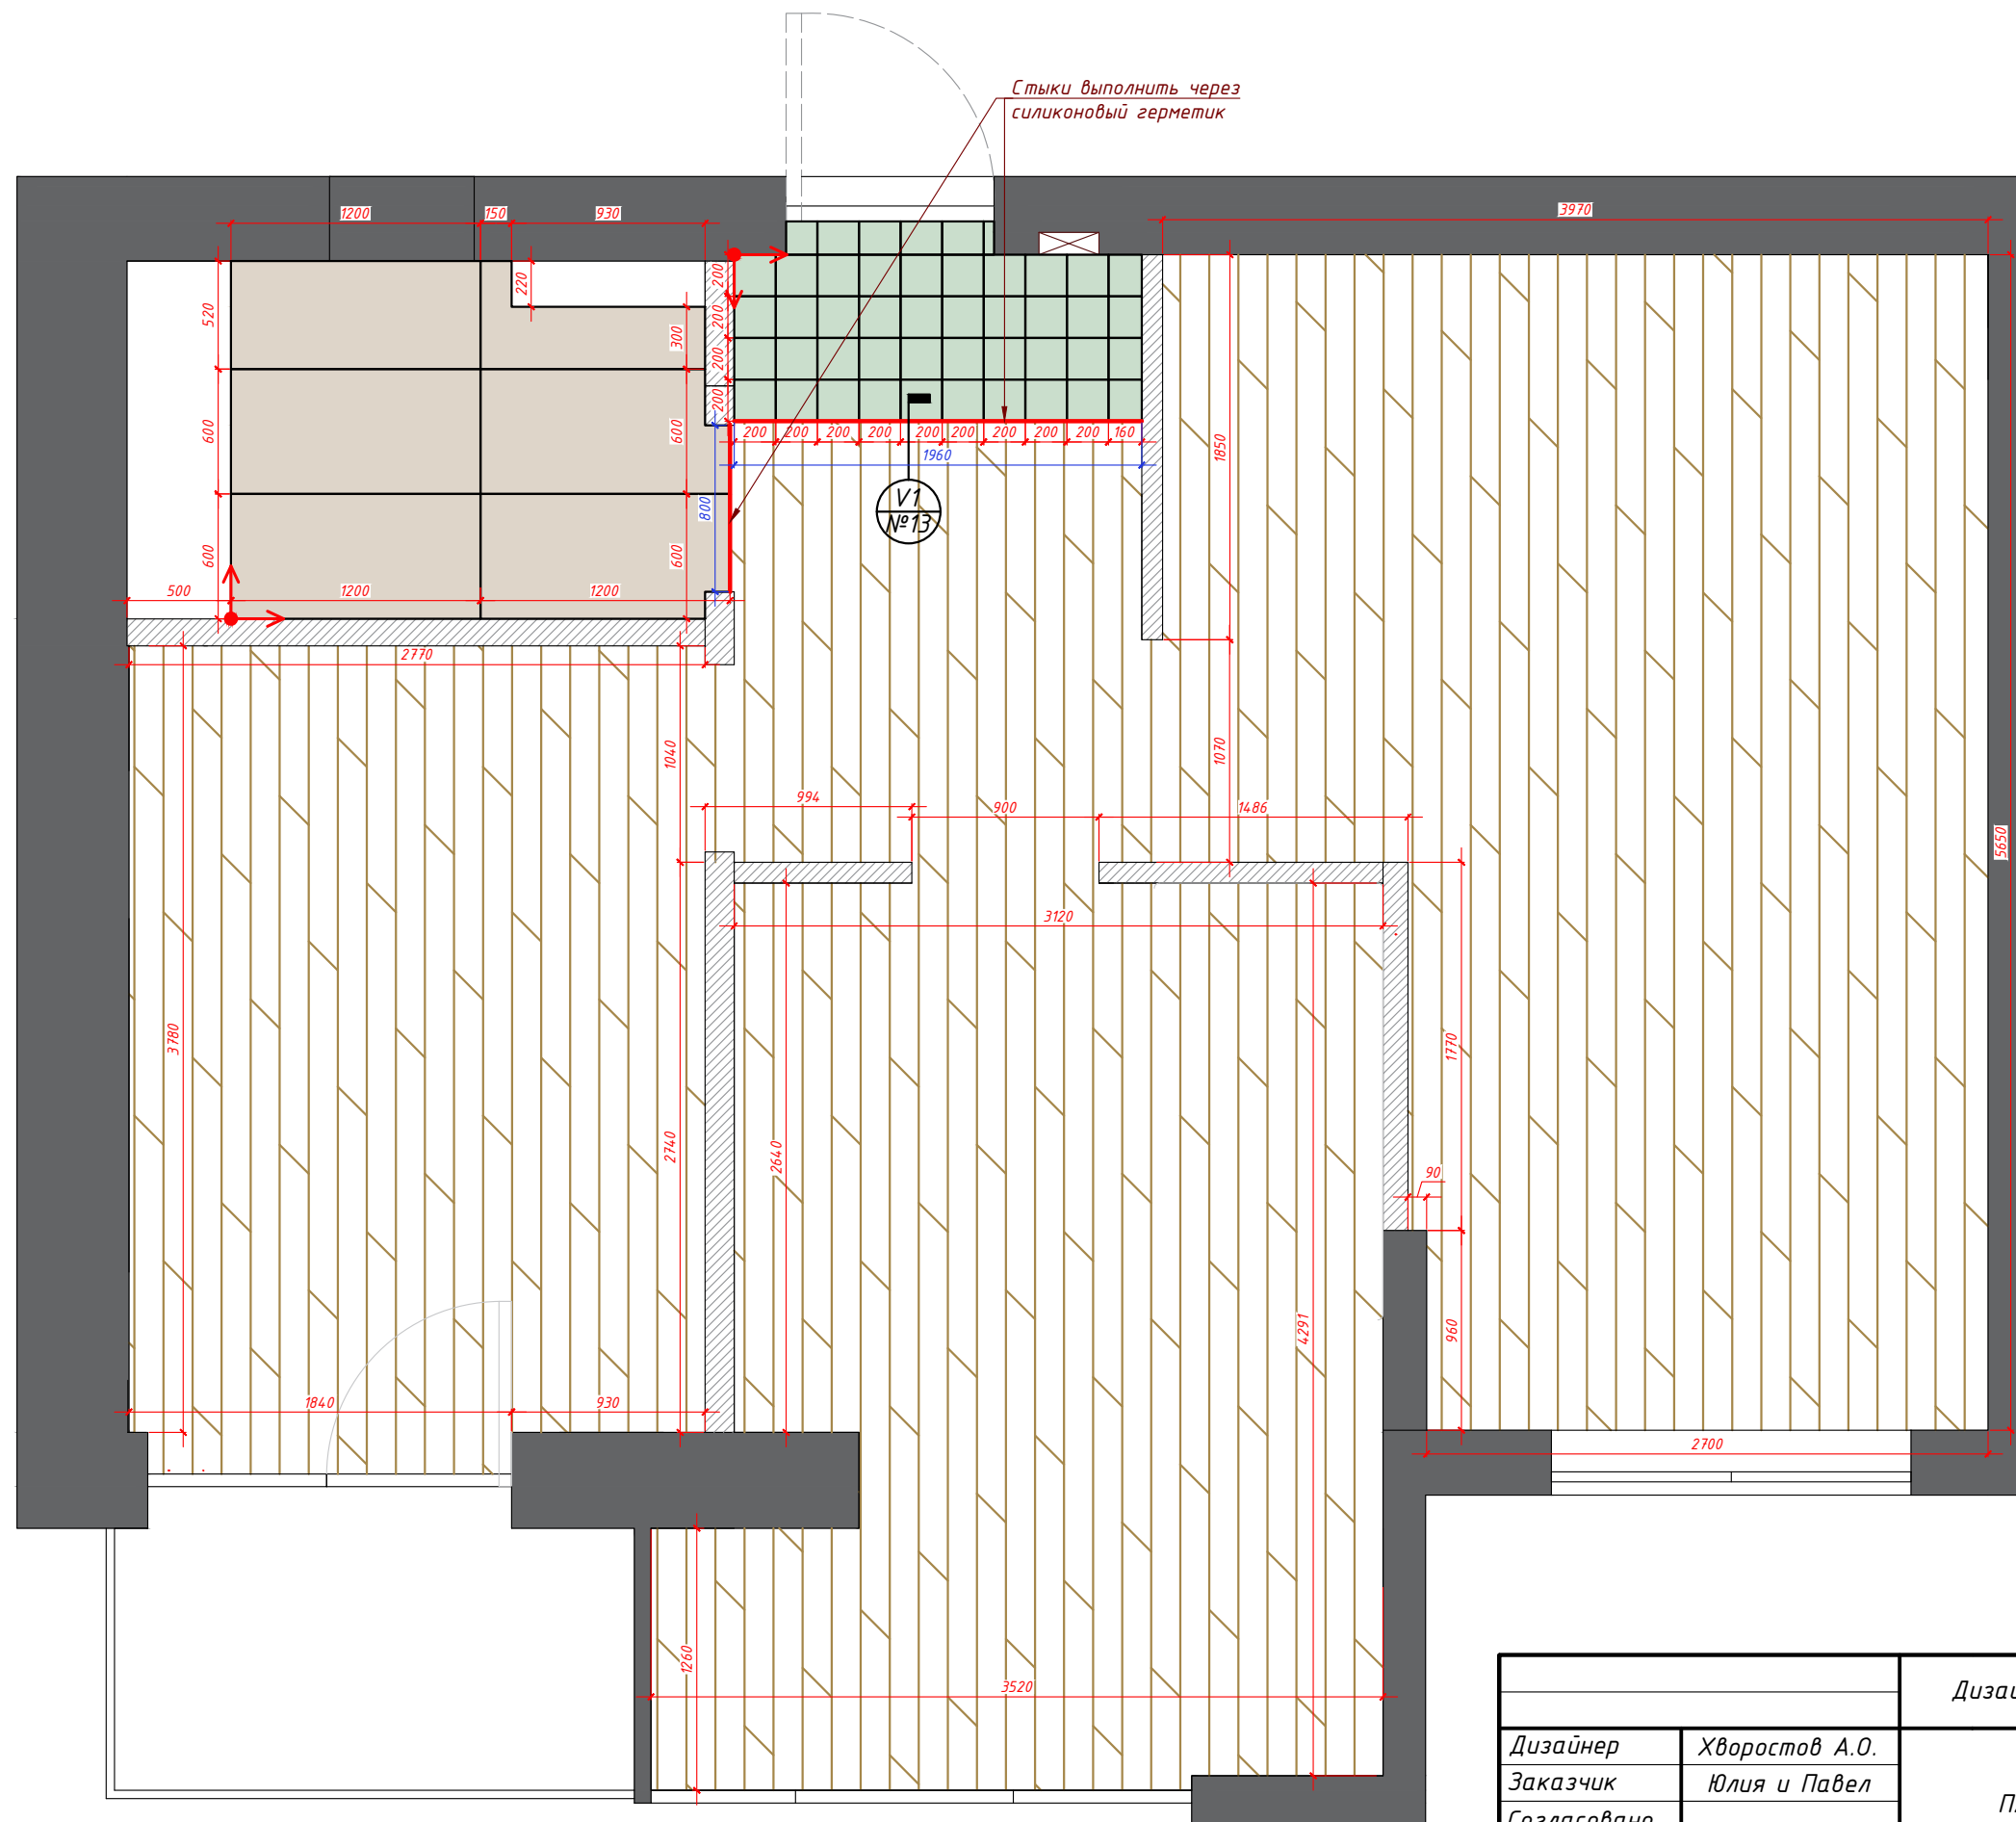

V1


Условные обозначения

- Вино Quick-Step Pristine -SGHBC20331 Дуб безъятежный натуральный светлыйог (49 м²)
- Ponza Lilly (200x200x8) Матовая (50 шт.)
- Argenta Westone Cream MAT 120x60 см (6шт.)

Примечание:


- Допустимая погрешность в размерах 20 мм. При большей погрешности, по факту, скорректировать размеры по месту на усмотрение строительно-монтажной бригады, согласовать изменения с заказчиком или представителем авторского надзора, или лицом его представляющим.
- Напольные покрытия могут быть скорректированы согласно пожеланиям дизайнера или заказчика.
- Монтаж напольных покрытий осуществлять только после прокладки всех инженерных коммуникаций.
- Все объемы по материалам посчитаны без учета запаса. Для определения общего количества материалов, просчетов сметной стоимости и определения общего объема работ обязательен перерасчет со специалистом по месту.
- Монтаж напольных покрытий осуществлять согласно рекомендациям производителя.
- Все напольные покрытия показаны условно. Раскладку напольных покрытий запросить в салоне и скорректировать по месту.
- При необходимости выровнять существующий пол самовыравнивающимися смесями (наливной бетонный выравнивающий слой).
- Стык напольных покрытий осуществлять через пробковый или латунный порожек. Стык напольных покрытий под дверьми осуществлять на расстоянии 20 мм от начала дверного полотна (под дверным полотном)
- Все размеры даны с учетом чистовой отделки стен.

		Дизайн-проект квартиры по ул. Миля 9	Стадия	Лист	Листов
			РП	14	49
Дизайнер	Хворостов А.О.	План напольных покрытий (1:35)			
Заказчик	Юлия и Павел				
Согласовано					
Дата	31.07.2026				

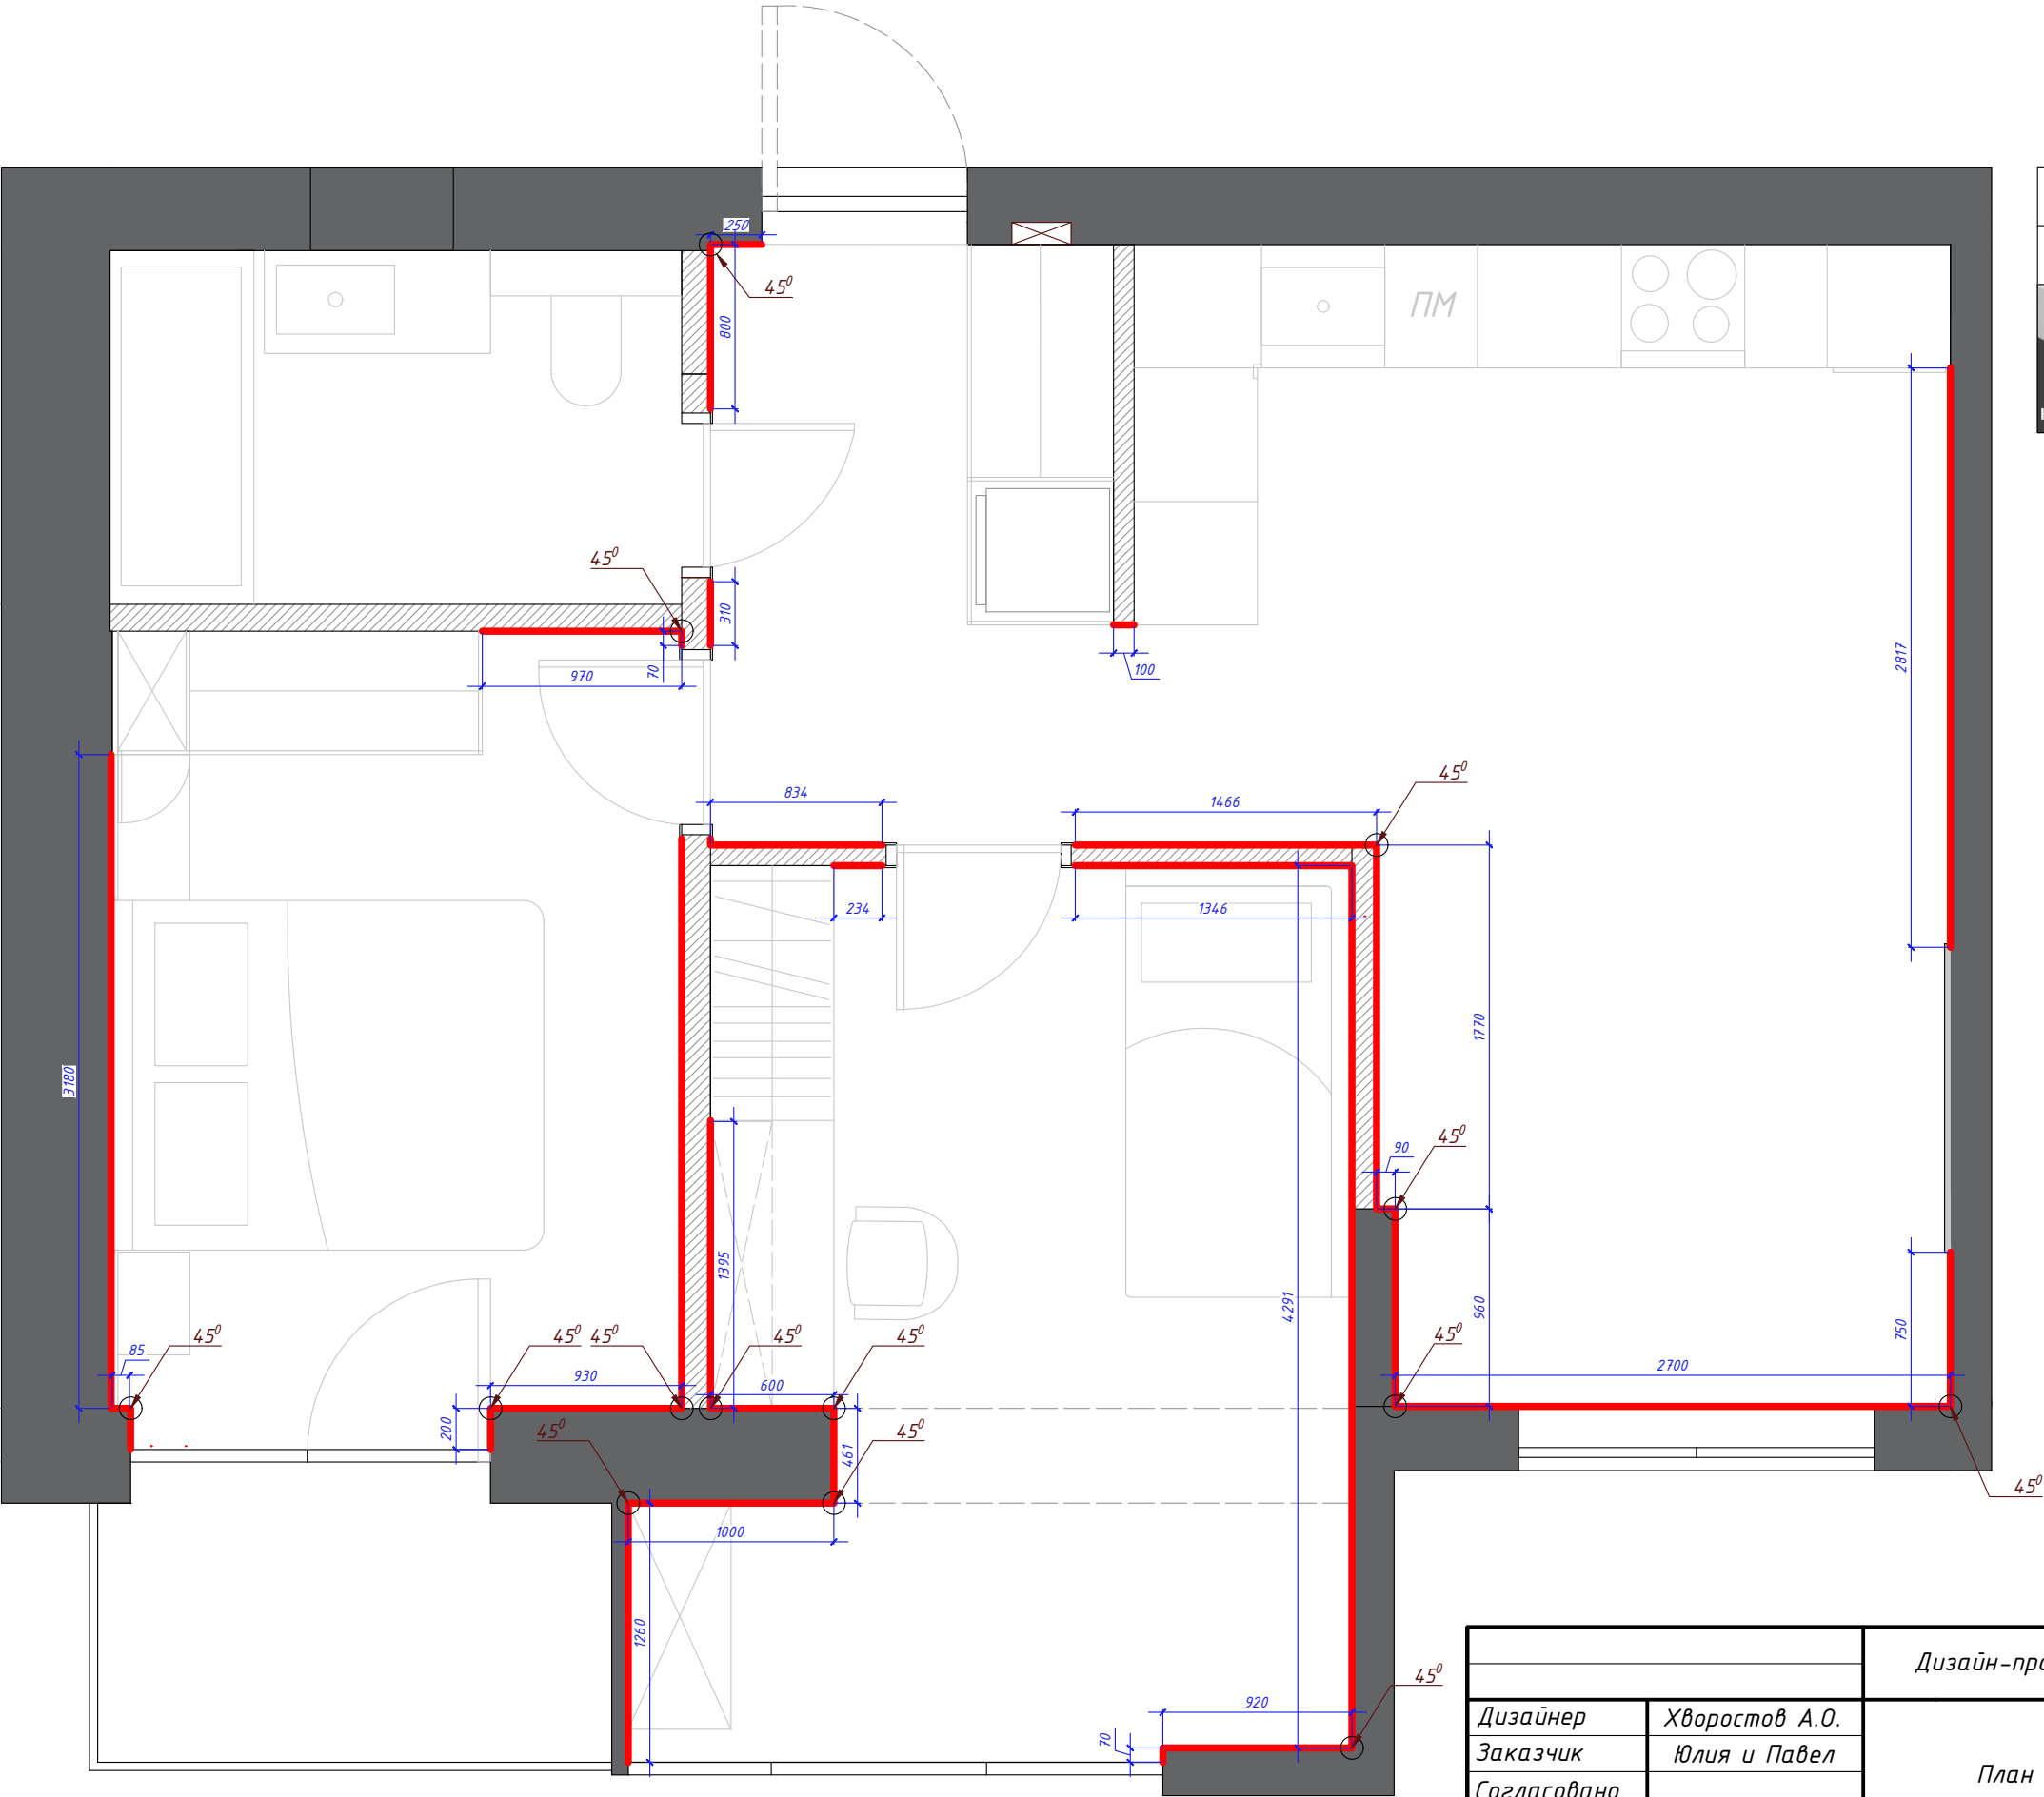


Спецификация напольных плинтусов			
Изобр.	Наименование	Обозначение	Кол-во
	Плинтус напольный МДФ ОНЗ НМ-1540. 2070 м.		17 шт.

		Дизайн-проект квартиры по ул. Миля 9	Стадия	Лист	Листов
			РП	16	49
Дизайнер	Хворостов А.О.	План напольных плинтусов (1:35)			
Заказчик	Юлия и Павел				
Согласовано					
Дата	31.07.2026				

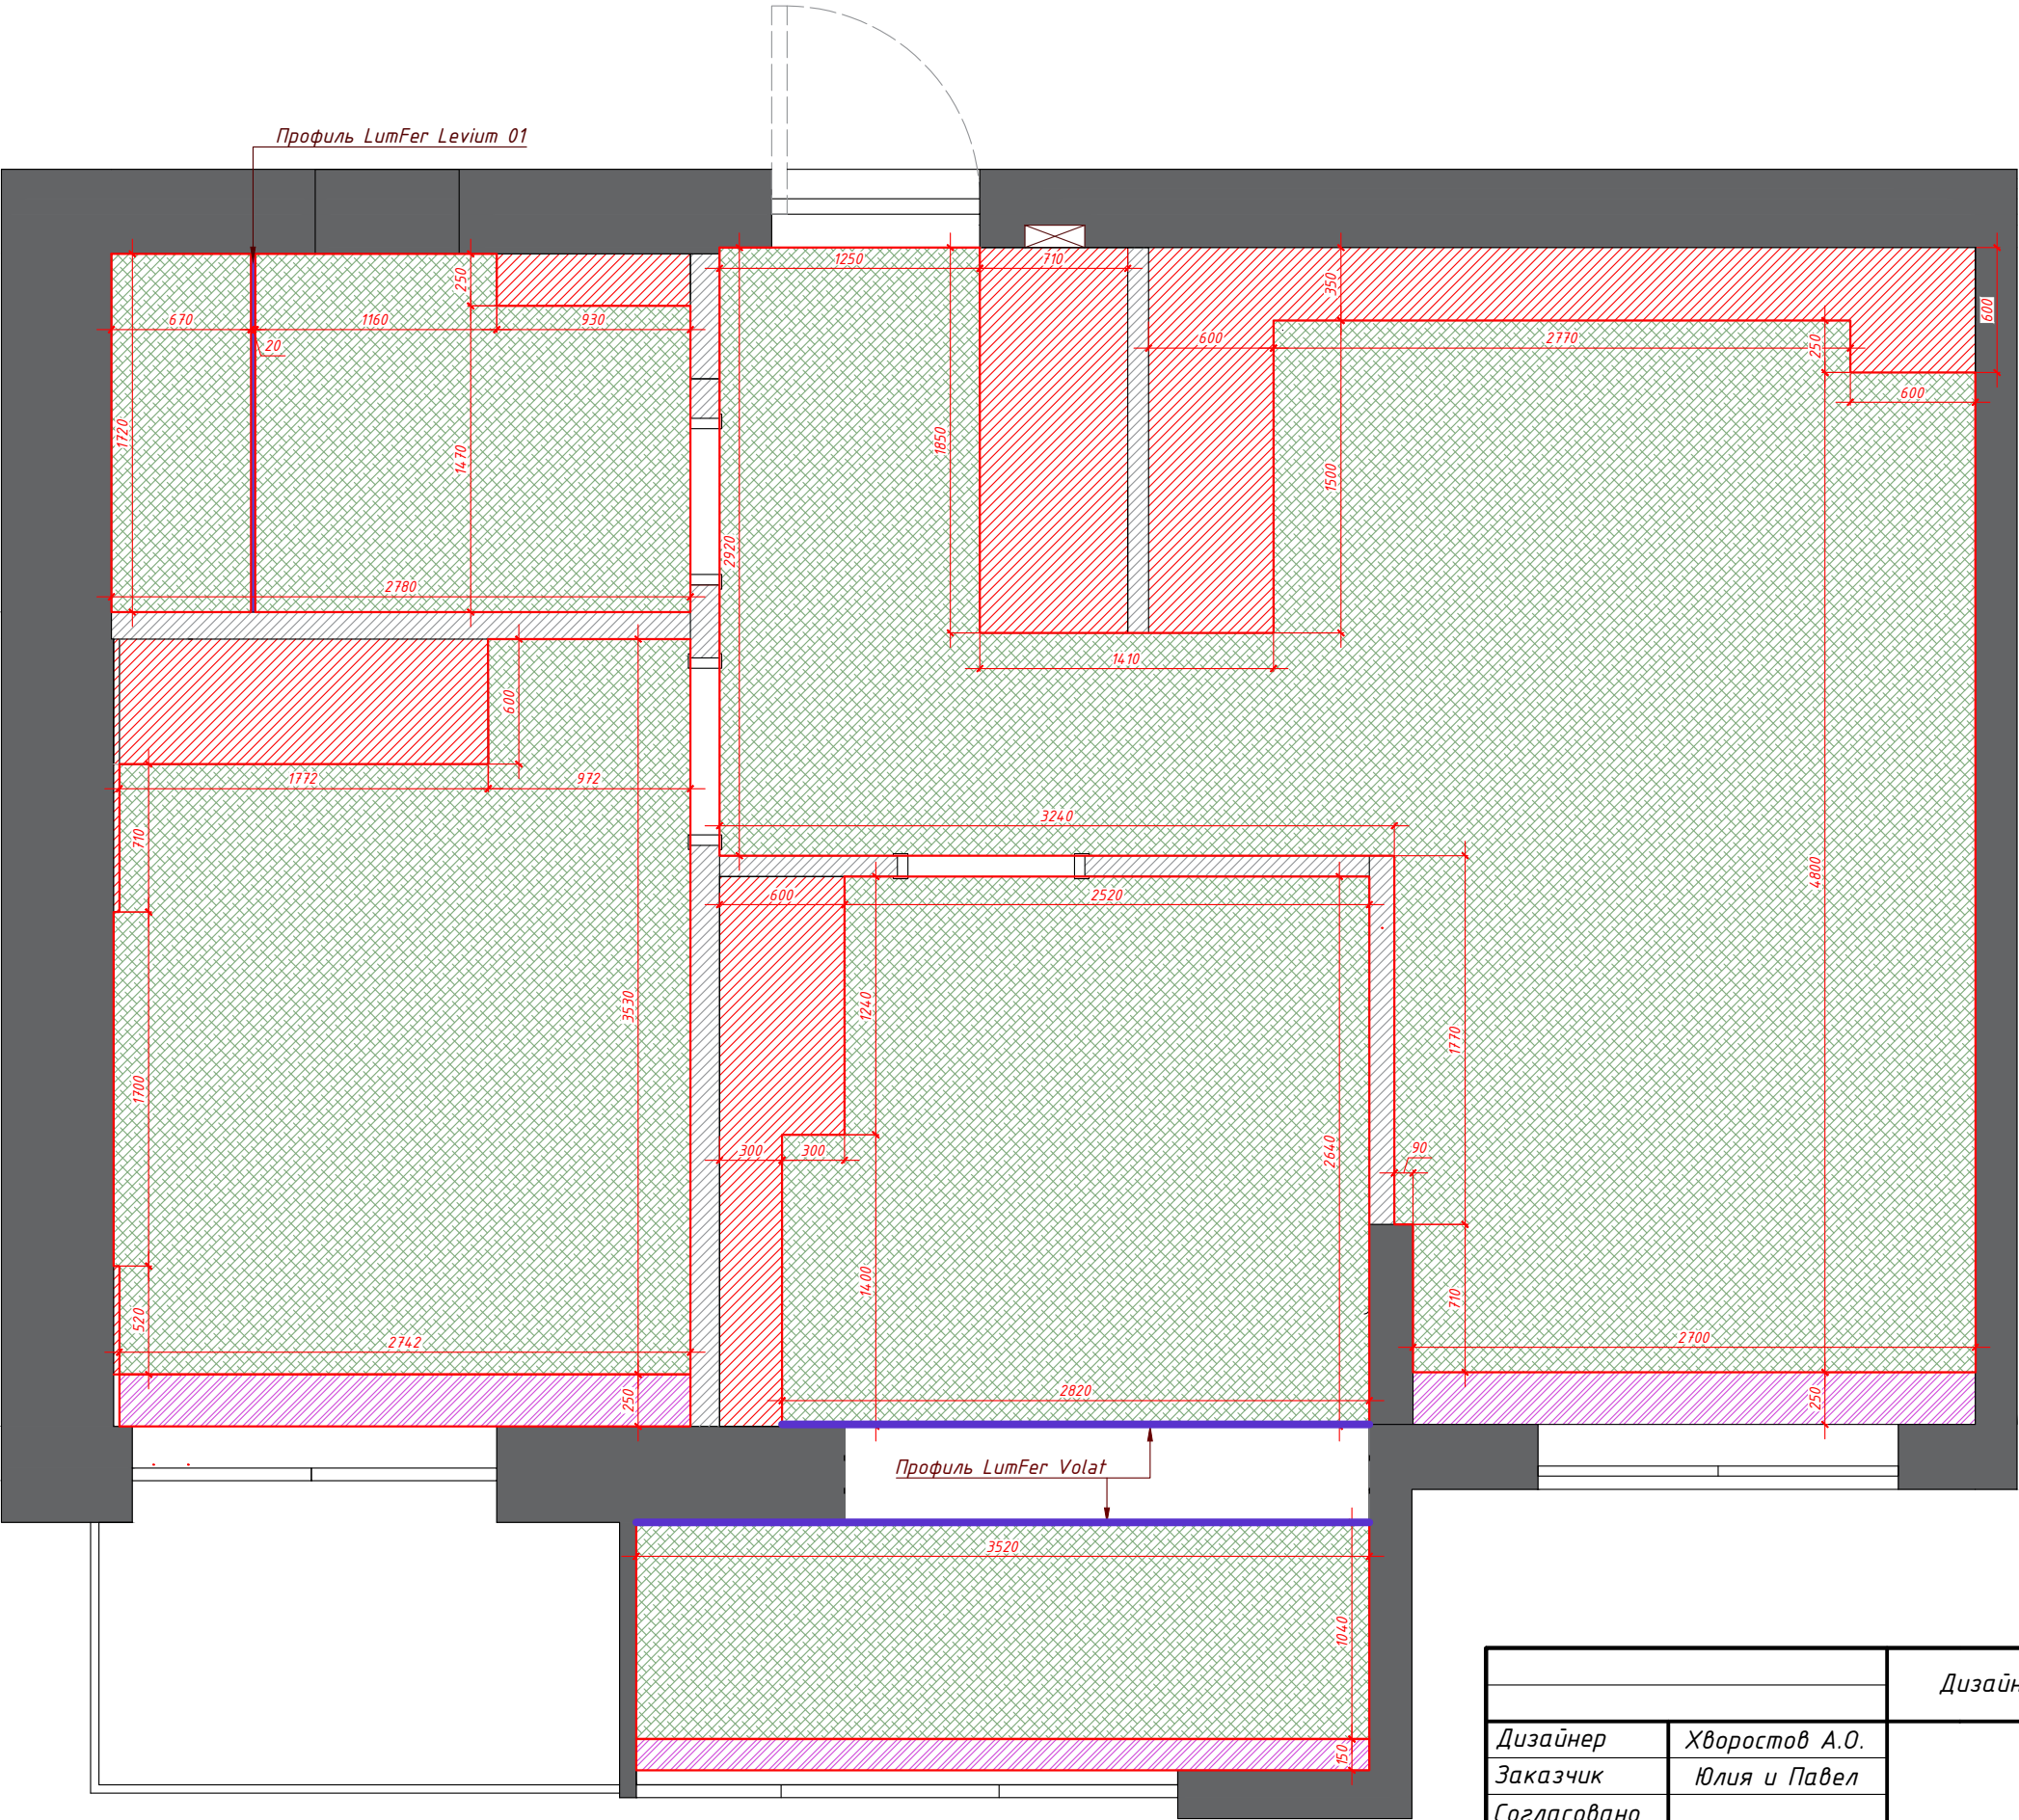


Условные обозначения		
	Натяжной потолок	45 м²
	Корпусная мебель	
	Профиль LumFer SK Magnum	9 м.п.

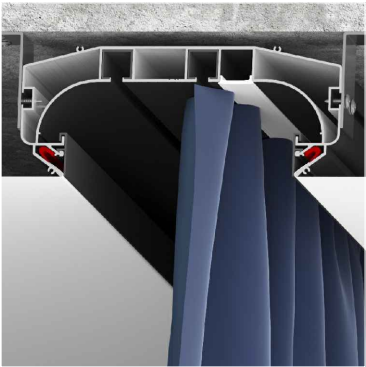


Профиль LumFer SK Magnum



Профиль LumFer Levium 01

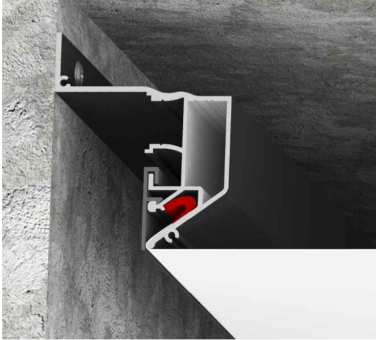


Профиль LumFer Volat

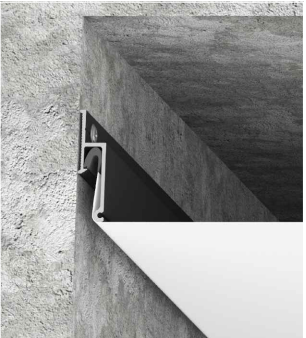


Профиль EuroLumFer 02 по всему периметру его используем.




		Дизайн-проект квартиры по ул. Миля 9	Стадия	Лист	Листов
			РП	17	49
Дизайнер	Хворостов А.О.	План потолков (1:35)			
Заказчик	Юлия и Павел				
Согласовано					
Дата	31.07.2026				

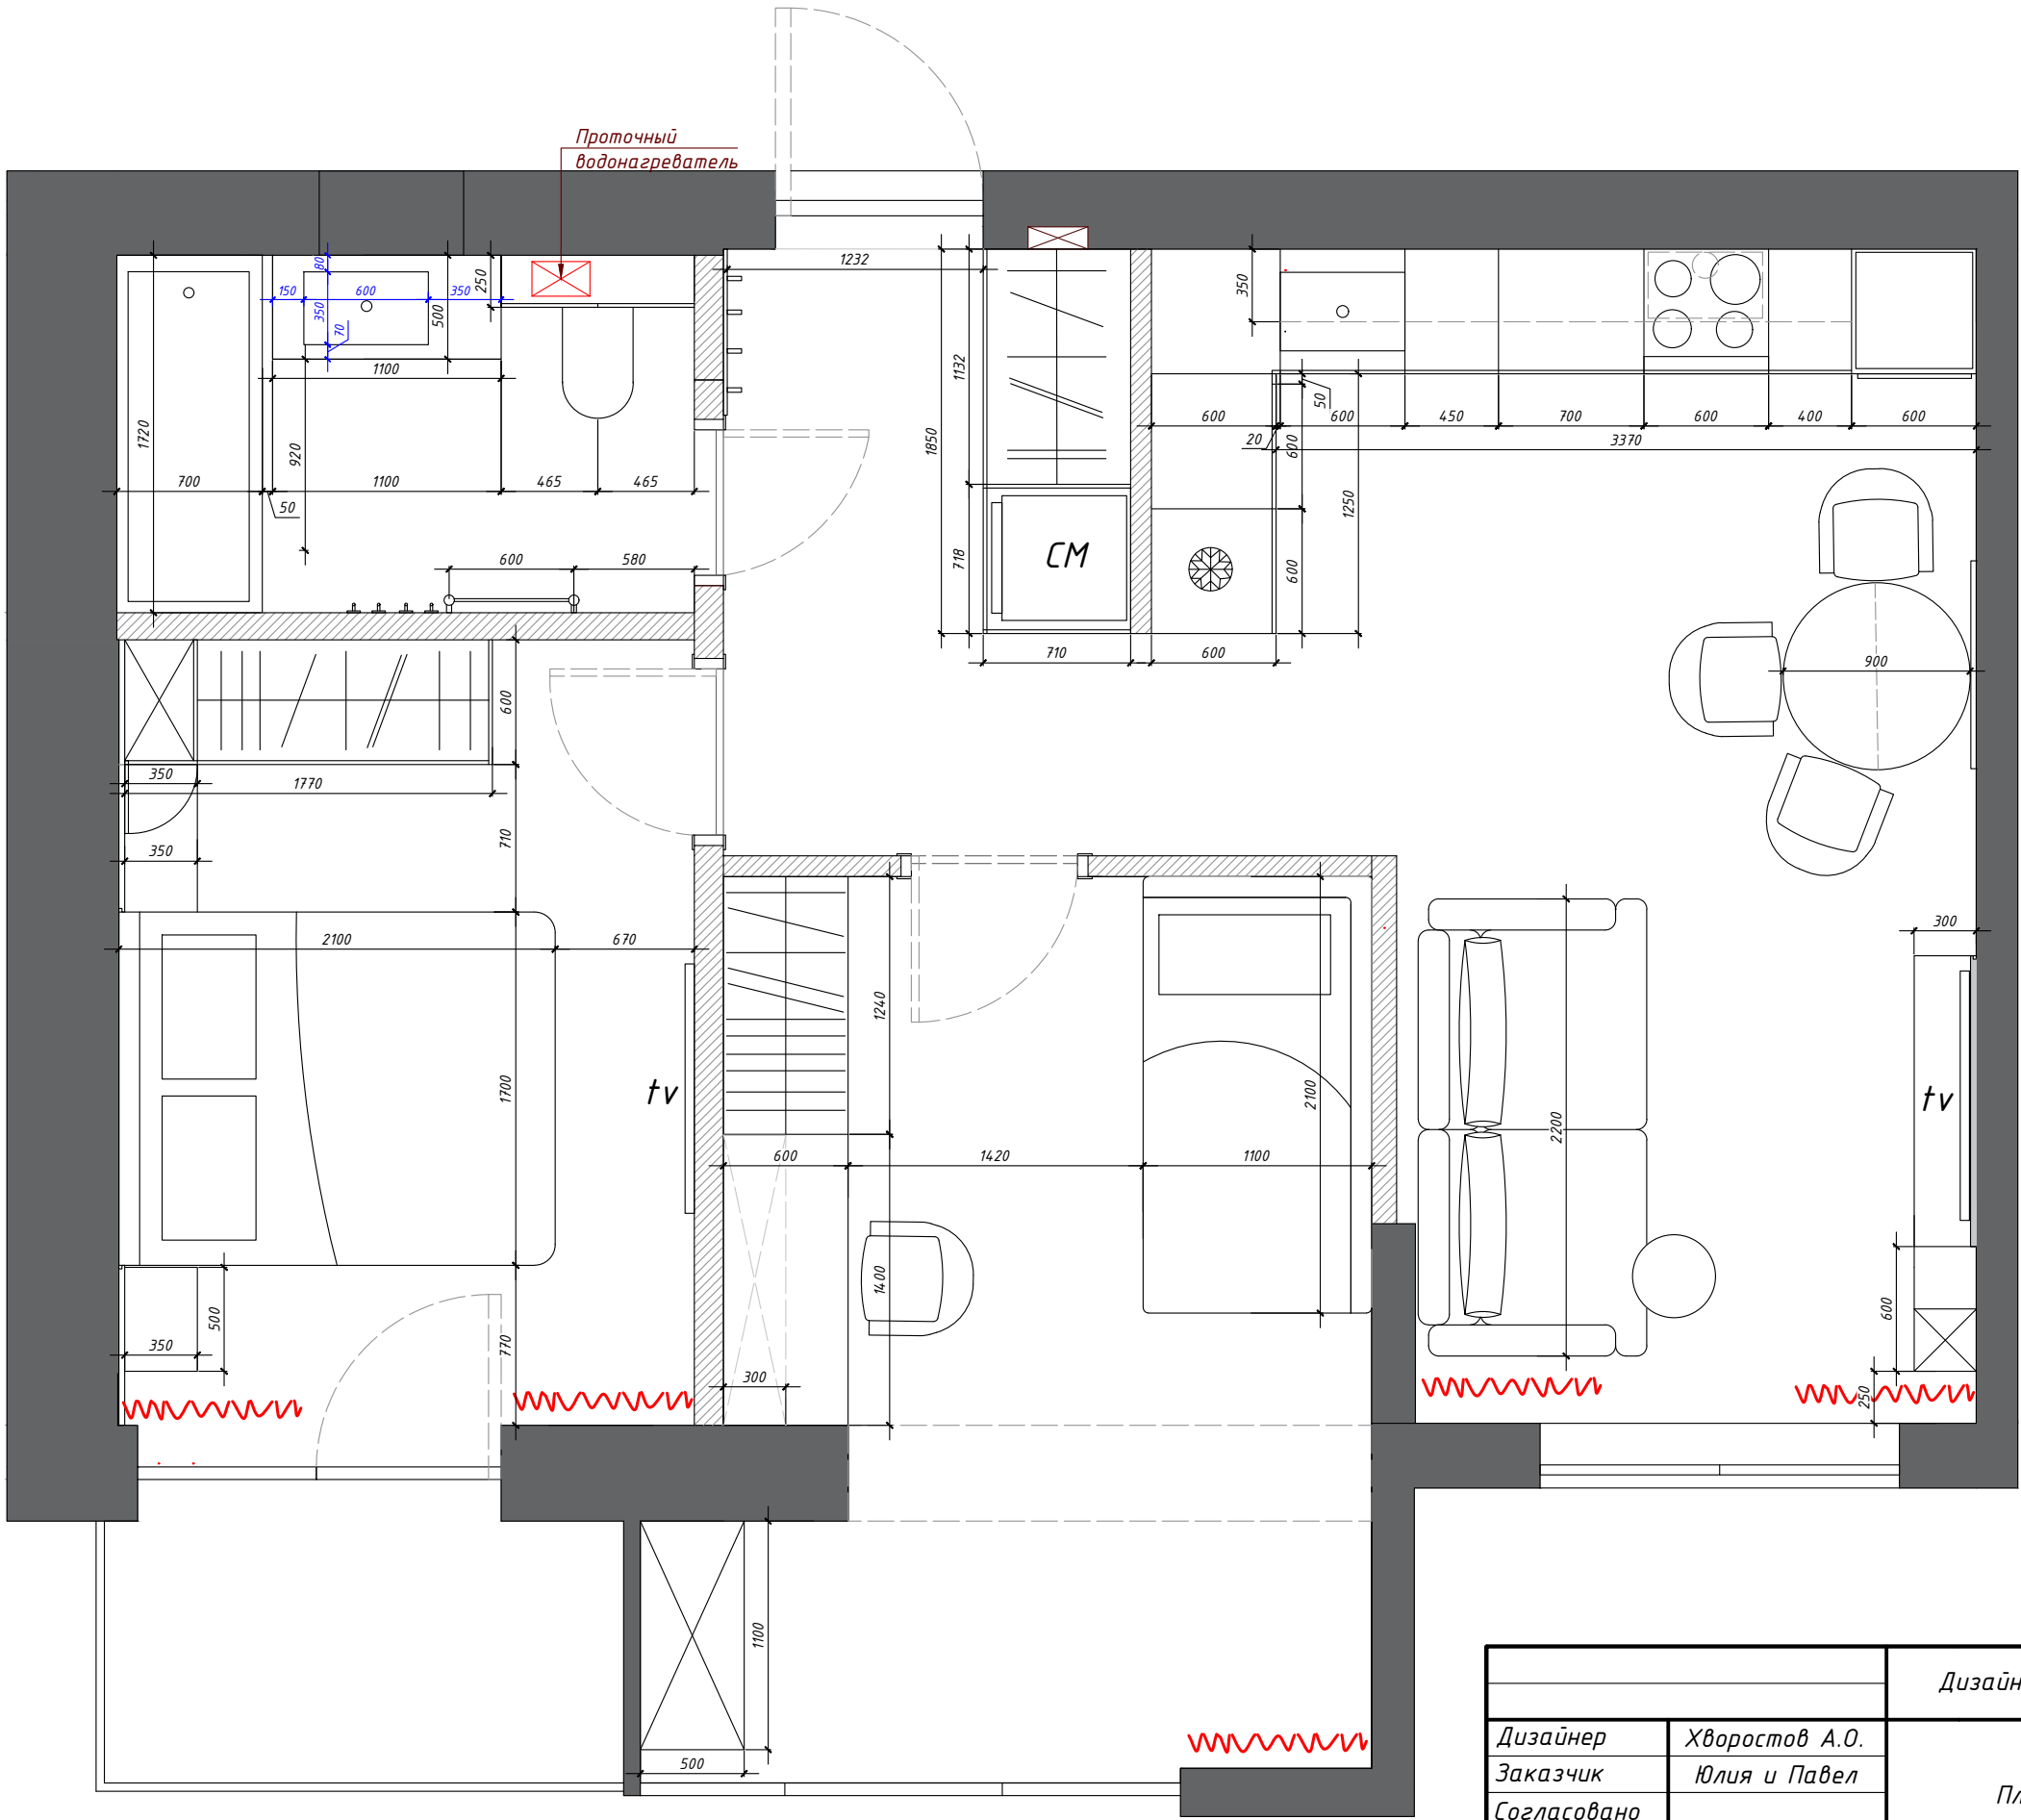

		Дизайн-проект квартиры по ул. Миля 9	Стадия	Лист	Листов
			РП	18	49
Дизайнер	Хворостов А.О.	План расстановки мебели (1:35)			
Заказчик	Юлия и Павел				
Согласовано					
Дата	31.07.2026				

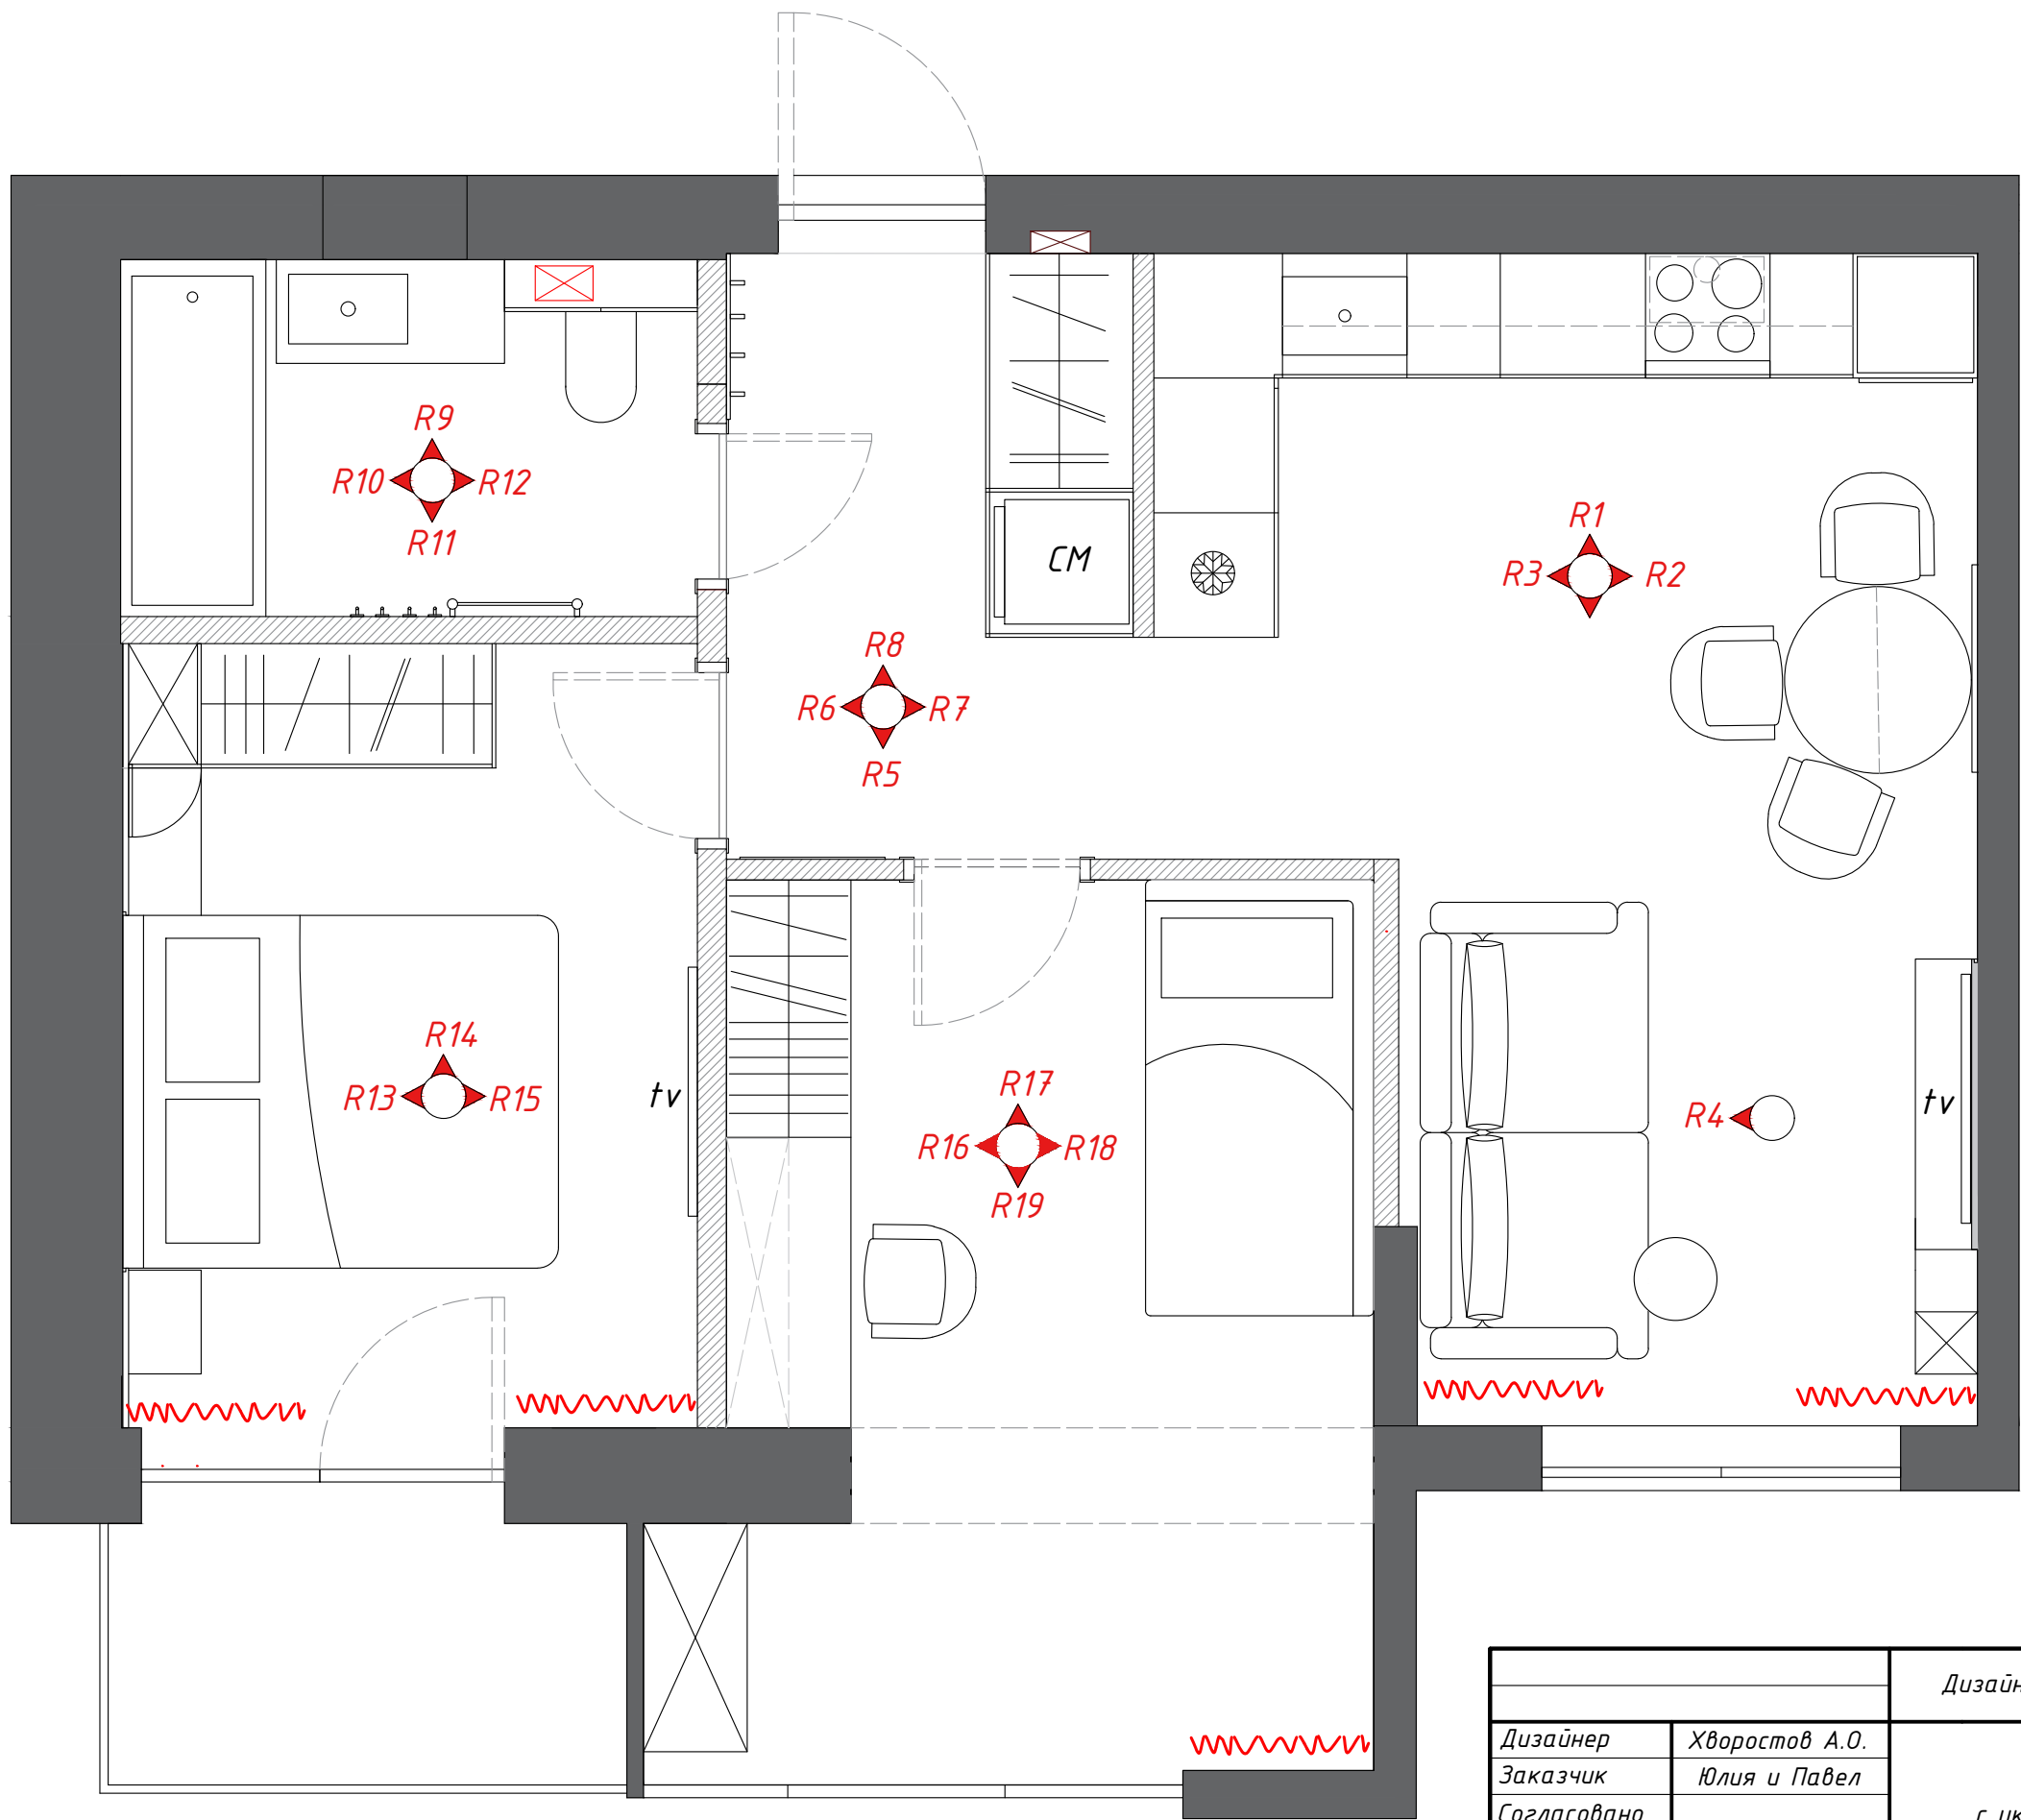

		Дизайн-проект квартиры по ул. Миля 9	Стадия	Лист	Листов
			РП	19	49
Дизайнер	Хворостов А.О.	План расстановки мебели с указанием развёрток стен (1:35)			
Заказчик	Юлия и Павел				
Согласовано					
Дата	31.07.2026				

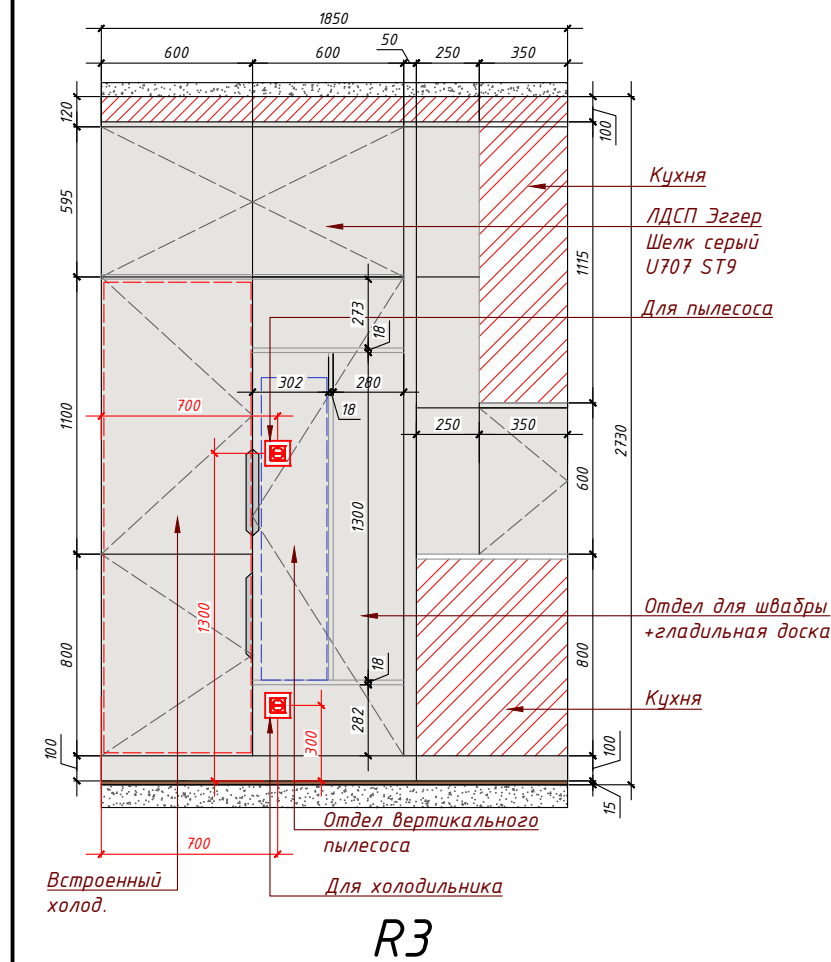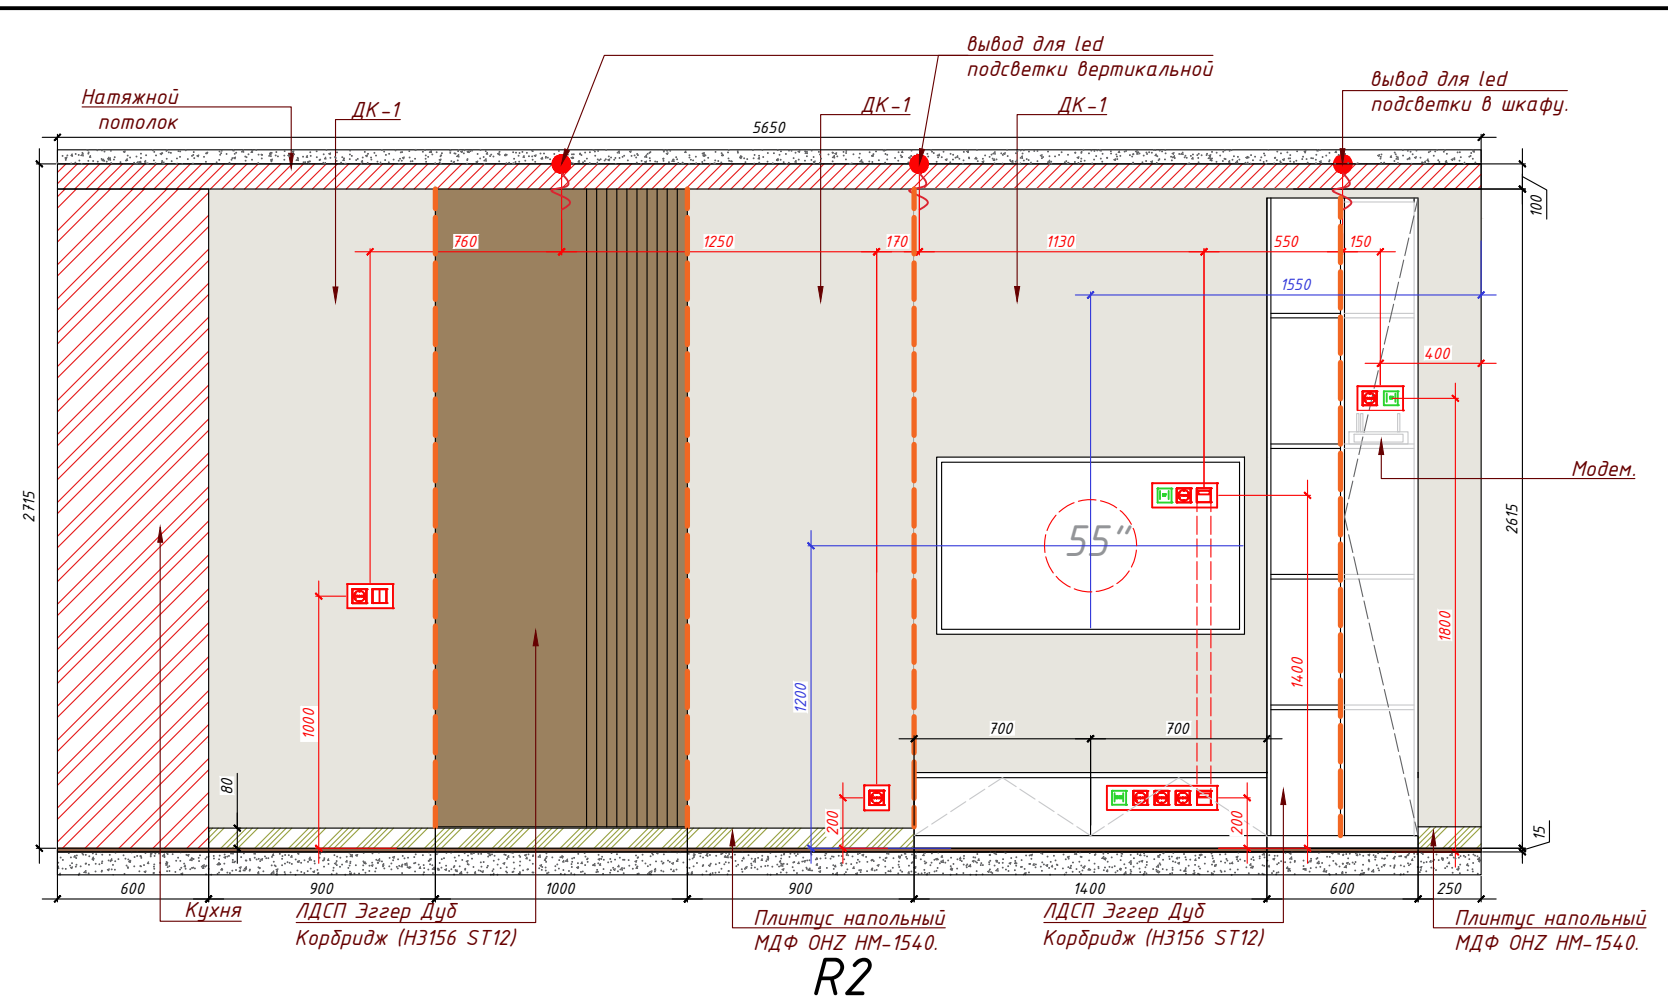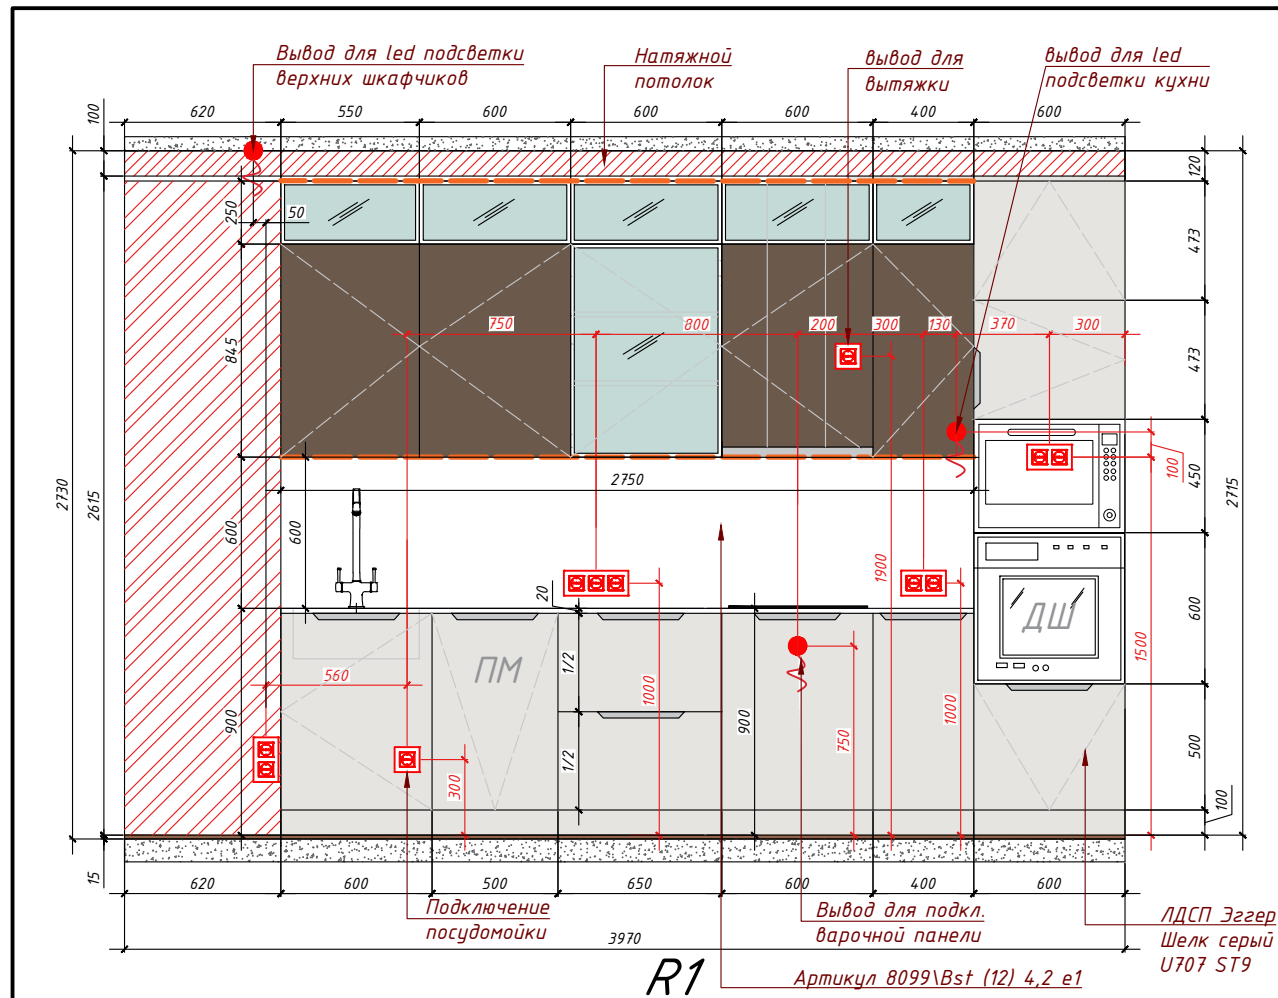






Условные обозначения

-  - Вывод эл.кабеля.
-  -Выключатель двухклавишный
-  -Розетка 220V
-  -Розетка RJ45 x 1 (internet)
-  -Розетка RJ45 x 2 (internet)
-  -Розетка заглушка кабелей

Примечание:

1. Допустимая погрешность в размерах 20 мм. При большей погрешности, по факту, скорректировать размеры по месту на усмотрение строительно-монтажной бригады, согласовать изменения с заказчиком или представителем авторского надзора, или лицом его представляющим.
2. Все размеры указаны с учетом штукатурного слоя. Габаритные размеры мебели даны с учетом всех слоев отделки стен. Все размеры привязок розеток, выключателей, пультов управления и электровыводов даны по центру прибора. Все высоты привязок розеток, выключателей, пультов управления и электровыводов даны от уровня чистового пола.
3. Размещение всех розеток, выключателей, пультов управления и электровыводов уточнить по месту и согласовать с заказчиком или представителем авторского надзора, или лицом его представляющим.
4. Перед проведением отделочных работ выполнить цветовые выкраски, согласовать все цвета с заказчиком или представителем авторского надзора, или лицом его представляющим.
5. Цвет отделочных материалов может быть скорректирован заказчиком самостоятельно
6. Все объемы по материалам посчитаны без учета запаса. Для определения общего количества материалов, просчет сметной стоимости и определения общего объема работ обязателен перерасчет со специалистом по месту.
7. Плитка показана условно. Раскладку плитки запросить в салоне и скорректировать по месту.

		Дизайн-проект квартиры по ул. Миля 9	Стадия	Лист	Листов
			РП	20	49
Дизайнер	Хворостов А.О.	Развёртки стен (1:35)			
Заказчик	Юлия и Павел				
Согласовано					
Дата	31.07.2026				

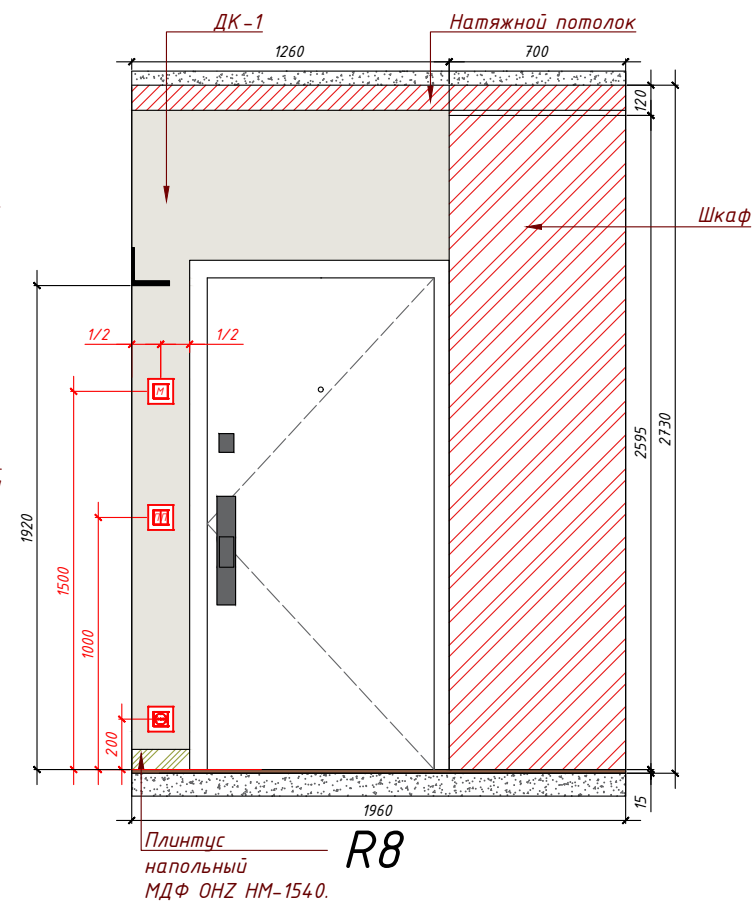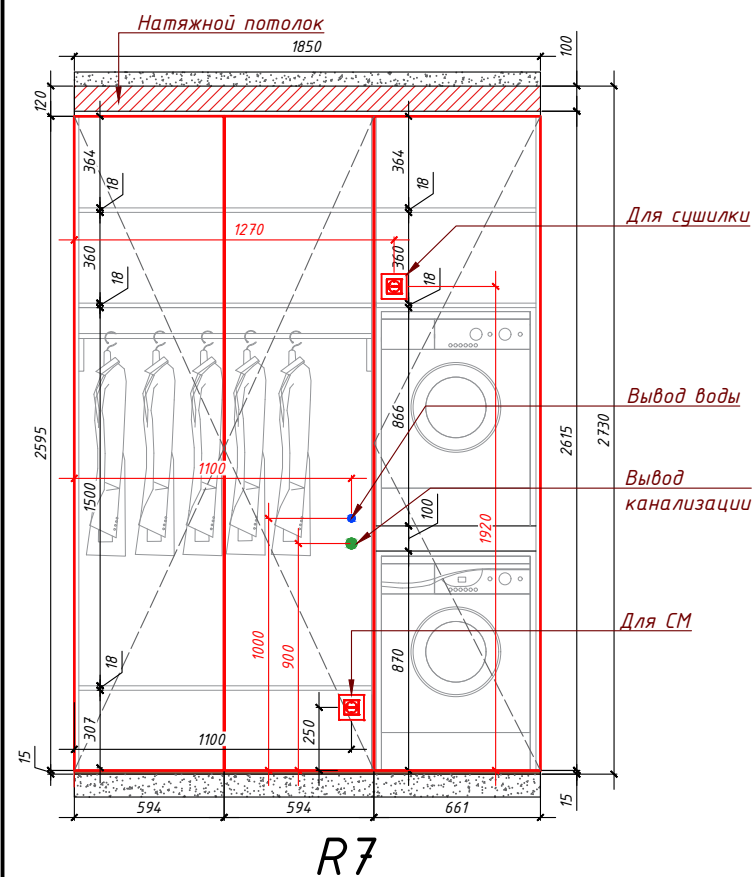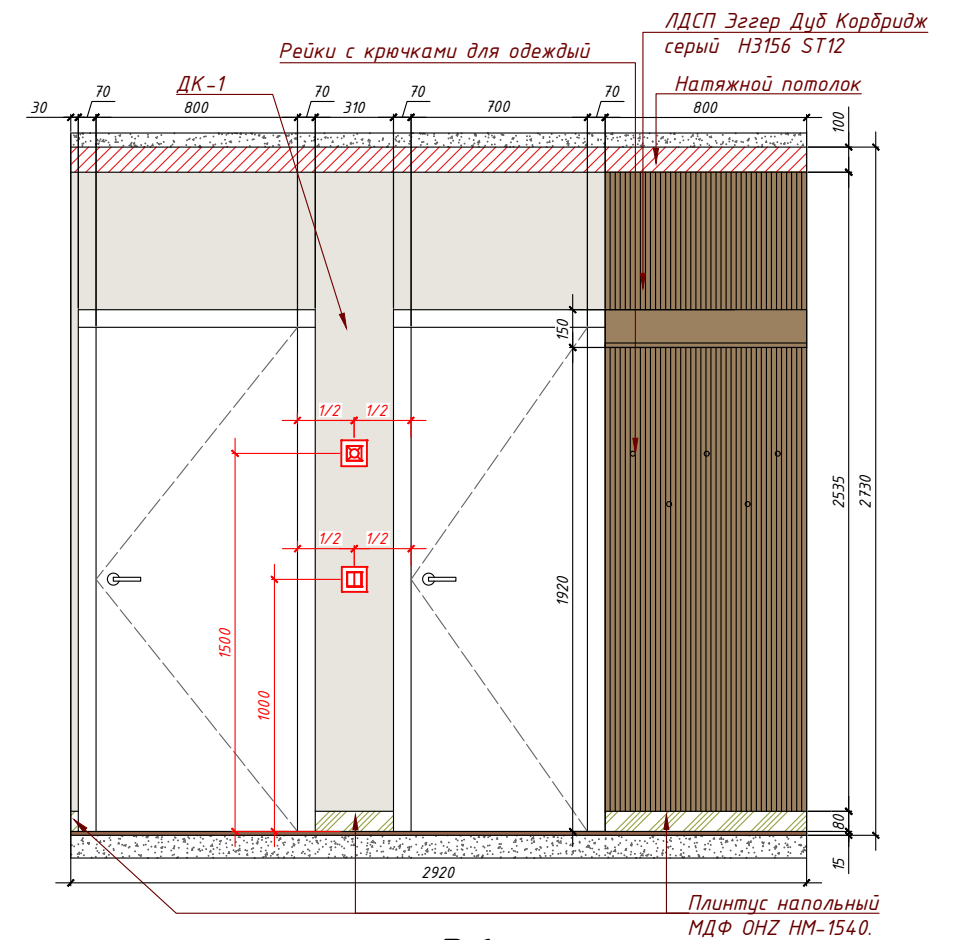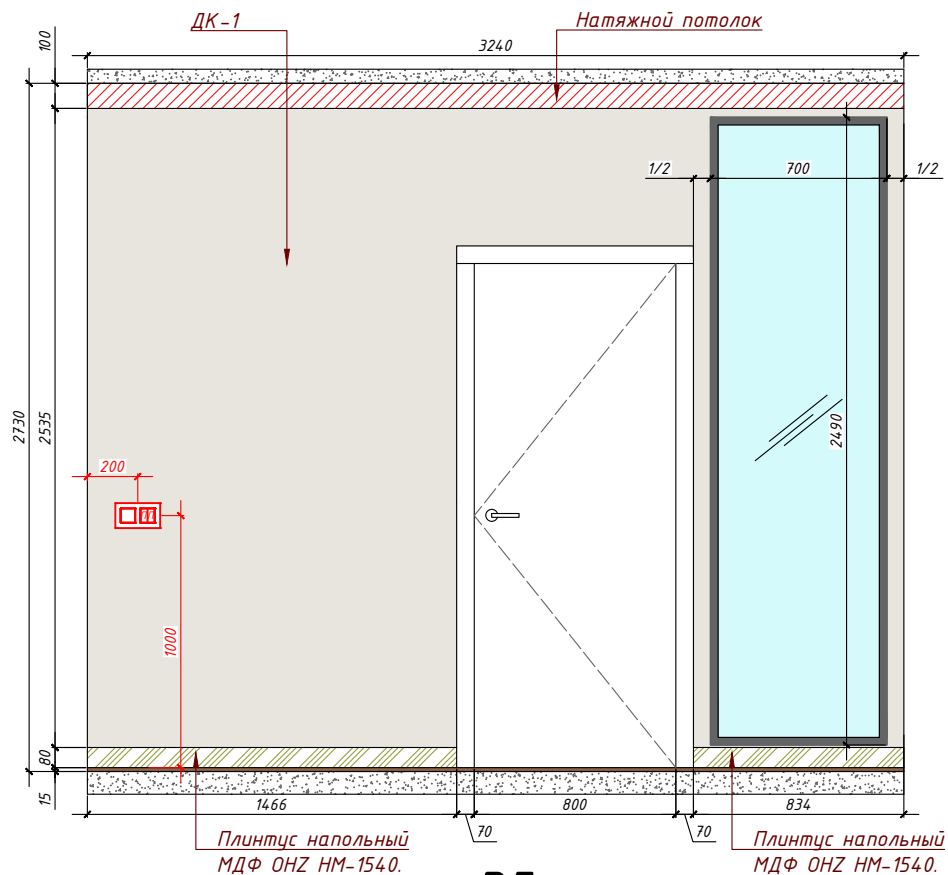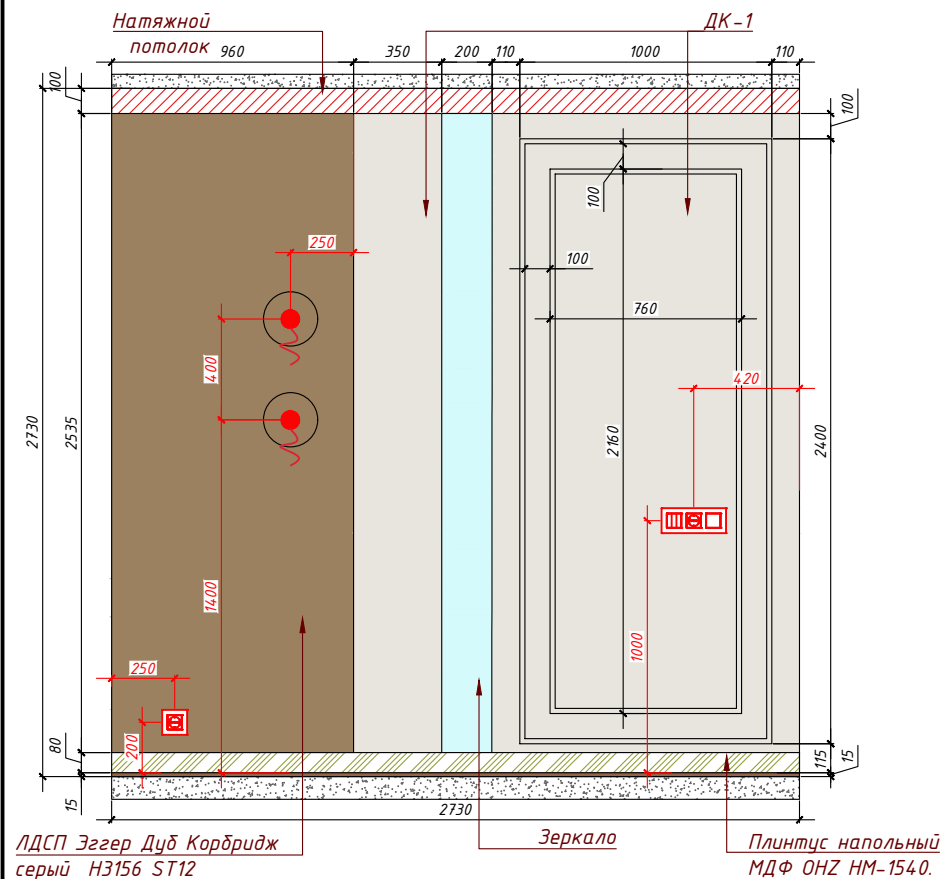

Условные обозначения




Примечание:

1. Допустимая погрешность в размерах 20 мм. При большой погрешности, по факту, скорректировать размеры по месту на усмотрение строительно-монтажной бригады, согласовать изменения с заказчиком или представителем авторского надзора, или лицом его представляющим.
2. Все размеры указаны с учетом штукатурного слоя. Габаритные размеры мебели даны с учетом всех слоев отделки стен. Все размеры привязок розеток, выключателей, пультов управления и электропроводов даны по центру прибора. Все высоты привязок розеток, выключателей, пультов управления и электропроводов даны от уровня чистового пола.
3. Размещение всех розеток, выключателей, пультов управления и электропроводов уточнить по месту и согласовать с заказчиком или представителем авторского надзора, или лицом его представляющим.
4. Перед проведением отделочных работ выполнить цветковые выкраски, согласовать все цвета с заказчиком или представителем авторского надзора, или лицом его представляющим.
5. Цвет отделочных материалов может быть скорректирован заказчиком самостоятельно
6. Все объемы по материалам посчитаны без учета запаса. Для определения общего количества материалов, просчет сменной стоимости и определения общего объема работ обязателен перерасчет со специалистом по месту.
7. Плитка показана условно. Раскладку плитки запросить в салоне и скорректировать по месту.

		Дизайн-проект квартиры по ул. Милля 9	Стадия	Лист	Листов
			РП	21	49
Дизайнер	Хворостов А.О.	Развёртки стен (1:35)			
Заказчик	Юлия и Павел				
Согласовано					
Дата	31.07.2026				







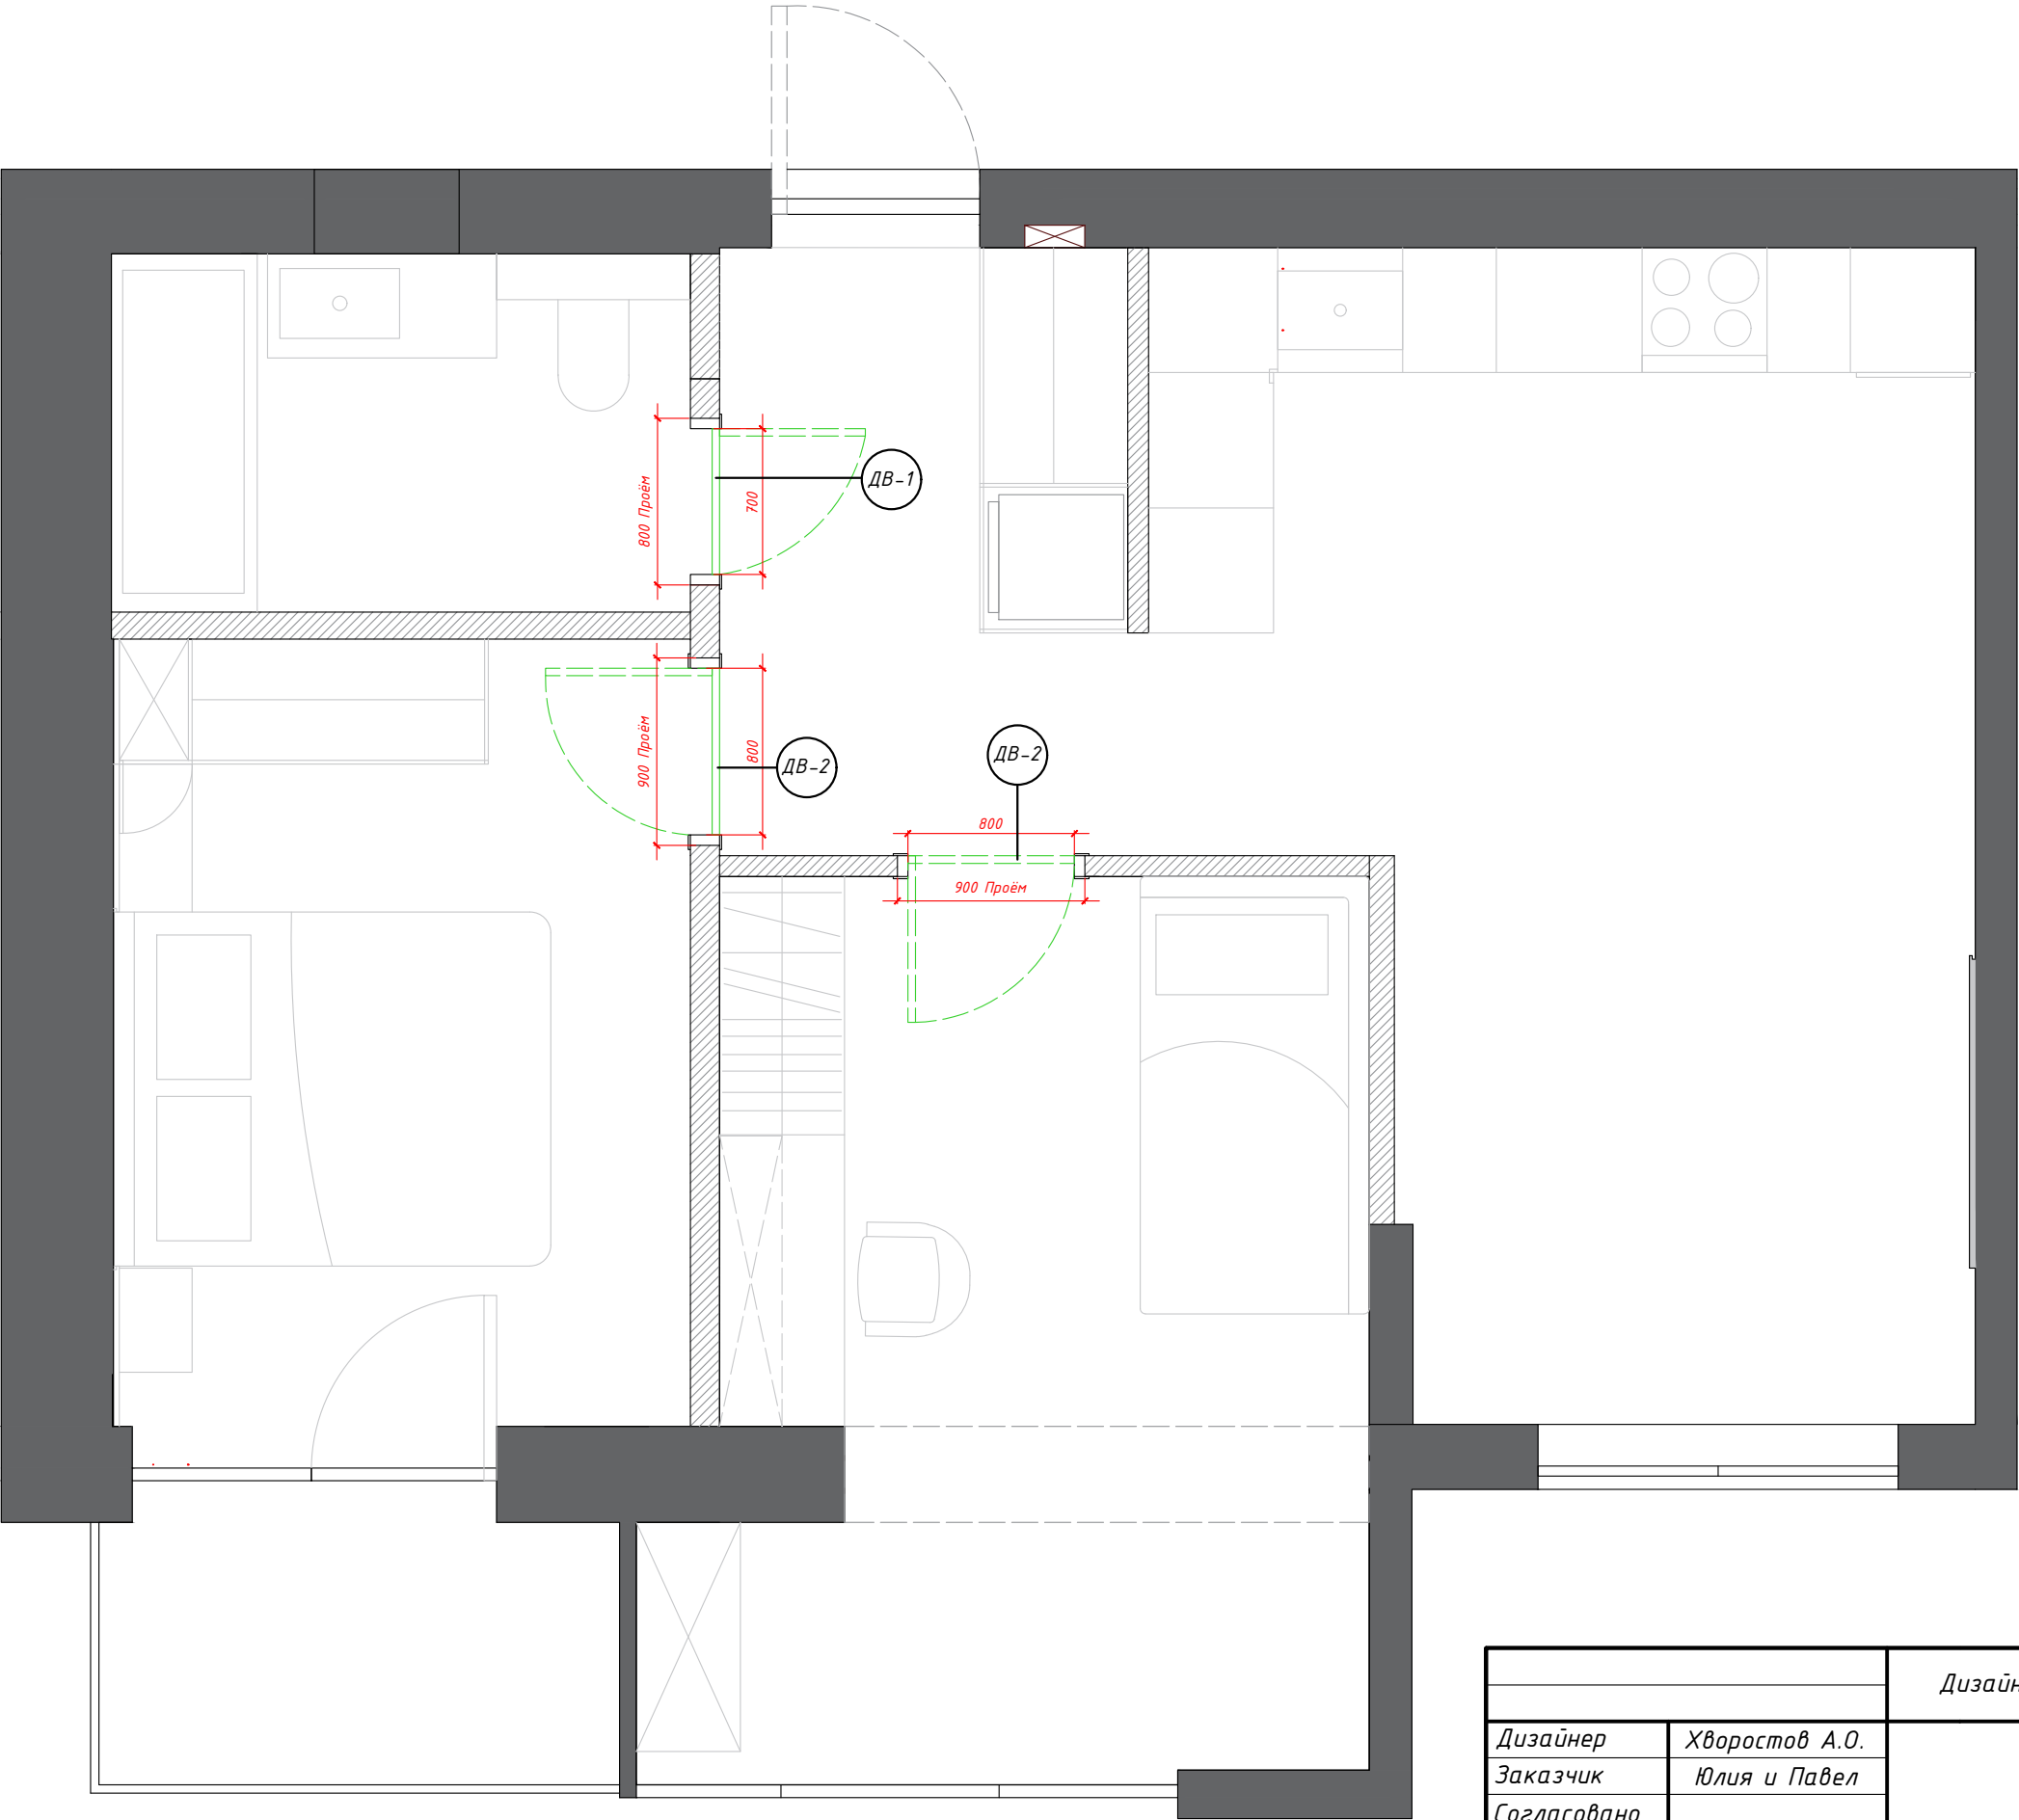

Спецификация межкомнатных дверей		
ДВ-1	Межкомнатная дверь 700мм.	1 шт.
ДВ-2	Межкомнатная дверь 800мм. (реверс)	2 шт.

Примечание:
1. Перед заказом заполнения дверных проемов выполнить замеры существующих дверных проемов по факту.
2. Размеры дверных проемов могут быть изменены согласно рекомендациям производителя.
3. Монтаж дверных проемов осуществлять согласно рекомендациям производителя.
4. Точные размеры дверных полотен уточнить у производителя.
5. Высота проема указана без учета чистовых покрытий, с учетом штукатурки потолка

		Дизайн-проект квартиры по ул. Миля 9	Стадия	Лист	Листов
			РП	15	49
Дизайнер	Хворостов А.О.	План дверей (1:35)			
Заказчик	Юлия и Павел				
Согласовано					
Дата	31.07.2026				

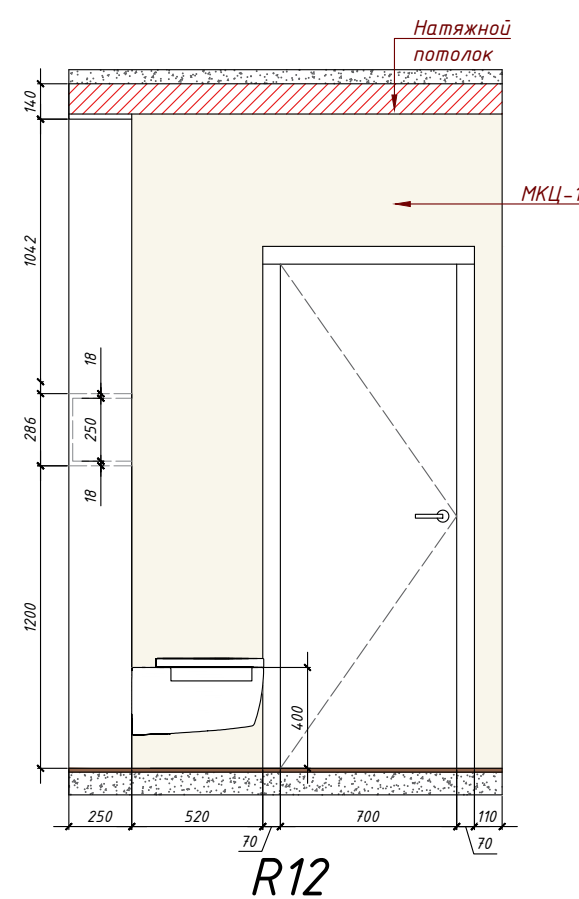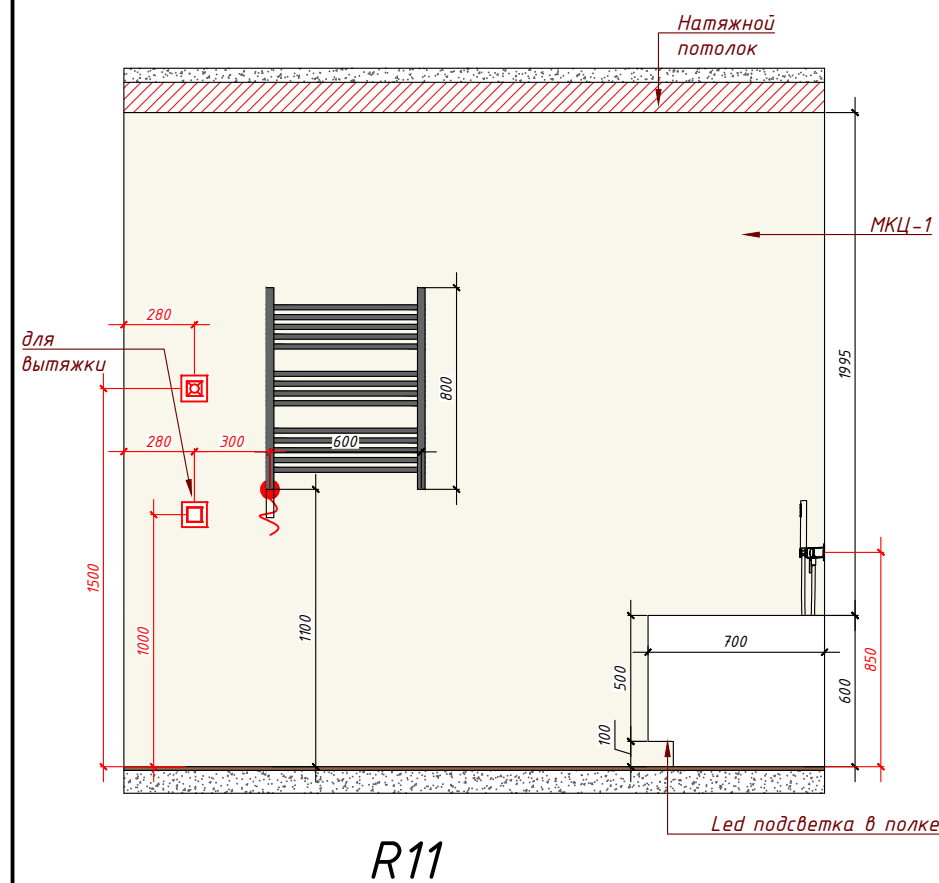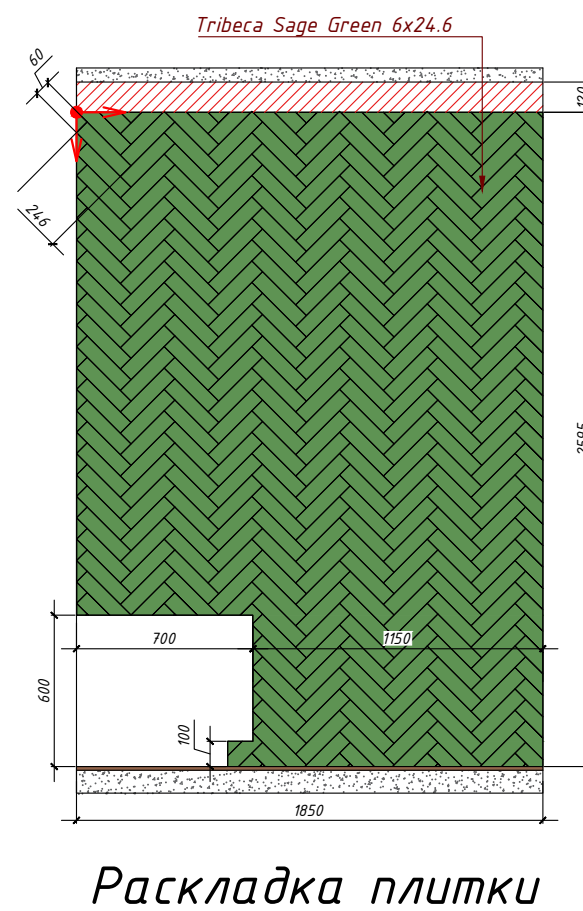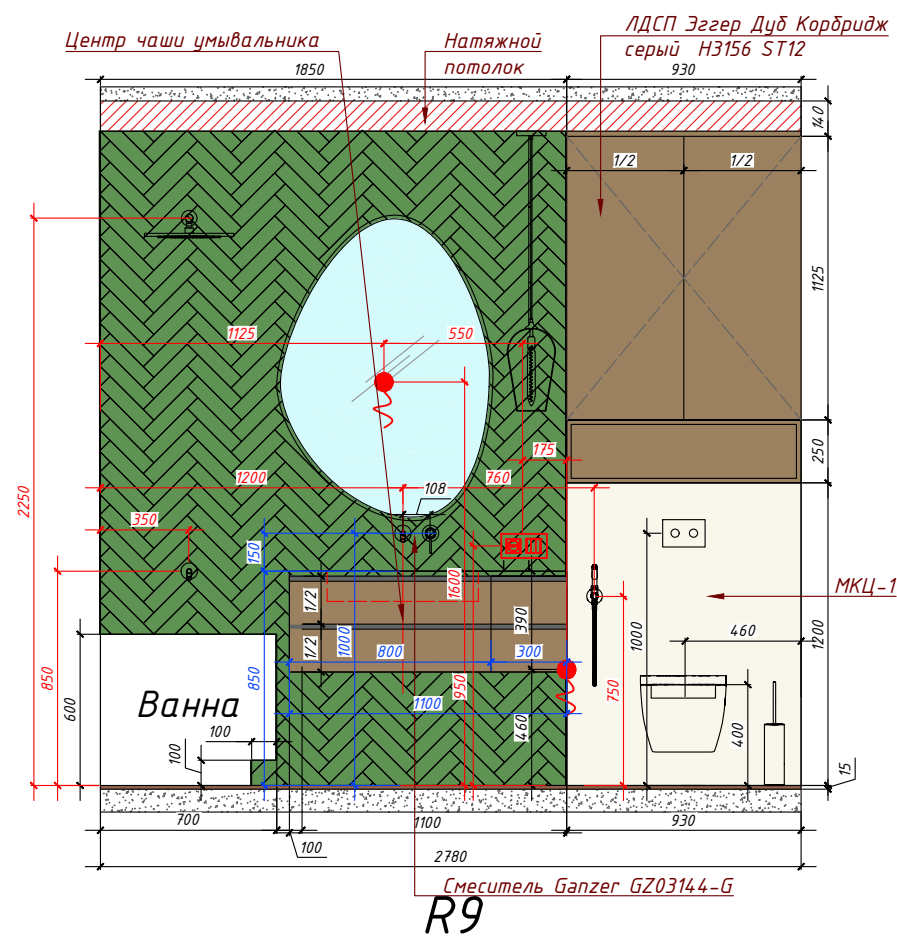


Условные обозначения

- Вывод эл.кабеля.
- Розетка 220V.
- Выключатель одноклавишный
- Выключатель трёхклавишный
- Направление начала раскладки плитки


Примечание:

- Допустимая погрешность в размерах 20 мм. При большей погрешности, по факту, скорректировать размеры по месту на усмотрение строительно-монтажной бригады, согласовать изменения с заказчиком или представителем авторского надзора, или лицом его представляющим.
- Все размеры указаны с учетом штукатурного слоя. Габаритные размеры мебели даны с учетом всех слоев отделки стен. Все размеры привязок розеток, выключателей, пультов управления и электропроводов даны по центру прибора. Все высоты привязок розеток, выключателей, пультов управления и электропроводов даны от уровня чистового пола.
- Размещение всех розеток, выключателей, пультов управления и электропроводов уточнить по месту и согласовать с заказчиком или представителем авторского надзора, или лицом его представляющим.
- Перед проведением отделочных работ выполнить цветковые выкраски, согласовать все цвета с заказчиком или представителем авторского надзора, или лицом его представляющим.
- Цвет отделочных материалов может быть скорректирован заказчиком самостоятельно
- Все объемы по материалам посчитаны без учета запаса. Для определения общего количества материалов, просчетов сметной стоимости и определения общего объема работ обязателен перерасчет со специалистом по месту.
- Плитка показана условно. Раскладку плитки запросить в салоне и скорректировать по месту.


		Дизайн-проект квартиры по ул. Миля 9	Стадия	Лист	Листов
			РП	22	49
Дизайнер	Хворостов А.О.	Развёртки стен (1:35)			
Заказчик	Юлия и Павел				
Согласовано					
Дата	31.07.2026				

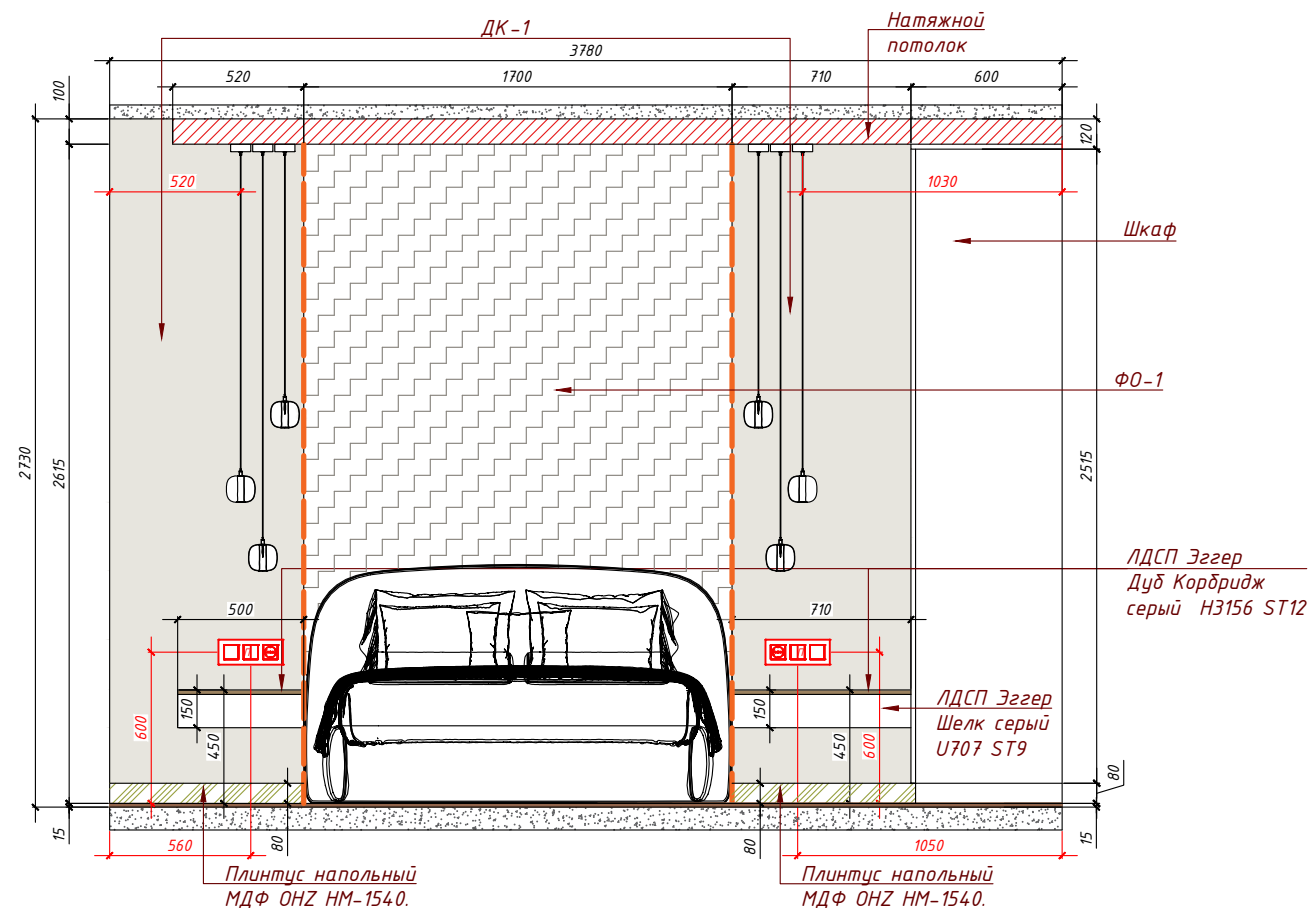

R13

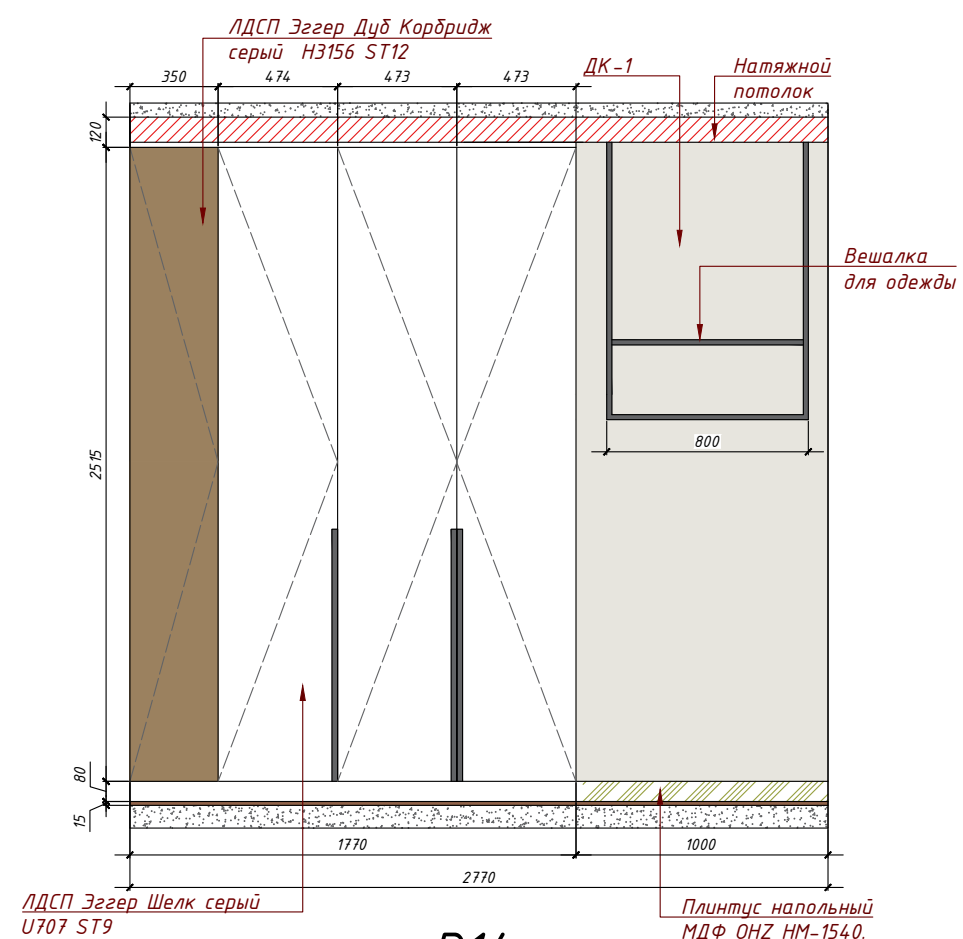

R14

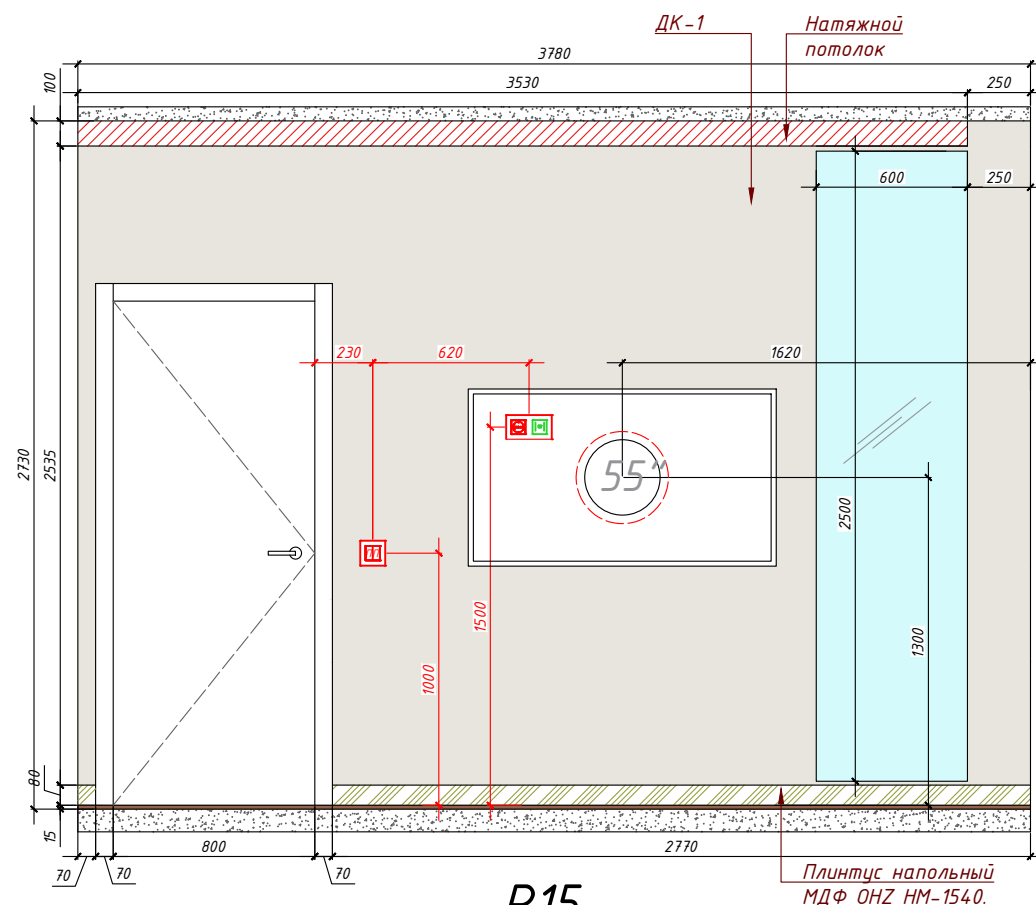



R15

-  -Розетка 220V.
-  -Выключатель одноклавишный
-  -Выключатель двухклавишный, одна клавиша проходная
-  -Выключатель двухклавишный проходной
-  -Розетка RJ45 x 1 (internet)

Примечание:

1. Допустимая погрешность в размерах 20 мм. При большей погрешности, по факту, скорректировать размеры по месту на усмотрение строительно-монтажной бригады, согласовать изменения с заказчиком или представителем авторского надзора, или лицом его представляющим.
2. Все размеры указаны с учетом штукатурного слоя. Габаритные размеры мебели даны с учетом всех слоев отделки стен. Все размеры привязок розеток, выключателей, пультов управления и электровыводов даны по центру прибора. Все высоты привязок розеток, выключателей, пультов управления и электровыводов даны от уровня чистового пола.
3. Размещение всех розеток, выключателей, пультов управления и электровыводов уточнить по месту и согласовать с заказчиком или представителем авторского надзора, или лицом его представляющим.
4. Перед проведением отделочных работ выполнить цветовые выкраски, согласовать все цвета с заказчиком или представителем авторского надзора, или лицом его представляющим.
5. Цвет отделочных материалов может быть скорректирован заказчиком самостоятельно.
6. Все объемы по материалам посчитаны без учета запаса. Для определения общего количества материалов, просчетов сметной стоимости и определения общего объема работ обязателен перерасчет со специалистом по месту.
7. Плитка показана условно. Раскладку плитки запросить в салоне и скорректировать по месту.

		Дизайн-проект квартиры по ул. Миля 9	Стадия	Лист	Листов
			РП	23	49
Дизайнер	Хворостов А.О.	Развёртки стен (1:35)			
Заказчик	Юлия и Павел				
Согласовано					
Дата	31.07.2026				

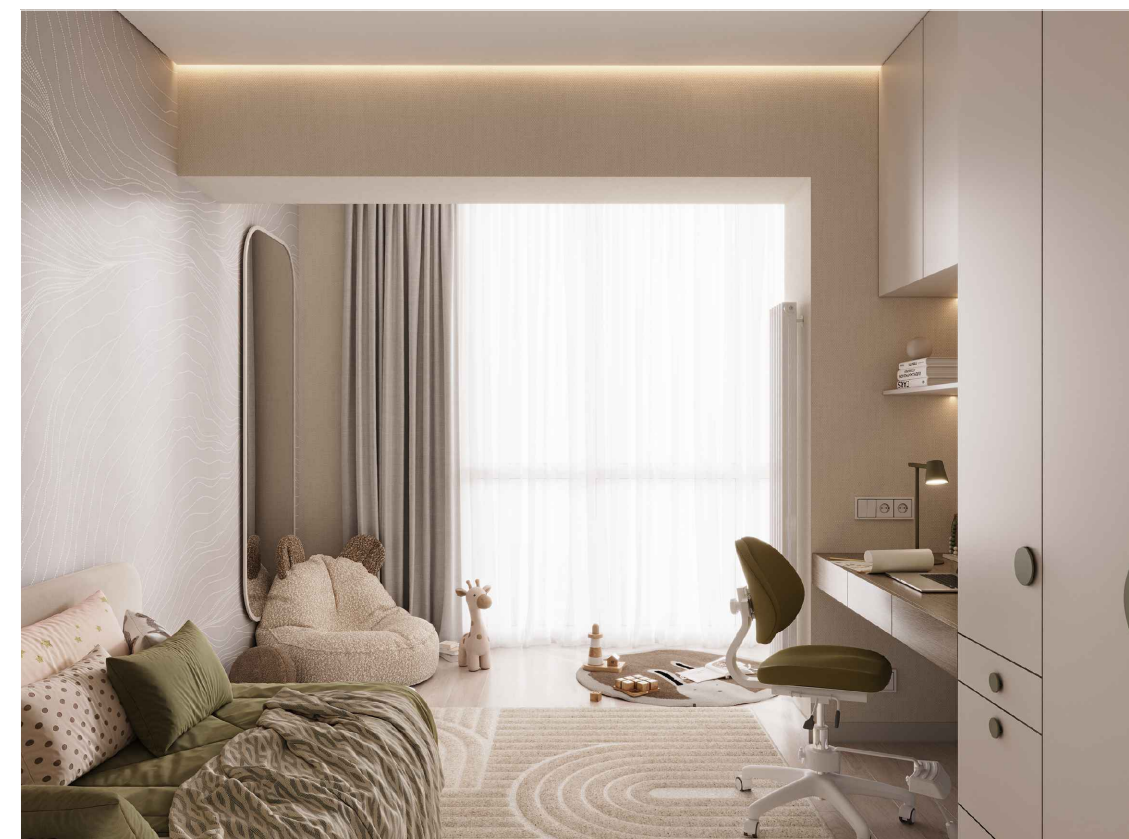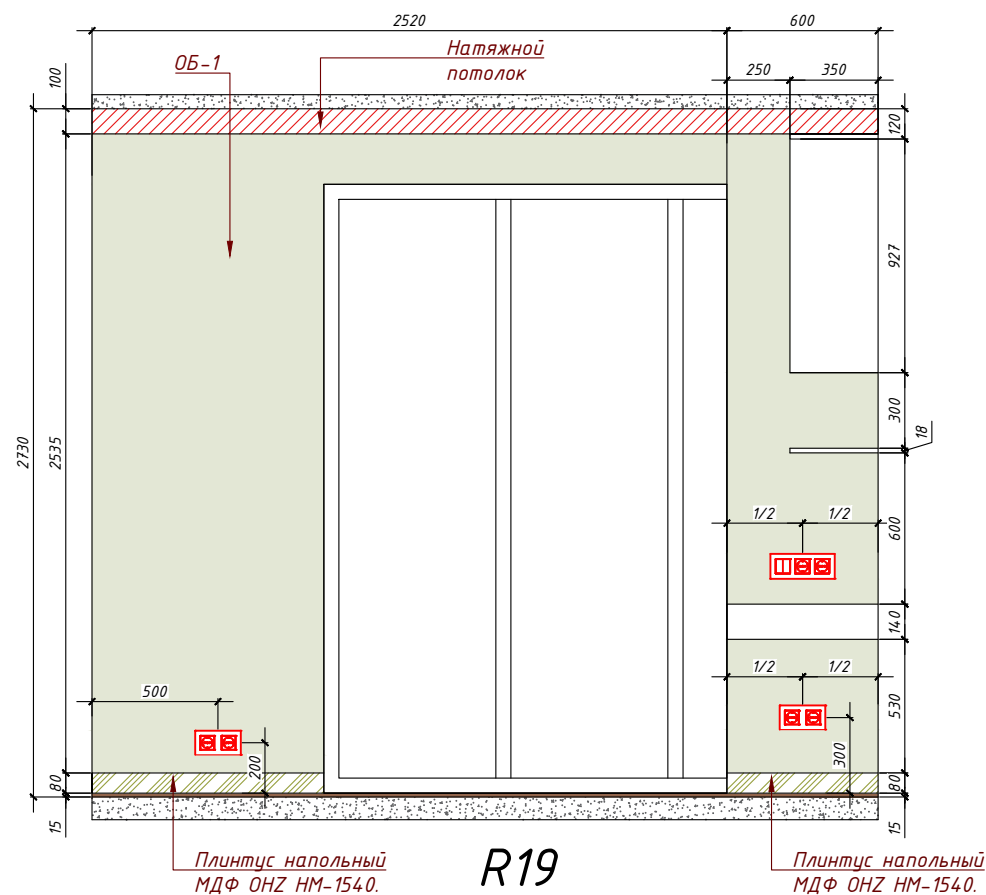

Условные обозначения

-  -Выключатель двухклавишный
-  -Розетка 220V

- Примечание:
- Допустимая погрешность в размерах 20 мм. При большей погрешности, по факту, скорректировать размеры по месту на усмотрение строительно-монтажной бригады, согласовать изменения с заказчиком или представителем авторского надзора, или лицом его представляющим.
 - Все размеры указаны с учетом штукатурного слоя. Габаритные размеры мебели даны с учетом всех слоев отделки стен. Все размеры привязок розеток, выключателей, пультов управления и электропроводов даны по центру прибора. Все высоты привязок розеток, выключателей, пультов управления и электропроводов даны от уровня чистового пола.
 - Размещение всех розеток, выключателей, пультов управления и электропроводов уточнить по месту и согласовать с заказчиком или представителем авторского надзора, или лицом его представляющим.
 - Перед проведением отделочных работ выполнить цветовые выкраски, согласовать все цвета с заказчиком или представителем авторского надзора, или лицом его представляющим.
 - Цвет отделочных материалов может быть скорректирован заказчиком самостоятельно.
 - Все объемы по материалам посчитаны без учета запаса. Для определения общего количества материалов, просчетов сметной стоимости и определения общего объема работ обязателен перерасчет со специалистом по месту.
 - Плитка показана условно. Раскладку плитки запросить в салоне и скорректировать по месту.

		Дизайн-проект квартиры по ул. Миля 9	Стадия	Лист	Листов
			РП	25	49
Дизайнер	Хворостов А.О.	Развёртки стен (1:35)			
Заказчик	Юлия и Павел				
Согласовано					
Дата	31.07.2026				

№1		Инсталяция для подвесного унитаза TECE.	1шт.	https://www.instagram.com/salon_keytown?igsh=MXg2bWdoNmRlbjNrYw==		Диван	1шт.	https://artestudio.by/
№2		Унитаз подвесной Rosa The Gap Clean Rim (арт.34647L000), 54х34, безободковый, с крышкой SoftClose Supralit	1шт.			Межкомнатные двери	3шт.	https://www.instagram.com/homeporte.by?igsh=MWEyand3bmNtMTVubw==
№3		Стальная ванна Kaldewei Eurowa 170х70, 119812030001+ ножки и шумоизоляция.	1шт.			Входные двери	1шт.	https://joinery.by/
№4		Сунержа Богема 3.1 прямая 800х500 МЭМ правый	1шт.			Кварцвинил		https://alexparket.by/ или https://ecopol.by/viniloviy-pol/viniloviy-pol-Quick-Step/pvh-plitka-pristine-sghbc20331-dub-bezmyafegnyj-naturalnyj-svetlyj.html
№5		Клавиша смыва для инсталяции	1шт.			Керамогранит		https://terracotta.by/
№6		Зеркало с подсветкой	1шт.	https://www.instagram.com/zerkala.minsk?igsh=a3h2dWg2Mzk5c2Ns		Кухонный стол	1шт.	https://www.instagram.com/aleksei.mebel?igsh=ZXZ6cnhrNDQ5Z213
№7		Умывальник под заказ вылить	1шт.			Стулья	3шт.	https://hypemebel.by/
№8		Скрытый смеситель для раковины MOZA 316L	1шт.			Кровать	1шт.	https://artestudio.by/
№9		Душевая система MOZA из стали 316L со скрытым сливом и смесителем на 3 отверстия с двумя режимами работы.	1шт.			Освещение		https://eurosvet.by/
№10		Скрытый смеситель для биде MOZA CHROME	1шт.			Детская кровать	1шт.	https://artestudio.by/
№11		Смеситель для кухонной мойки Vieir V15019-L под фильтр	1шт.			Зеркало с подсветкой	1шт.	https://www.instagram.com/zerkala.minsk?igsh=a3h2dWg2Mzk5c2Ns
№12		Дозатор для моющих средств Paulmark Kraft D003-CR / D003-BS	1шт.			Зеркало	1шт.	https://www.instagram.com/zerkala.minsk?igsh=a3h2dWg2Mzk5c2Ns
						Фотообои		https://vinni.by/ https://signex.by/shirokoformatnaya-pechat/fotooboi
						Радиаторы отопления	2шт.	https://www.instagram.com/h2_belarus?igsh=eHgxYTM30XozdGdl
						Корпусная мебель и кухня под заказ		
						Напольный плинтус	17 шт.	https://vmetre.by/napolnye-pokrytiya/napolnyy-plintus/plintus-napolnyij-mdf-ohz-hm-1540/
						Штукатурка декоративная Marmorino Naturale Fine B.CO/P		https://premiumdecor.by/
				Шторы		https://www.instagram.com/filipova_lana?igsh=N3NrOWhjaWxsam5z		
				Профиля Loconistic	4 шт.	https://kvitney.by/		
				Розетки серии (Vertus)		https://www.instagram.com/altalight.by/		
				Обои		https://minskoboi.by/		

		Дизайн-проект квартиры по ул. Миля 9	Стадия	Лист	Листов
			РП	26	49
Дизайнер	Хворостов А.О.	Спецификации (1:35)			
Заказчик	Юлия и Павел				
Согласовано					
Дата	31.07.2026				

Тёплый пол	5 м²	https://nexi.by/
Молдинги	15 м/п	https://art-karnizy.by/katalog/moldingi-i-ugolki
Столешница и фартук	2750x600мм.	Артикул 8099\Bst (12) 4,2 е1- Компакт плита
		Duoto Blanco 1000x3000x5.6mm Артикул 78DU41P (50-60) – Керамогранит https://coverlam.by/product/duoto-blanco-1000x3000x5-6mm/

		Дизайн-проект квартиры по ул. Миля 9	Стадия	Лист	Листов
			РП	27	49
Дизайнер	Хворостов А.О.	Спецификации (1:35)			
Заказчик	Юлия и Павел				
Согласовано					
Дата	31.07.2026				



Подвесной светильник
Jemstone 5084/5L

Кольцевые люстры и
светильники CASPIAN два кольца
или аналог из Китая.

Артикул: 5-103 (5-102 color 1)

ЛДСП Эггер Дуб Корбридж
серый H3156 ST12

APL.648.11.10
Бра настенное светодиодное Arloyt Stefa

		Дизайн-проект квартиры по ул. Миля 9	Стадия	Лист	Листов
			РП	28	49
Дизайнер	Хворостов А.О.	3D эскизы (1:35)			
Заказчик	Юлия и Павел				
Согласовано					
Дата	31.07.2026				



ЛДСП Эггер Дуб Корбридж
серый Н3156 ST12

Подвесной дизайнерский светильник
Flamingo 1530 by Vibia

ЛДСП Эггер Дуб Корбридж
серый Н3156 ST12



Tribeca Sage Green 6x24.6

Подвесной светильник
Cisterna by Romatti 22x37
или аналог в Китае

ЛДСП Эггер
Дуб Корбридж
серый Н3156 ST12

		Дизайн-проект квартиры по ул. Миля 9	Стадия	Лист	Листов
			РП	29	49
Дизайнер	Хворостов А.О.	3D эскизы (1:35)			
Заказчик	Юлия и Павел				
Согласовано					
Дата	31.07.2026				



ЛДСП Эггер Шелк серый
U707 ST9

ЛДСП Эггер
Дуб Кордридз
серый H3156 ST12

		Дизайн-проект квартиры по ул. Миля 9	Стадия	Лист	Листов
			РП	30	49
Дизайнер	Хворостов А.О.	3D эскизы (1:35)			
Заказчик	Юлия и Павел				
Согласовано					
Дата	31.07.2026				



		Дизайн-проект квартиры по ул. Миля 9	Стадия	Лист	Листов
			РП	31	49
Дизайнер	Хворостов А.О.	Визуализация кухни-гостиной (1:35)			
Заказчик	Юлия и Павел				
Согласовано					
Дата	31.07.2026				



		Дизайн-проект квартиры по ул. Миля 9	Стадия	Лист	Листов
			РП	32	49
Дизайнер	Хворостов А.О.	Визуализация кухни-гостиной (1:35)			
Заказчик	Юлия и Павел				
Согласовано					
Дата	31.07.2026				



		Дизайн-проект квартиры по ул. Миля 9	Стадия	Лист	Листов
			РП	33	49
Дизайнер	Хворостов А.О.	Визуализация кухни-гостиной (1:35)			
Заказчик	Юлия и Павел				
Согласовано					
Дата	31.07.2026				



		Дизайн-проект квартиры по ул. Миля 9	Стадия	Лист	Листов
			РП	34	49
Дизайнер	Хворостов А.О.	Визуализация кухни-гостиной (1:35)			
Заказчик	Юлия и Павел				
Согласовано					
Дата	31.07.2026				



		Дизайн-проект квартиры по ул. Милыя 9	Стадия	Лист	Листов
			РП	35	49
Дизайнер	Хворостов А.О.	Визуализация кухни-гостиной (1:35)			
Заказчик	Юлия и Павел				
Согласовано					
Дата	31.07.2026				



		Дизайн-проект квартиры по ул. Миля 9	Стадия	Лист	Листов
			РП	36	49
Дизайнер	Хворостов А.О.	Визуализация кухни-гостиной (1:35)			
Заказчик	Юлия и Павел				
Согласовано					
Дата	31.07.2026				



		Дизайн-проект квартиры по ул. Миля 9	Стадия	Лист	Листов
			РП	37	49
Дизайнер	Хворостов А.О.	Визуализация кухни-гостиной (1:35)			
Заказчик	Юлия и Павел				
Согласовано					
Дата	31.07.2026				



		Дизайн-проект квартиры по ул. Миля 9	Стадия	Лист	Листов
			РП	38	49
Дизайнер	Хворостов А.О.	Визуализация кухни-гостиной (1:35)			
Заказчик	Юлия и Павел				
Согласовано					
Дата	31.07.2026				



		Дизайн-проект квартиры по ул. Миля 9	Стадия	Лист	Листов
			РП	39	49
Дизайнер	Хворостов А.О.	Визуализация спальни (1:35)			
Заказчик	Юлия и Павел				
Согласовано					
Дата	31.07.2026				



		Дизайн-проект квартиры по ул. Миля 9	Стадия	Лист	Листов
			РП	40	49
Дизайнер	Хворостов А.О.	Визуализация спальни (1:35)			
Заказчик	Юлия и Павел				
Согласовано					
Дата	31.07.2026				



		Дизайн-проект квартиры по ул. Миля 9	Стадия	Лист	Листов
			РП	41	49
Дизайнер	Хворостов А.О.	Визуализация спальни (1:35)			
Заказчик	Юлия и Павел				
Согласовано					
Дата	31.07.2026				




		Дизайн-проект квартиры по ул. Миля 9	Стадия	Лист	Листов
			РП	42	49
Дизайнер	Хворостов А.О.	Визуализация детской комнаты (1:35)			
Заказчик	Юлия и Павел				
Согласовано					
Дата	31.07.2026				



		Дизайн-проект квартиры по ул. Миля 9	Стадия	Лист	Листов
			РП	43	49
Дизайнер	Хворостов А.О.	Визуализация детской комнаты (1:35)			
Заказчик	Юлия и Павел				
Согласовано					
Дата	31.07.2026				



		Дизайн-проект квартиры по ул. Миля 9	Стадия	Лист	Листов
			РП	44	49
Дизайнер	Хворостов А.О.	Визуализация детской комнаты (1:35)			
Заказчик	Юлия и Павел				
Согласовано					
Дата	31.07.2026				

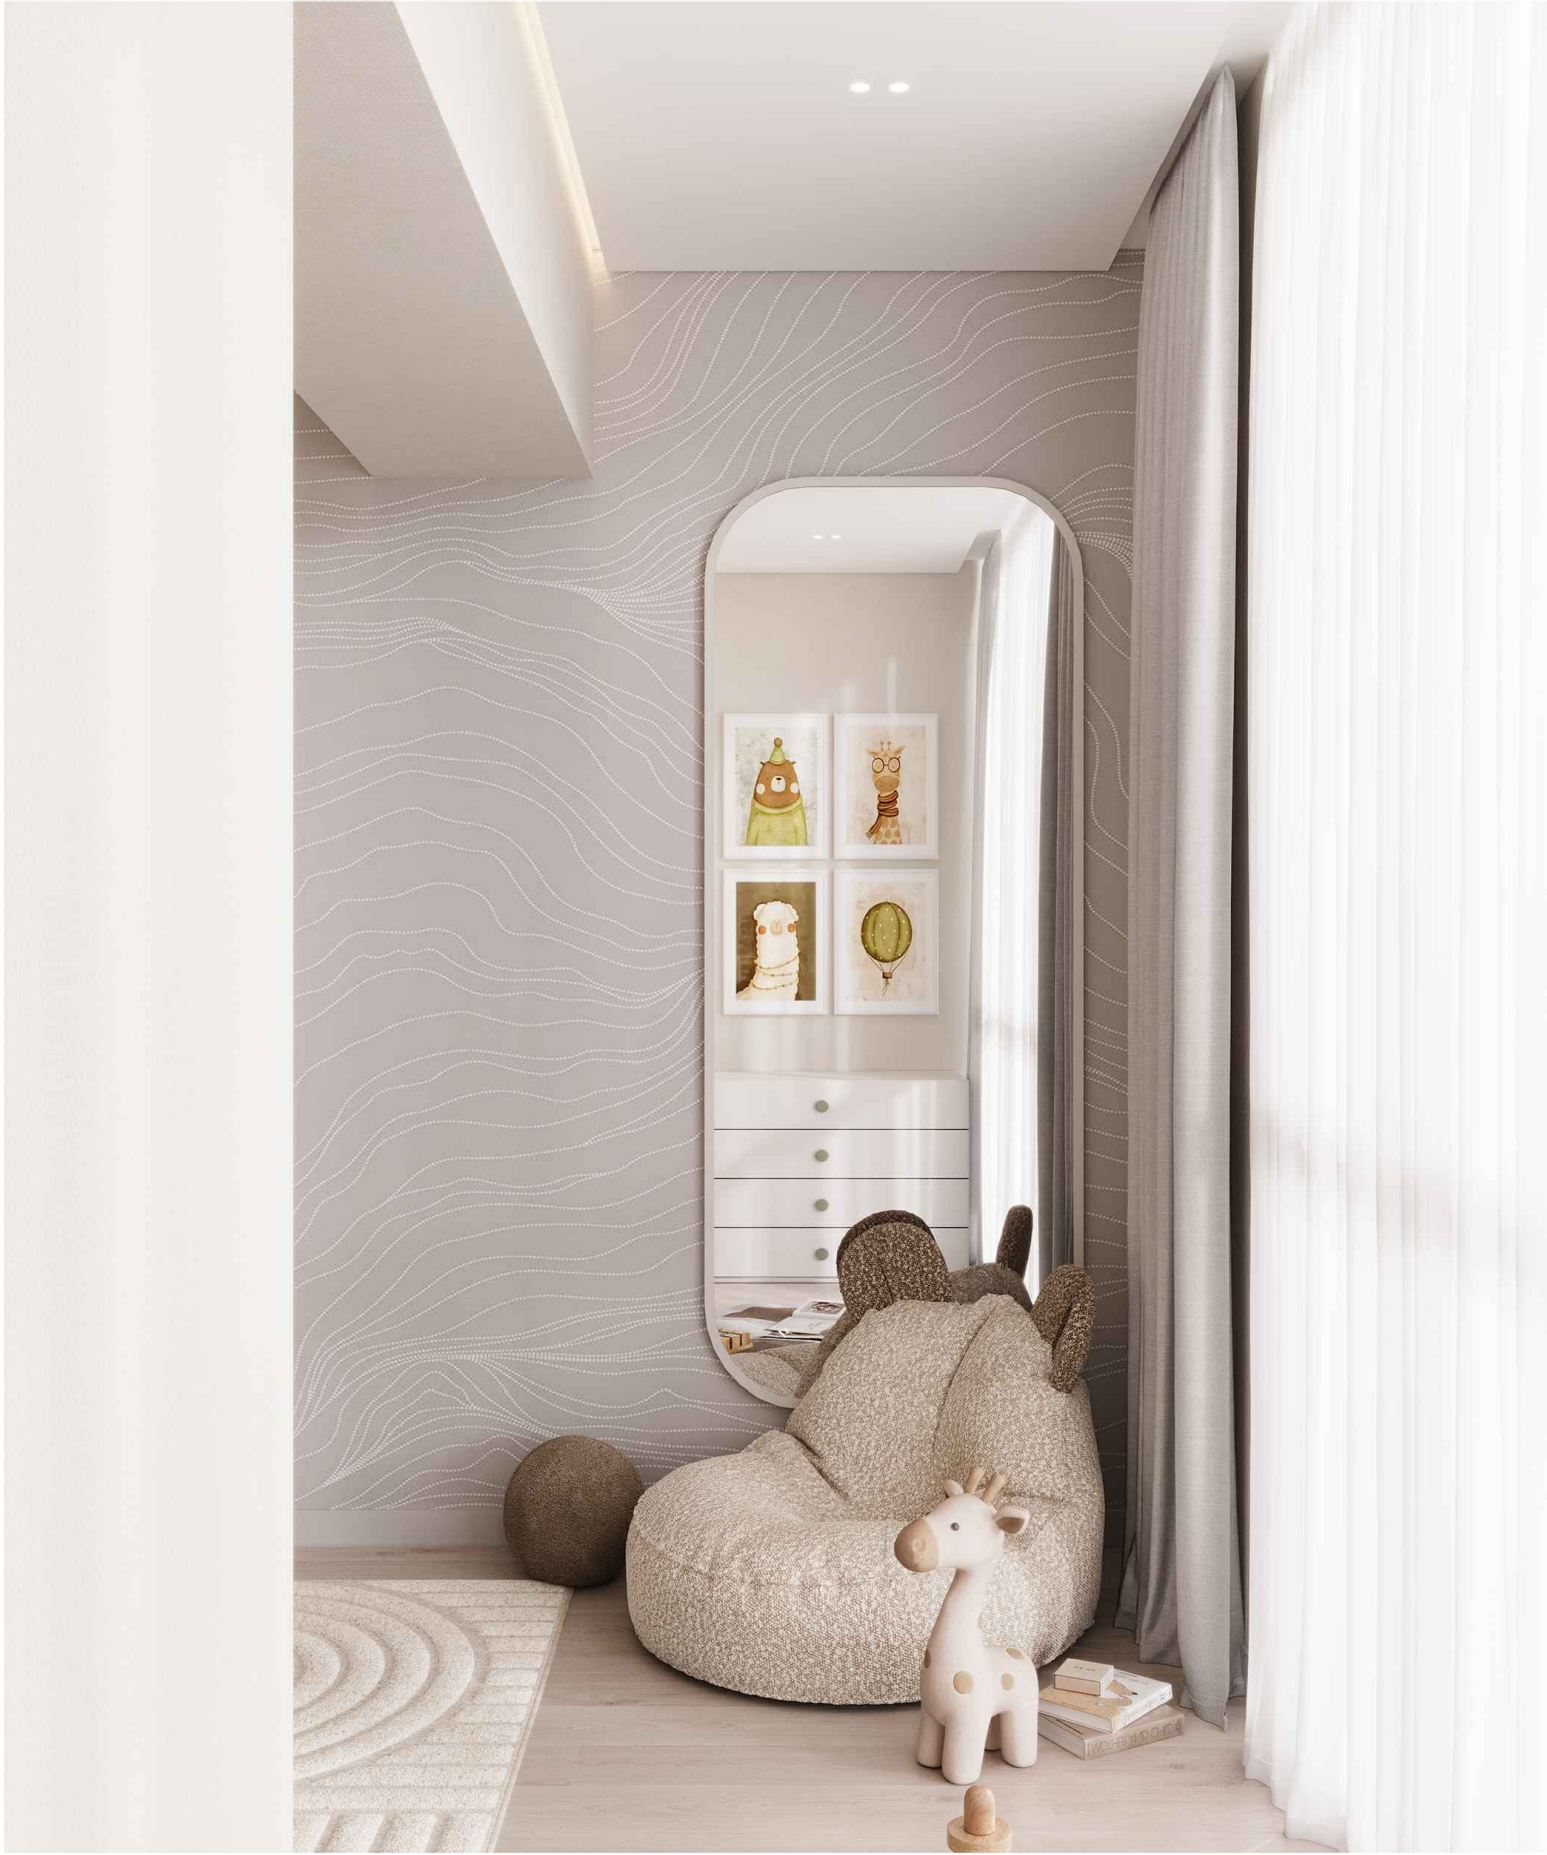

		Дизайн-проект квартиры по ул. Миля 9	Стадия	Лист	Листов
			РП	45	49
Дизайнер	Хворостов А.О.	Визуализация детской комнаты (1:35)			
Заказчик	Юлия и Павел				
Согласовано					
Дата	31.07.2026				



		Дизайн-проект квартиры по ул. Миля 9	Стадия	Лист	Листов
			РП	46	49
Дизайнер	Хворостов А.О.	Визуализация детской комнаты			
Заказчик	Юлия и Павел				
Согласовано					
Дата	31.07.2026				



		Дизайн-проект квартиры по ул. Миля 9	Стадия	Лист	Листов
			РП	47	49
Дизайнер	Хворостов А.О.	Визуализация санузла			
Заказчик	Юлия и Павел				
Согласовано					
Дата	31.07.2026				



		Дизайн-проект квартиры по ул. Миля 9	Стадия	Лист	Листов
			РП	48	49
Дизайнер	Хворостов А.О.	Визуализация санузла			
Заказчик	Юлия и Павел				
Согласовано					
Дата	31.07.2026				



		Дизайн-проект квартиры по ул. Миля 9	Стадия	Лист	Листов
			РП	49	49
Дизайнер	Хворостов А.О.	Визуализация санузла			
Заказчик	Юлия и Павел				
Согласовано					
Дата	31.07.2026				